A-0

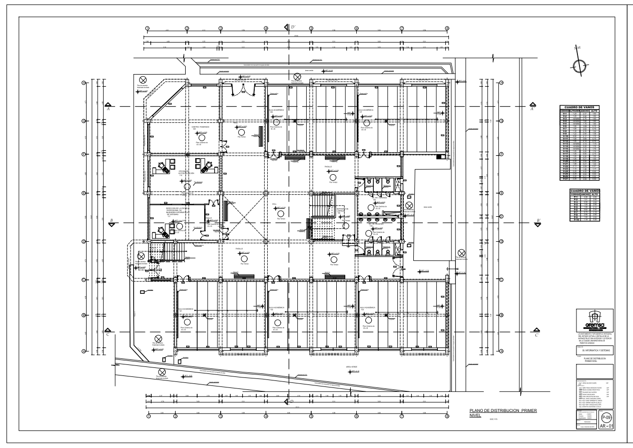

A-0

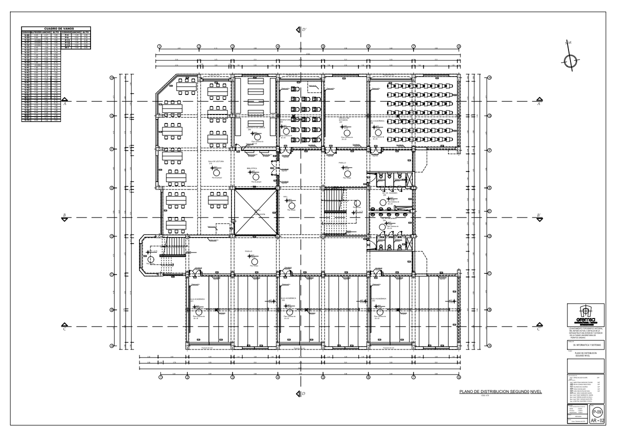

A-0

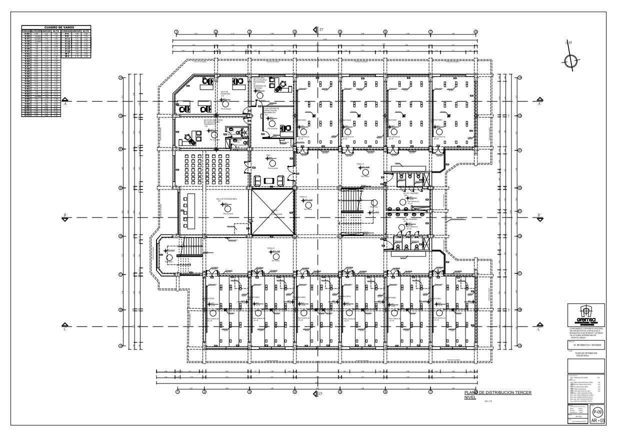

A-0

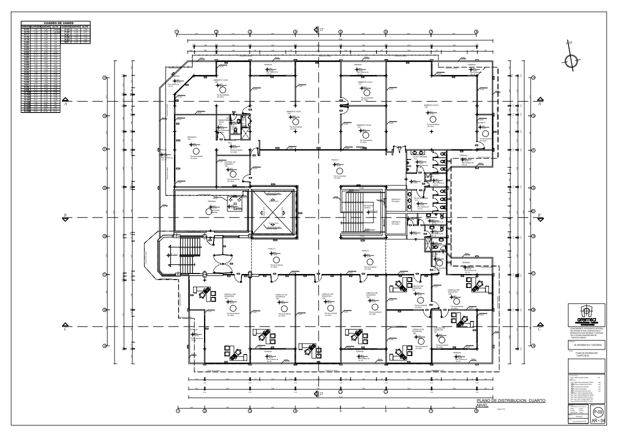

A-0

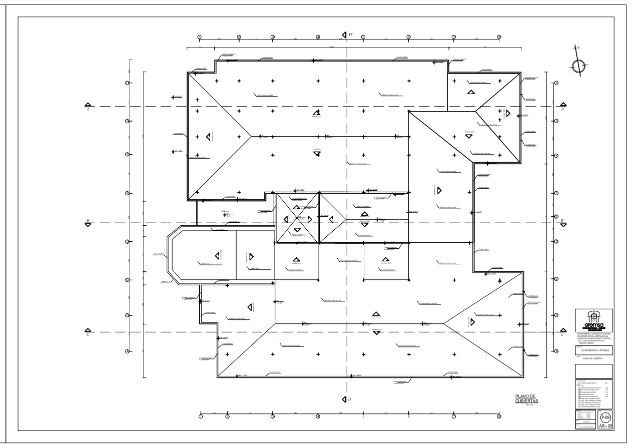

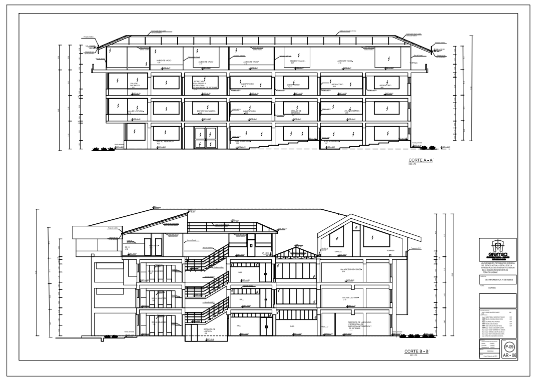

A-1

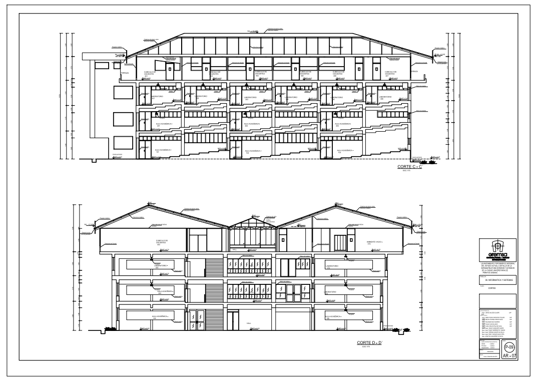

A-1

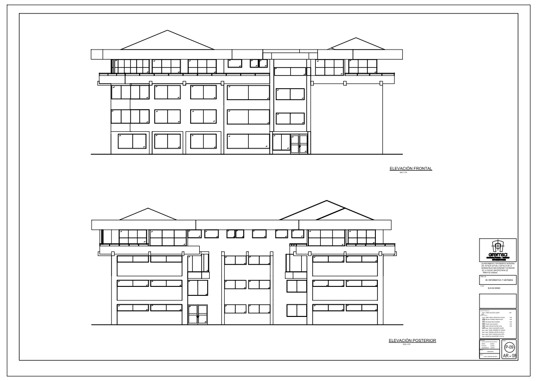

A-1

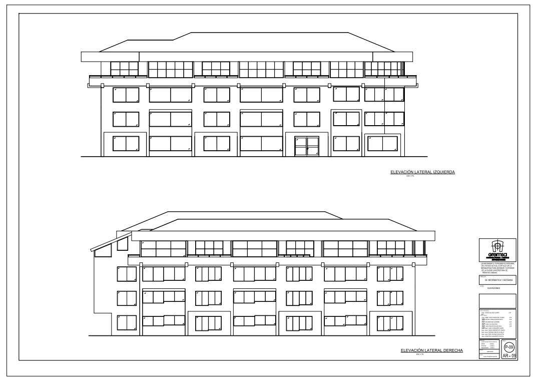

A-1

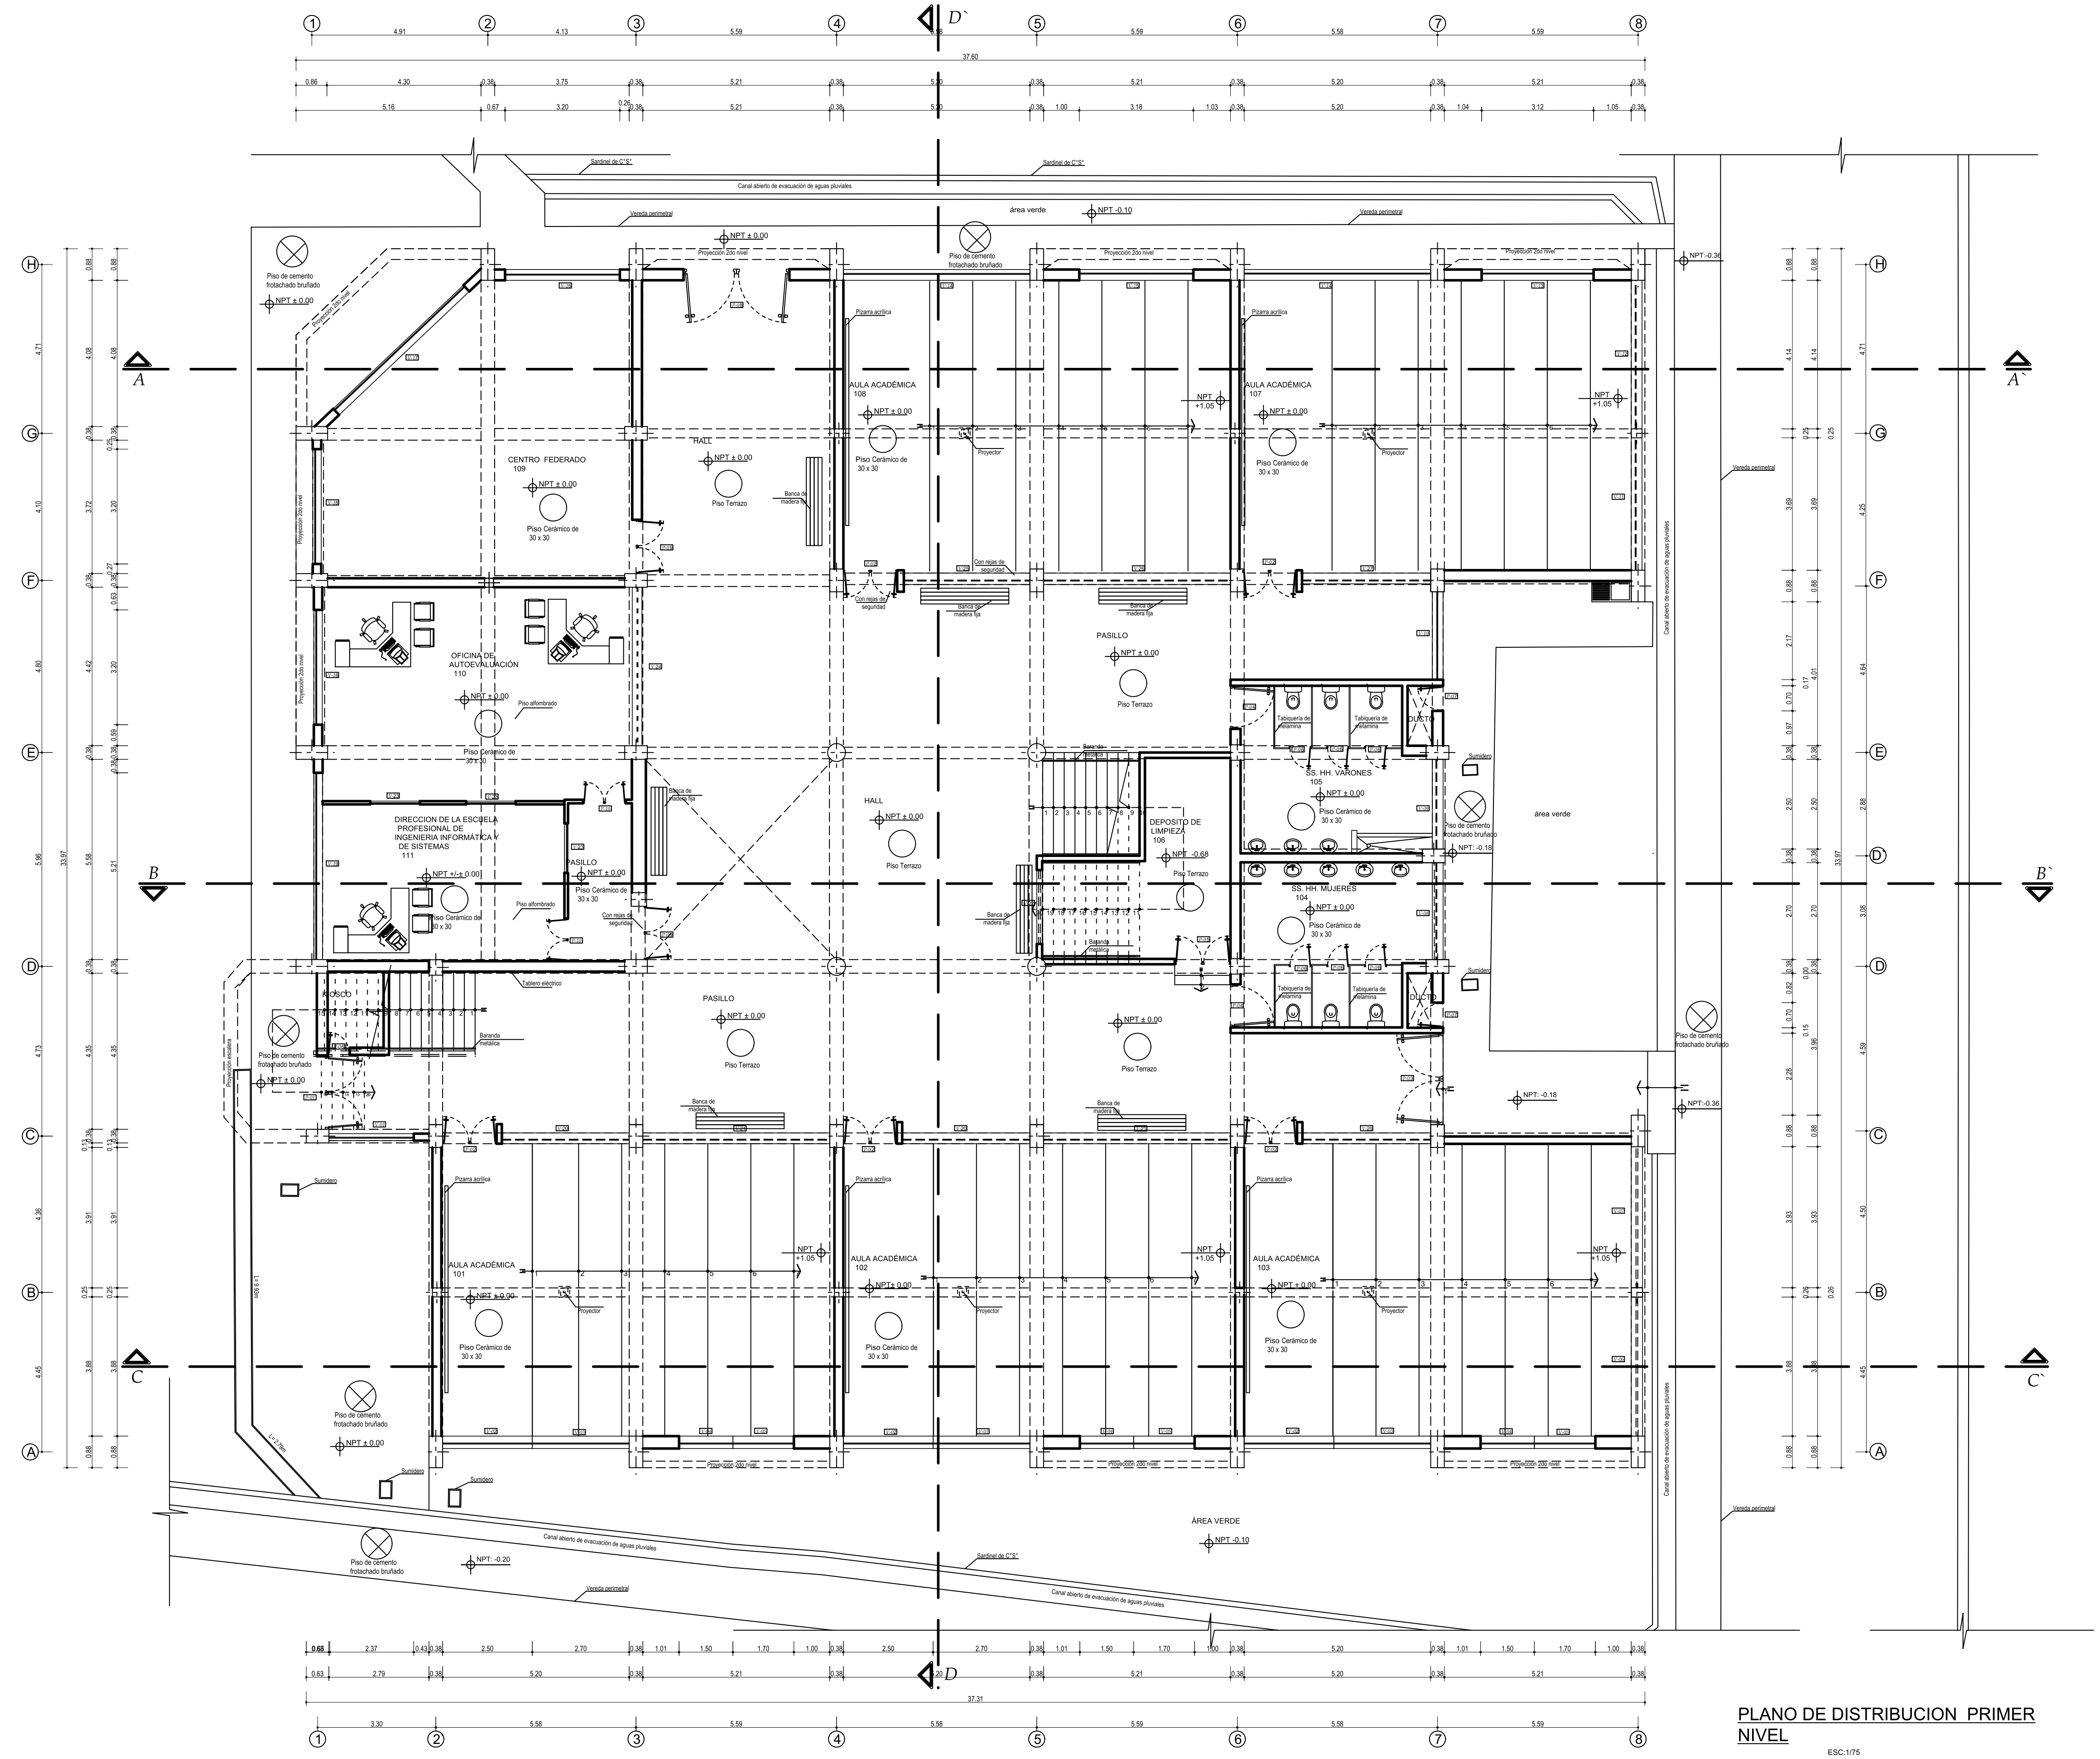

PLANO DE DISTRIBUCION PRIMER NIVEL

ESC:1/75

CUADRO DE VANOS			
CODIGO	**ALFEIZER**	**ANCHO**	**ALTO**
V-1	1.20	2.37	1.60
V-2	1.20	2.50	1.60
V-3	variable	2.70	1.60
V-4	variable	1.50	1.60
V-5	variable	1.70	1.60
V-6	1.80	3.88	0.75
V-7	1.80	3.93	0.75
V-8	1.30	2.70	1.30
V-9	1.22	2.50	1.38
V-10	0.90	2.17	1.70
V-11	1.80	3.69	0.75
V-12	1.85	4.14	0.75
V-13	variable	3.12	1.75
V-14	variable	5.20	1.75
V-15	variable	3.18	1.75
V-16	1.05	3.20	1.75
V-17	1.05	5.00	2.15
V-18	1.05	3.20	1.55
V-19	1.05	5.21	1.55
V-20	2.28	3.55	0.52
V-21	1.98	5.21	1.22
V-22	2.13	2.06	0.47
V-23	1.10	1.38	1.17
V-24	2.28	4.42	0.52
V-25	2.28	3.52	0.52
V-26	2.28	5.21	0.52
V-27	2.28	3.59	0.52

CUADRO DE VANOS		
CODIGO	**ANCHO**	**ALTO**
P-1	2.08	2.60
P-2	1.51	2.80
P-3	2.55	2.60
P-4	1.00	2.80
P-5	1.55	2.10
P-6	0.62	2.50
P-7	0.70	1.75
P-8	2.95	2.80
P-9	1.50	2.60
P-10	1.19	3.20

gremsa
CONSULTORIA - OBRAS
INVERSIONES

LEVANTAMIENTO TOPOGRÁFICO INTEGRAL DEL ESTADO ACTUAL A DETALLE DE LA INFRAESTRUCTURA INTERIOR Y EXTERIOR DE LA CIUDAD UNIVERSITARIA DE PERAYOC-UNSAAC

PABELLON:
09. INFORMATICA Y SISTEMAS

PLANO:
PLANO DE DISTRIBUCION
PRIMER NIVEL

JEFE DE PROYECTO:
Arqto° JORGE SALCEDO QUISPE CAP 5812

EQUIPO TÉCNICO:
Arqto° AMED TEDILIO MOSCOSO TOLEDO CAP 13006
Arqta° NÉLIDA COANQUI SINCHI ROCA CAP 12517
Arqta° SOLANGE DIAZ CACERES CAP 12616
Arqta° VILMA CUSI DELGADO CAP 12615
Arqto° JUAN CARLOS PAUCAR VEGA CAP 11059
Bach. Arqta° JANIA CUSIQUISPE QUISPE
Bach. Arqto° DANDY BARRIENTOS RAMOS
Bach. Arqta° ADRIANA AIQUIPA ALOSILLA
Bach. Arqto° KENY CHOQUE INCACUTIPA
Asist. JHONATAN CASAVERDE CCOICCA

UBICACION:
CIUDAD UNIVERSITARIA DE PERAYOC
Distrito : CUSCO
Provincia : CUSCO
Departamento : CUSCO

ESCALA:
INDICADAS

FECHA:
Cusco, Diciembre del 2016

LAMINA:
P-09
AR - 01

CUADRO DE VANOS

CODIGO	ALFEIZER	ANCHO	ALTO
V-28	0.40	2.37	1.60
V-29	0.80	2.50	1.60
V-30	variable	2.70	1.60
V-31	variable	1.50	1.60
V-32	variable	1.70	1.60
V-33	0.45	3.88	0.75
V-34	0.45	3.93	0.75
V-35	0.71	2.55	1.54
V-36	1.26	2.70	0.99
V-37	1.26	2.50	0.99
V-38	0.71	2.45	1.54
V-39	1.68	3.50	0.72
V-40	variable	3.50	0.75
V-41	1.85	3.69	0.75
V-42	1.50	4.14	0.75
V-43	0.80	3.12	1.60
V-44	0.80	5.20	1.60
V-45	0.80	3.18	1.60
V-46	0.80	3.20	1.60
V-47	0.80	2.62	1.60
V-48	0.80	3.50	1.60
V-49	0.80	2.55	1.60
V-50	0.65	5.24	1.60
V-51	1.00	3.00	1.18
V-52	1.68	3.55	0.72
V-53	1.68	5.21	0.72
V-54	1.68	3.60	0.72
V-55	1.68	3.58	0.72
V-56	0.45	0.30	1.80
V-57	0.45	0.45	1.80
V-58	0.44	5.03	1.96
V-59	0.44	5.46	1.81
V-60	1.00	0.60	1.40
V-61	1.68	3.71	0.72
V-74	0.44	1.30	1.81

CODIGO	ANCHO	ALTO
P-4	1.00	2.80
P-6	0.62	2.50
P-11	1.51	2.40
P-12	1.89	2.25
P-13	0.82	2.80
M-1	1.49	2.60

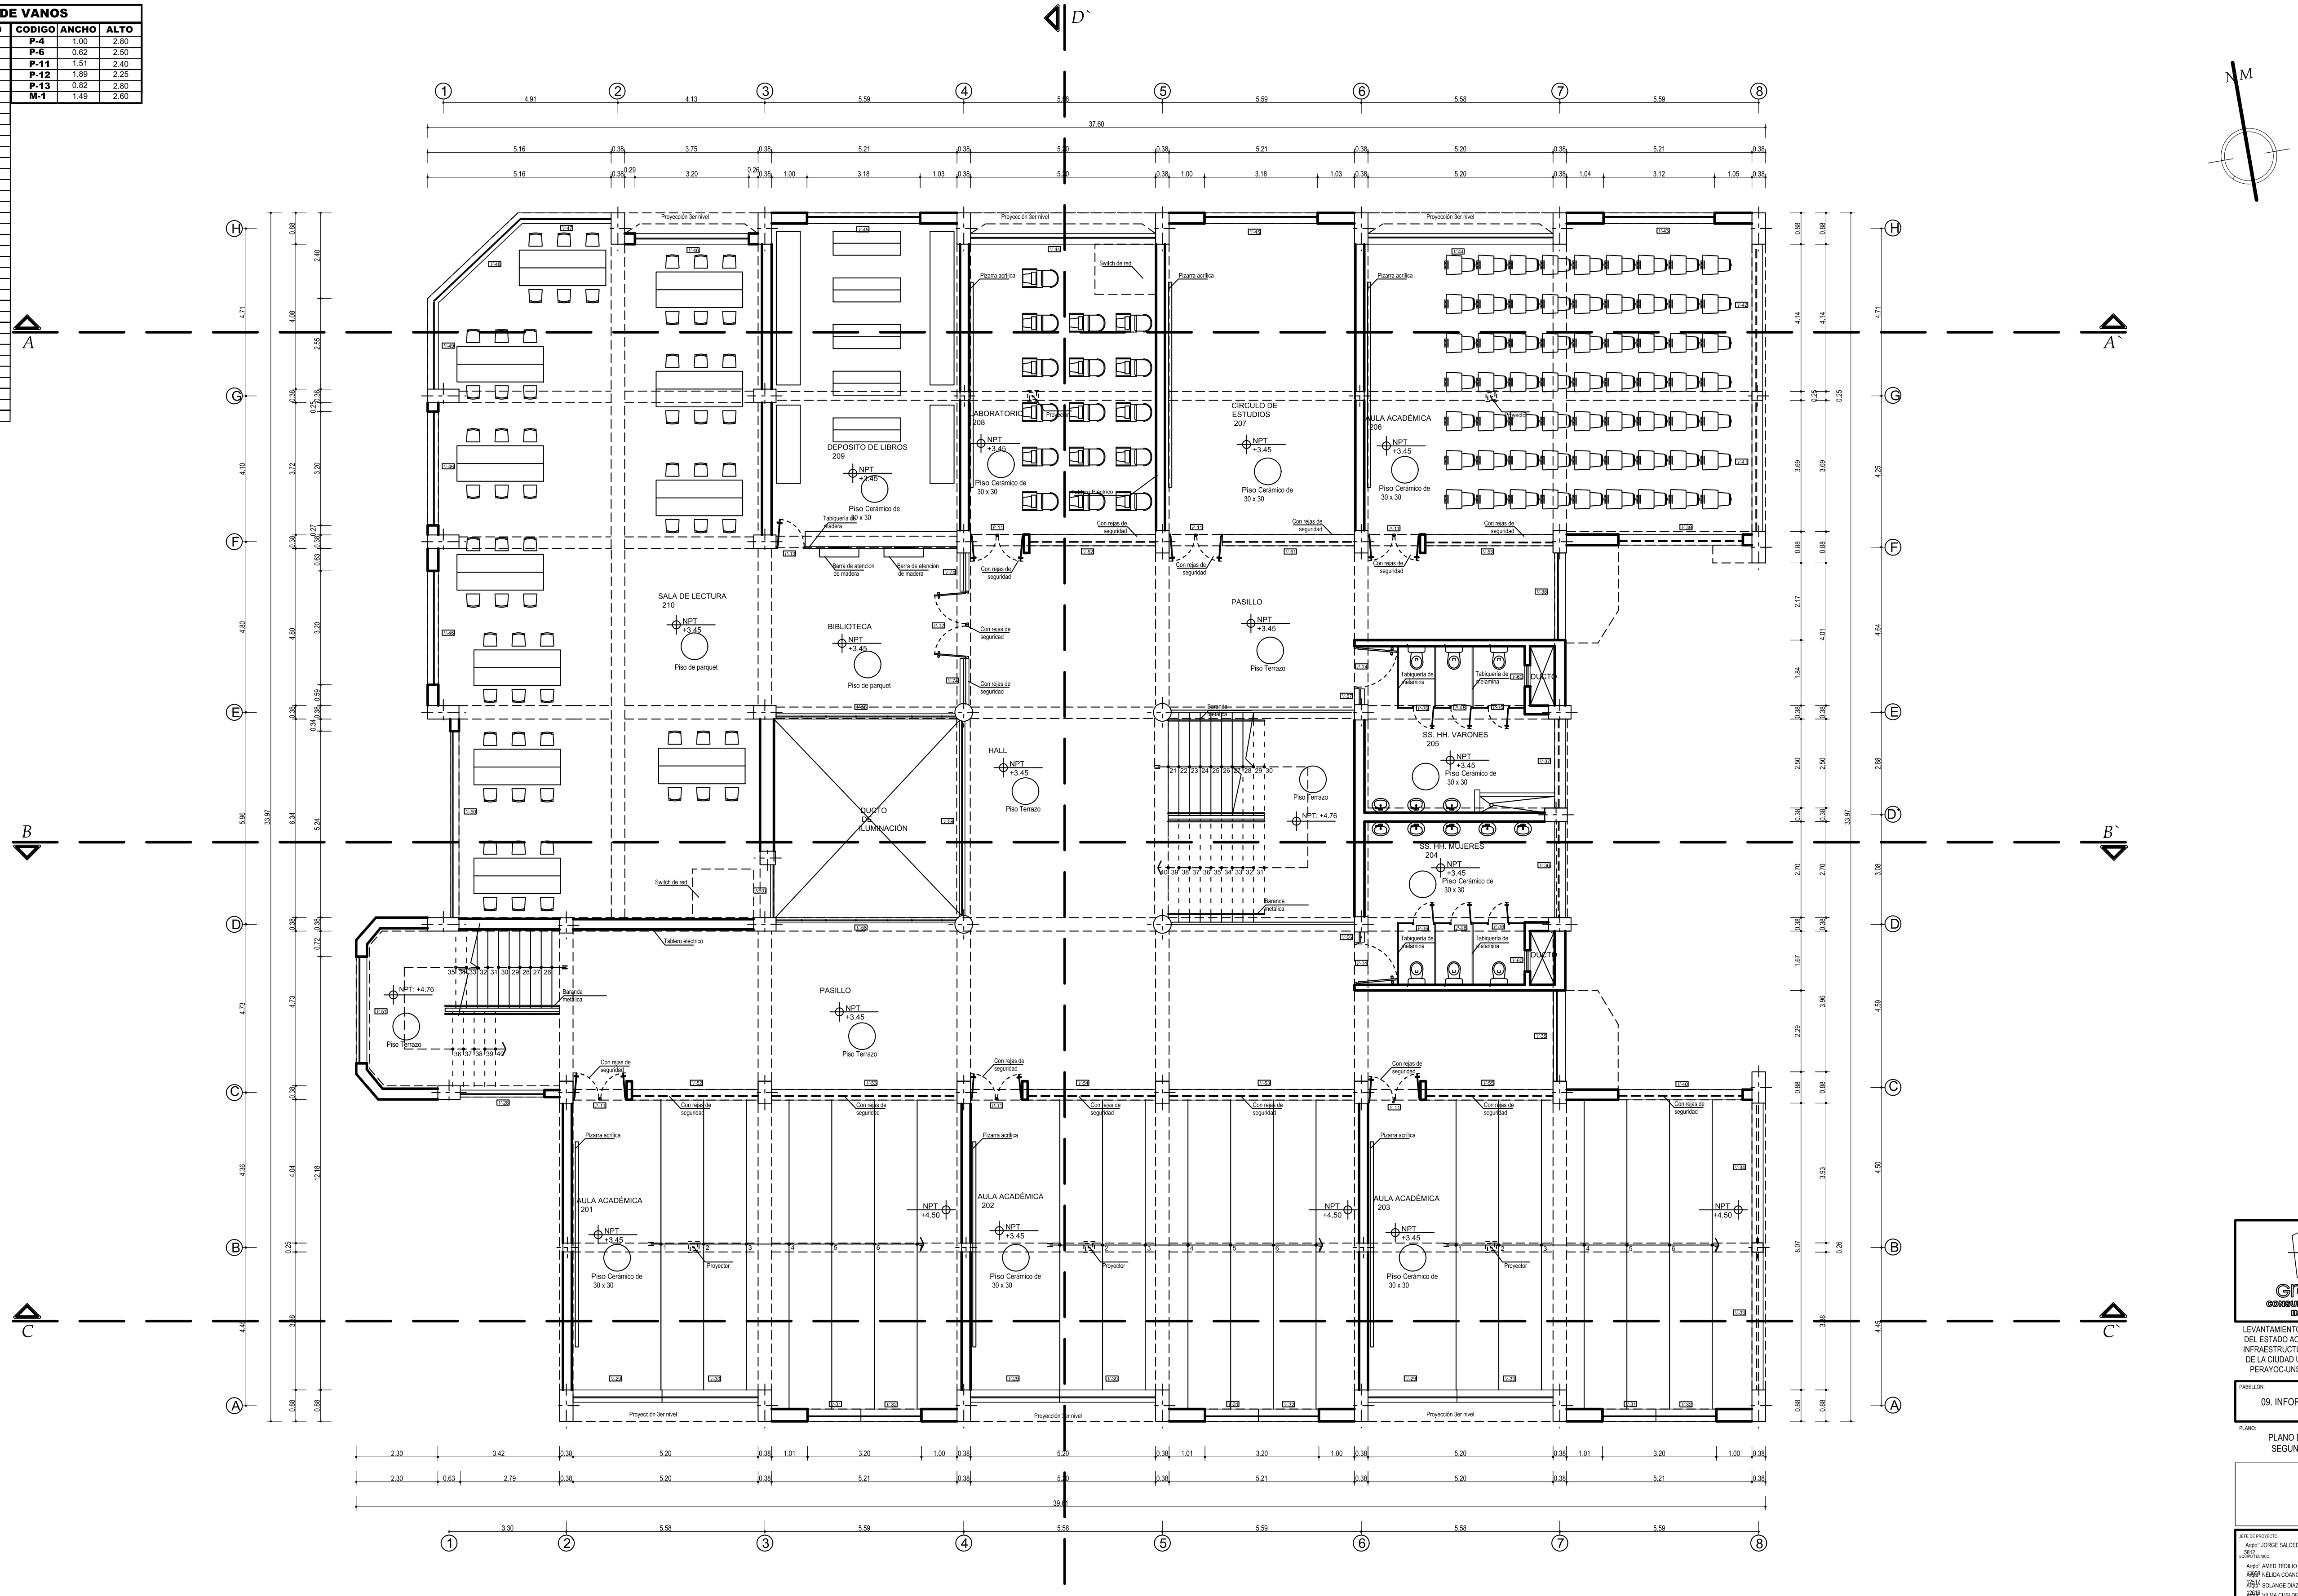

PLANO DE DISTRIBUCION SEGUNDO NIVEL

ESC:1/75

gremsa
CONSULTORIA - OBRAS
INVERSIONES

LEVANTAMIENTO TOPOGRÁFICO INTEGRAL
DEL ESTADO ACTUAL A DETALLE DE LA
INFRAESTRUCTURA INTERIOR Y EXTERIOR
DE LA CIUDAD UNIVERSITARIA DE
PERAYOC-UNSAAC

PABELLON:
09. INFORMATICA Y SISTEMAS

PLANO:
PLANO DE DISTRIBUCION
SEGUNDO NIVEL

JEFE DE PROYECTO:
Arqto° JORGE SALCEDO QUISPE CAP 5812

EQUIPO TÉCNICO:
Arqto° AMED TEDILIO MOSCOSO TOLEDO CAP 13006
Arqta° NÉLIDA COANQUI SINCHI ROCA CAP 12517
Arqta° SOLANGE DIAZ CACERES CAP 12616
Arqta° VILMA CUSI DELGADO CAP 12615
Arqto° JUAN CARLOS PAUCAR VEGA CAP 11059
Bach. Arqta° JANIA CUSIQUISPE QUISPE
Bach. Arqto° DANDY BARRIENTOS RAMOS
Bach. Arqta° ADRIANA AIQUIPA ALOSILLA
Bach. Arqto° KENY CHOQUE INCACUTIPA
Asist. JHONATAN CASAVERDE CCOICCA

UBICACION:
CIUDAD UNIVERSITARIA DE PERAYOC
Distrito : CUSCO
Provincia : CUSCO
Departamento : CUSCO

ESCALA:
INDICADAS

FECHA:
Cusco, Diciembre del 2016

LAMINA:
P-09
AR - 02

CUADRO DE VANOS

CODIGO	ALFEIZER	ANCHO	ALTO	CODIGO	ANCHO	ALTO
V-29	0.80	2.50	1.60	**P-4**	1.00	2.80
V-30	variable	2.70	1.60	**P-6**	0.62	2.50
V-31	variable	1.50	1.60	**P-11**	1.51	2.40
V-32	variable	1.70	1.60	**P-14**	1.89	2.25
V-36	1.26	2.70	0.99	**P-15**	0.90	2.80
V-37	1.26	2.50	0.99	**P-16**	0.95	2.25
V-39	1.68	3.50	0.72	**P-17**	0.80	2.80
V-41	1.85	3.69	0.75	**P-18**	1.50	2.25
V-42	1.50	4.14	0.75	**M-1**	1.49	2.60
V-43	0.80	3.12	1.60	**M-3**	4.16	2.08
V-44	0.80	5.20	1.60			
V-45	0.80	3.18	1.60			
V-46	0.80	3.20	1.60			
V-47	0.80	2.62	1.60			
V-48	0.80	3.50	1.60			
V-49	0.80	2.55	1.60			
V-50	0.80	5.24	1.60			
V-56	0.45	0.30	1.80			
V-57	0.45	0.45	1.80			
V-58	0.44	5.03	1.96			
V-59	0.44	5.46	1.81			
V-60	1.00	0.60	1.40			
V-62	0.40	2.37	1.60			
V-63	1.05	3.88	0.75			
V-64	1.05	3.93	0.75			
V-65	variable	3.48	0.75			
V-66	1.00	3.00	1.86			
V-67	1.90	3.55	0.50			
V-68	1.90	359	0.50			
V-69	1.90	3.60	0.50			
V-70	1.90	3.58	0.50			
V-71	1.66	3.70	0.74			
V-72	0.95	1.75	1.30			
V-73	1.00	0.80	1.30			

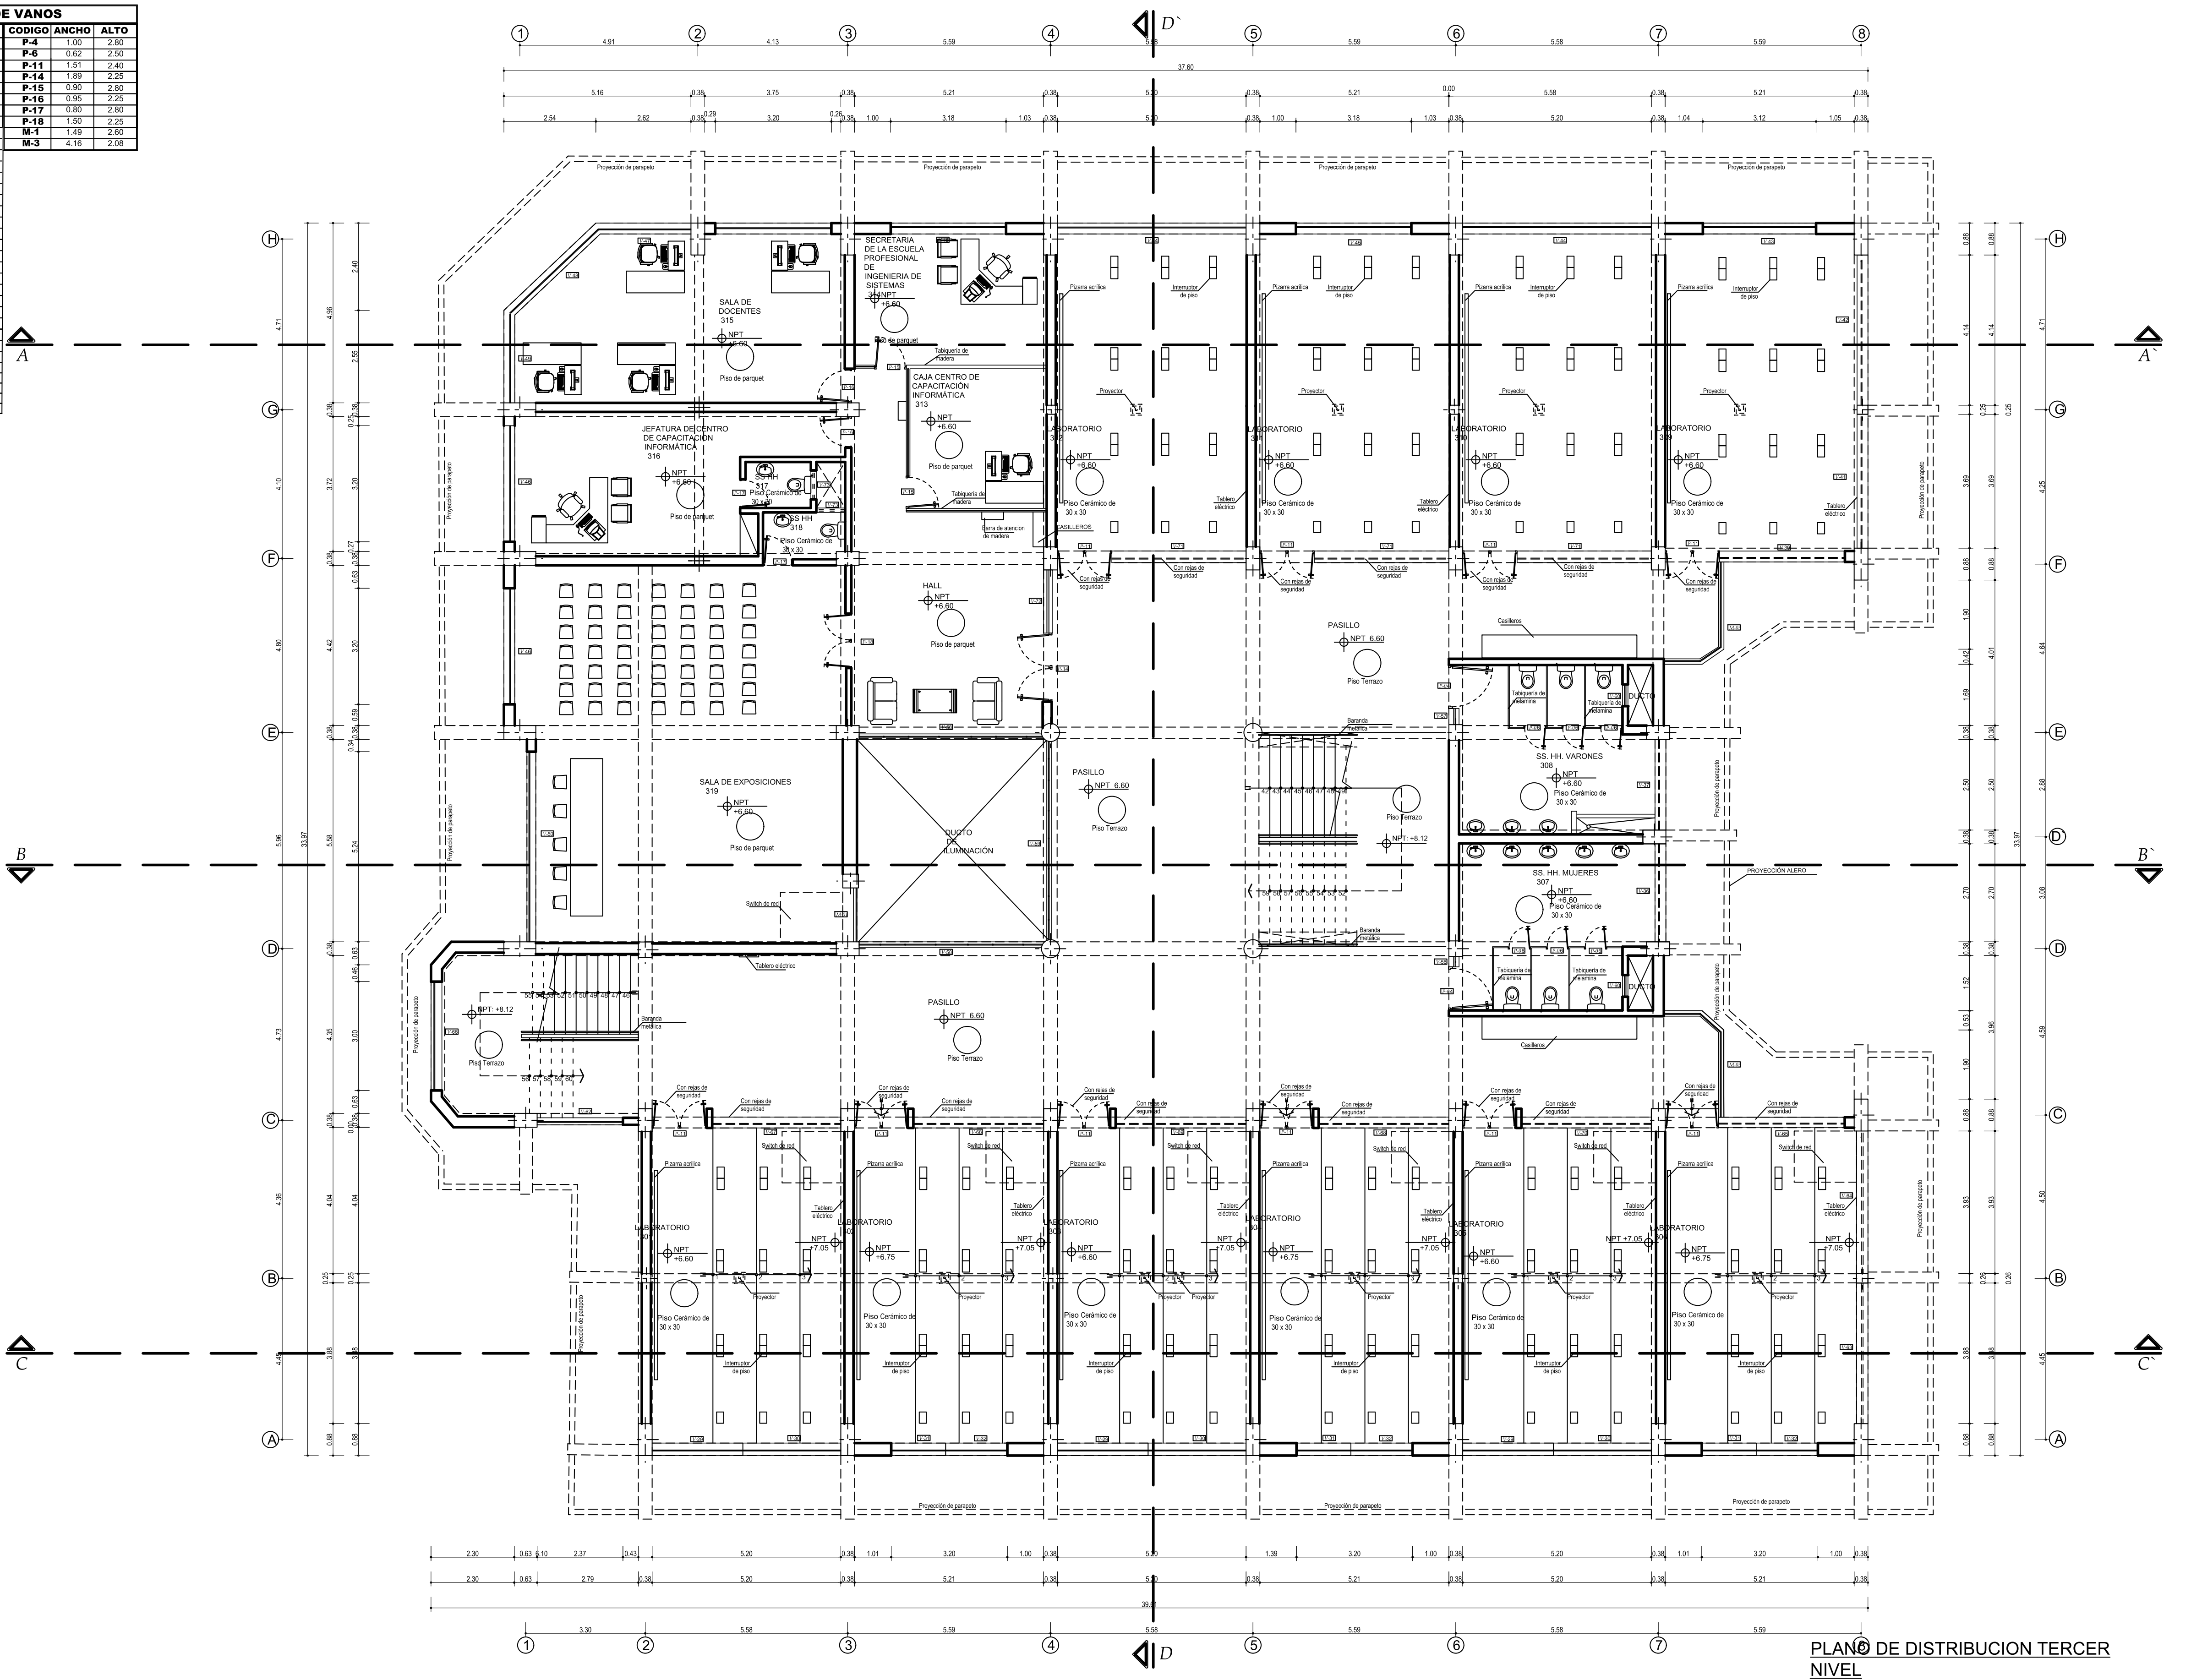

PLANO DE DISTRIBUCION TERCER NIVEL

ESC:1/75

gremsa
CONSULTORIA - OBRAS
INVERSIONES

LEVANTAMIENTO TOPOGRÁFICO INTEGRAL DEL ESTADO ACTUAL A DETALLE DE LA INFRAESTRUCTURA INTERIOR Y EXTERIOR DE LA CIUDAD UNIVERSITARIA DE PERAYOC-UNSAAC

PABELLON:
09. INFORMATICA Y SISTEMAS

PLANO:
PLANO DE DISTRIBUCION
TERCER NIVEL

JEFE DE PROYECTO:
Arqto° JORGE SALCEDO QUISPE CAP 5812
EQUIPO TÉCNICO:
Arqto° AMED TEDILIO MOSCOSO TOLEDO CAP 13006
Arqta° NÉLIDA COANQUI SINCHI ROCA CAP 12517
Arqta° SOLANGE DIAZ CACERES CAP 12616
Arqta° VILMA CUSI DELGADO CAP 12615
Arqto° JUAN CARLOS PAUCAR VEGA CAP 11059
Bach. Arqta° JANIA CUSIQUISPE QUISPE
Bach. Arqto° DANDY BARRIENTOS RAMOS
Bach. Arqta° ADRIANA AIQUIPA ALOSILLA
Bach. Arqto° KENY CHOQUE INCACUTIPA
Asist. JHONATAN CASAVERDE CCOICCA

UBICACION:
CIUDAD UNIVERSITARIA DE PERAYOC
Distrito : CUSCO
Provincia : CUSCO
Departamento : CUSCO

ESCALA:
INDICADAS

FECHA:
Cusco, Diciembre del 2016

LAMINA:
P-09
AR - 03

CUADRO DE VANOS						
CODIGO	ALFEIZER	ANCHO	ALTO	CODIGO	ANCHO	ALTO
V-75	1.20	1.34	variable	P-19	1.00	2.80
V-76	1.20	0.78	variable	P-20	2.40	2.87
V-77	1.20	1.40	1.67	P-21	1.00	2.15
V-78	1.20	2.04	1.67	P-22	1.00	2.10
V-79	1.20	2.26	1.67	P-23	1.62	2.80
V-80	1.20	2.24	1.67	M-2	2.02	2.87
V-81	1.20	2.25	1.67			
V-82	1.20	3.30	1.67			
V-83	1.20	1.20	1.67			
V-84	0.31	2.40	2.56			
V-85	0.72	4.25	2.15			
V-86	0.31	3.20	2.56			
V-87	0.72	5.50	2.15			
V-88	0.72	3.62	2.15			
V-89	1.20	3.20	1.67			
V-90	1.95	1.60	0.92			
V-91	1.72	1.62	1.00			
V-92	1.69	0.77	0.90			
V-93	1.70	0.77	1.99			
V-94	1.72	1.62	1.00			
V-95	1.69	1.62	0.89			
V-96	1.69	1.63	0.89			
V-97	0.31	2.66	2.56			
V-98	0.31	3.33	2.56			
V-99	0.31	1.29	2.56			
V-100	0.31	1.99	2.56			
V-101	0.31	2.16	2.56			
V-102	0.31	3.19	2.56			
V-103	0.31	2.74	2.56			
V-104	1.20	4.33	1.67			
V-105	1.20	5.80	1.67			
V-106	1.75	5.50	1.67			
V-107	0.70	5.67	2.17			
V-108	0.70	6.14	2.17			

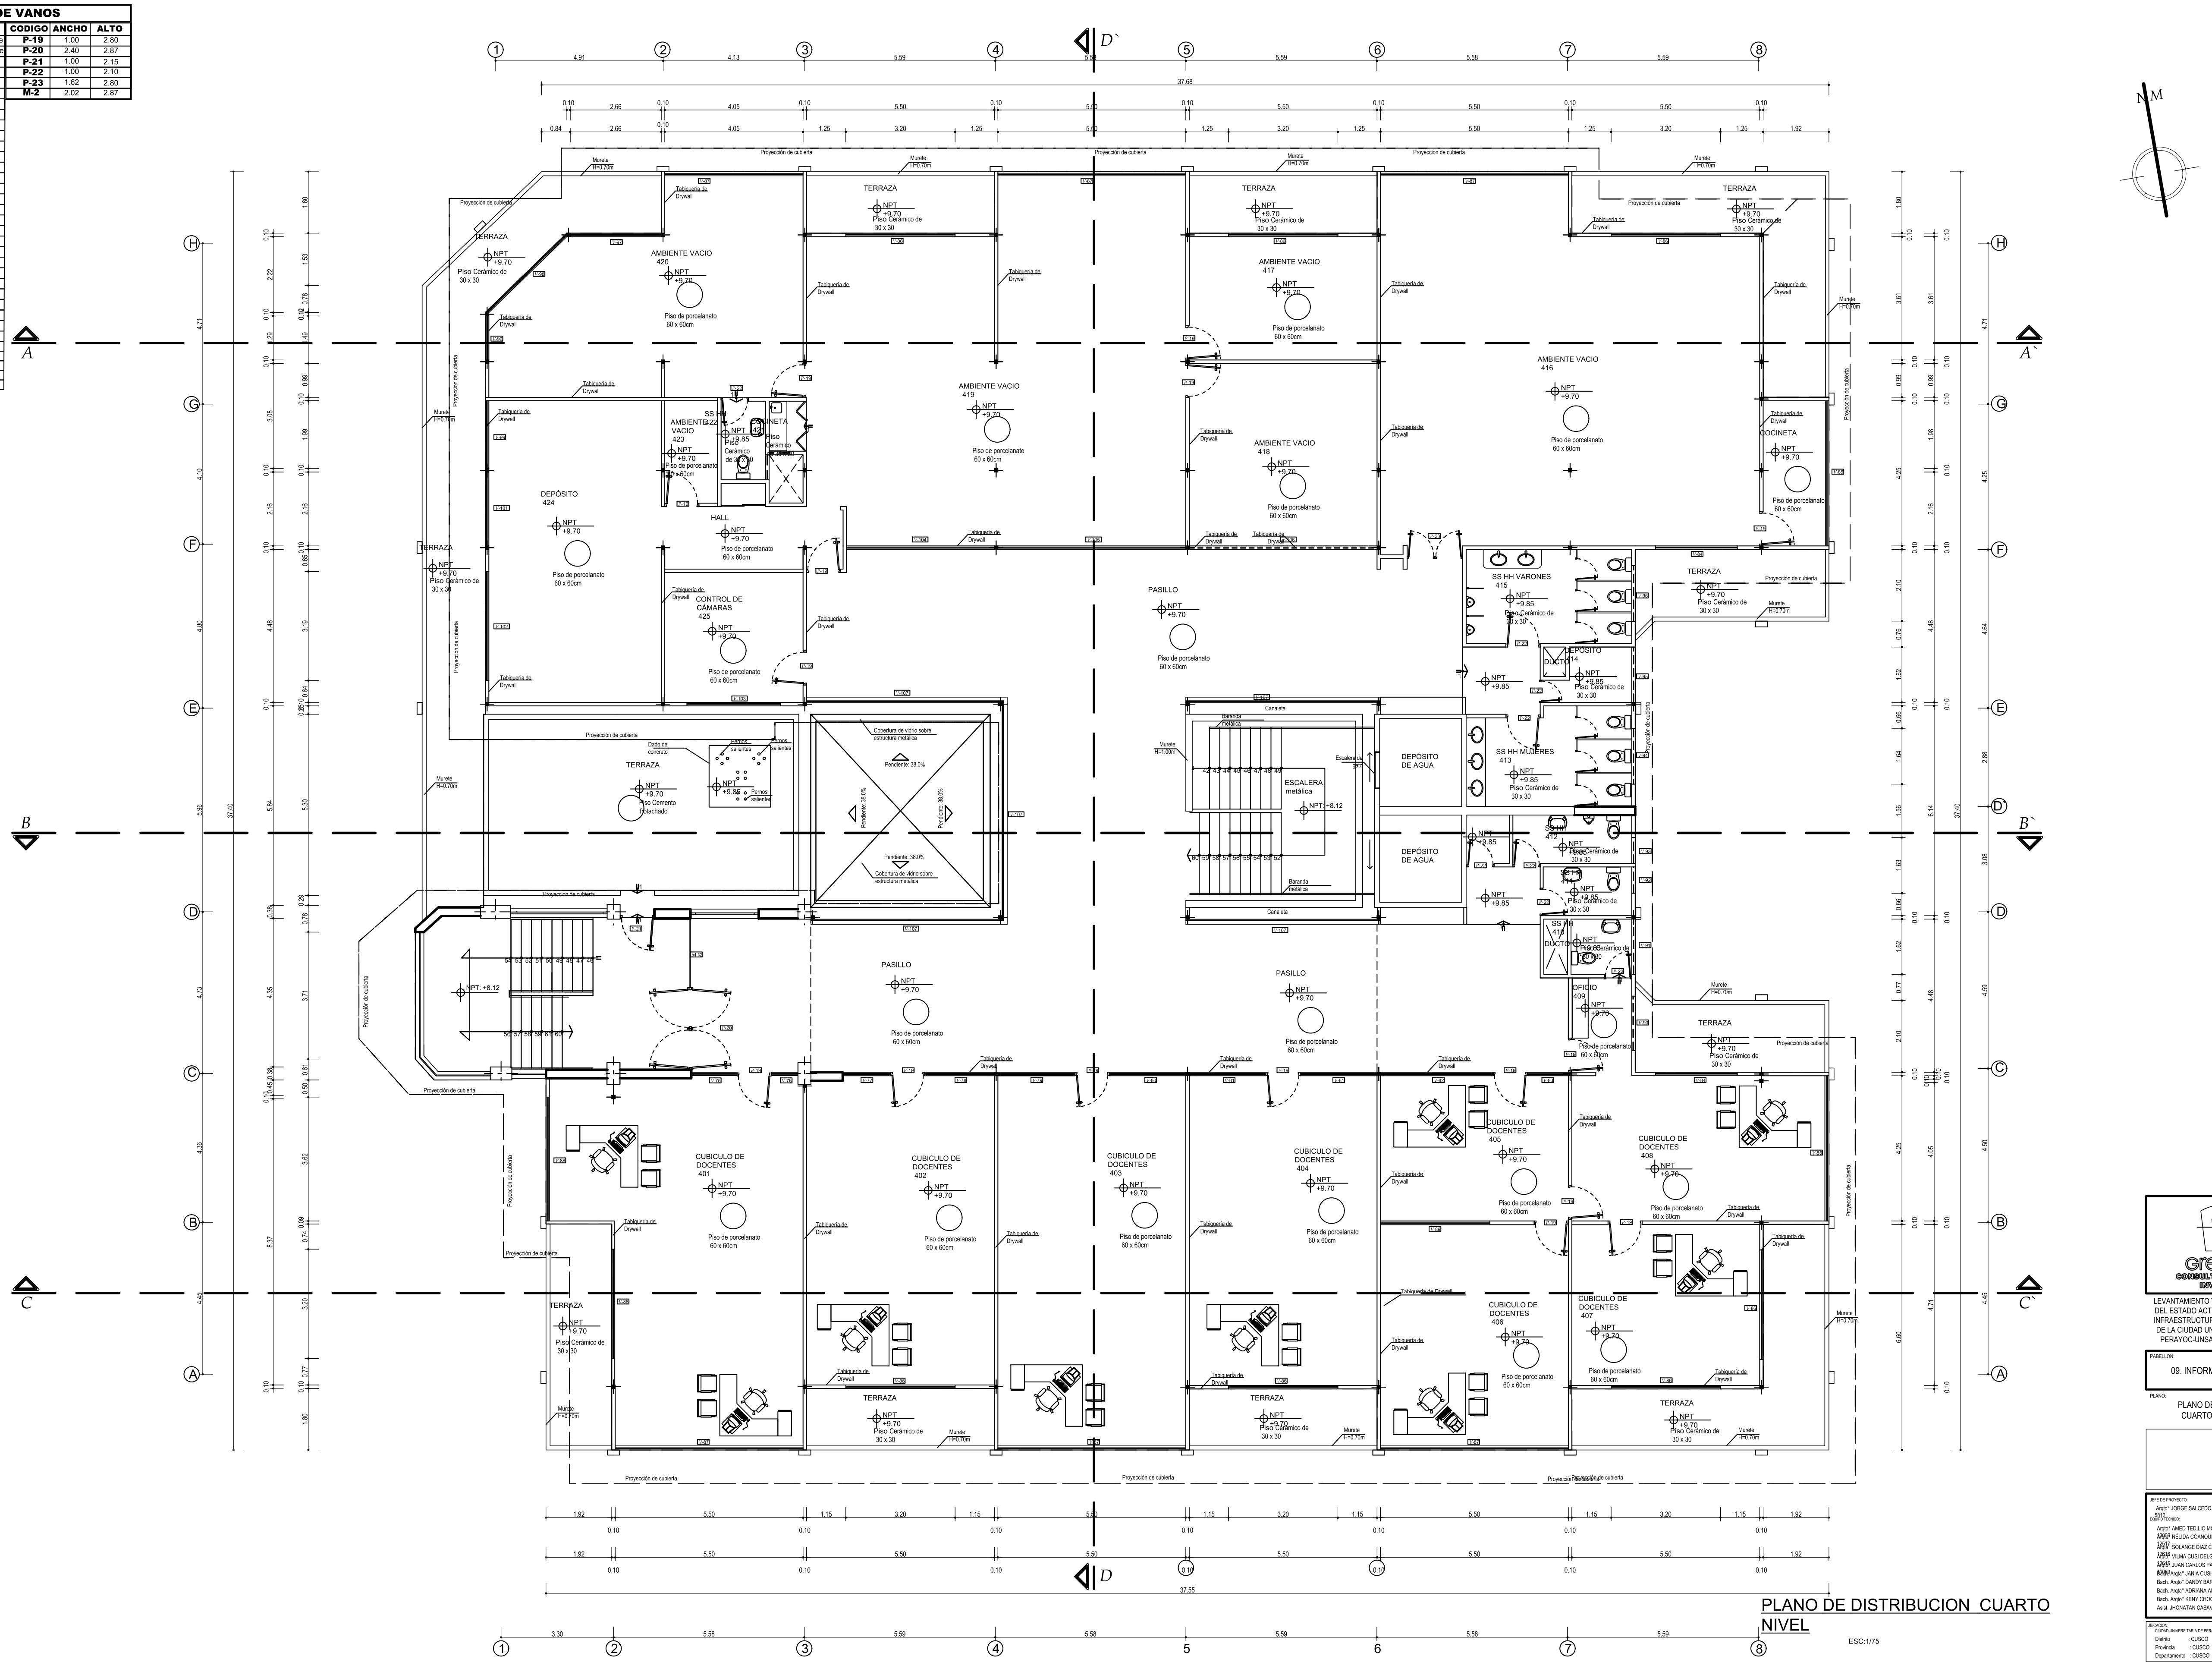

PLANO DE DISTRIBUCION CUARTO NIVEL

ESC:1/75

GREMSA
CONSULTORIA - OBRAS
INVERSIONES

LEVANTAMIENTO TOPOGRÁFICO INTEGRAL
DEL ESTADO ACTUAL A DETALLE DE LA
INFRAESTRUCTURA INTERIOR Y EXTERIOR
DE LA CIUDAD UNIVERSITARIA DE
PERAYOC-UNSAAC

PABELLON:
09. INFORMATICA Y SISTEMAS

PLANO:
PLANO DE DISTRIBUCION
CUARTO NIVEL

JEFE DE PROYECTO:
Arqto° JORGE SALCEDO QUISPE CAP 5812

EQUIPO TÉCNICO:
Arqto° AMED TEDILIO MOSCOSO TOLEDO CAP 13006
Arqta° NÉLIDA COANQUI SINCHI ROCA CAP 12517
Arqta° SOLANGE DIAZ CACERES CAP 12616
Arqta° VILMA CUSI DELGADO CAP 12615
Arqto° JUAN CARLOS PAUCAR VEGA CAP 11059
Bach. Arqta° JANIA CUSIQUISPE QUISPE
Bach. Arqto° DANDY BARRIENTOS RAMOS
Bach. Arqta° ADRIANA AIQUIPA ALOSILLA
Bach. Arqto° KENY CHOQUE INCACUTIPA
Asist. JHONATAN CASAVERDE CCOICCA

UBICACION:
CIUDAD UNIVERSITARIA DE PERAYOC
Distrito : CUSCO
Provincia : CUSCO
Departamento : CUSCO

ESCALA:
INDICADAS

FECHA:
Cusco, Diciembre del 2016

LAMINA:
P-09
AR - 04

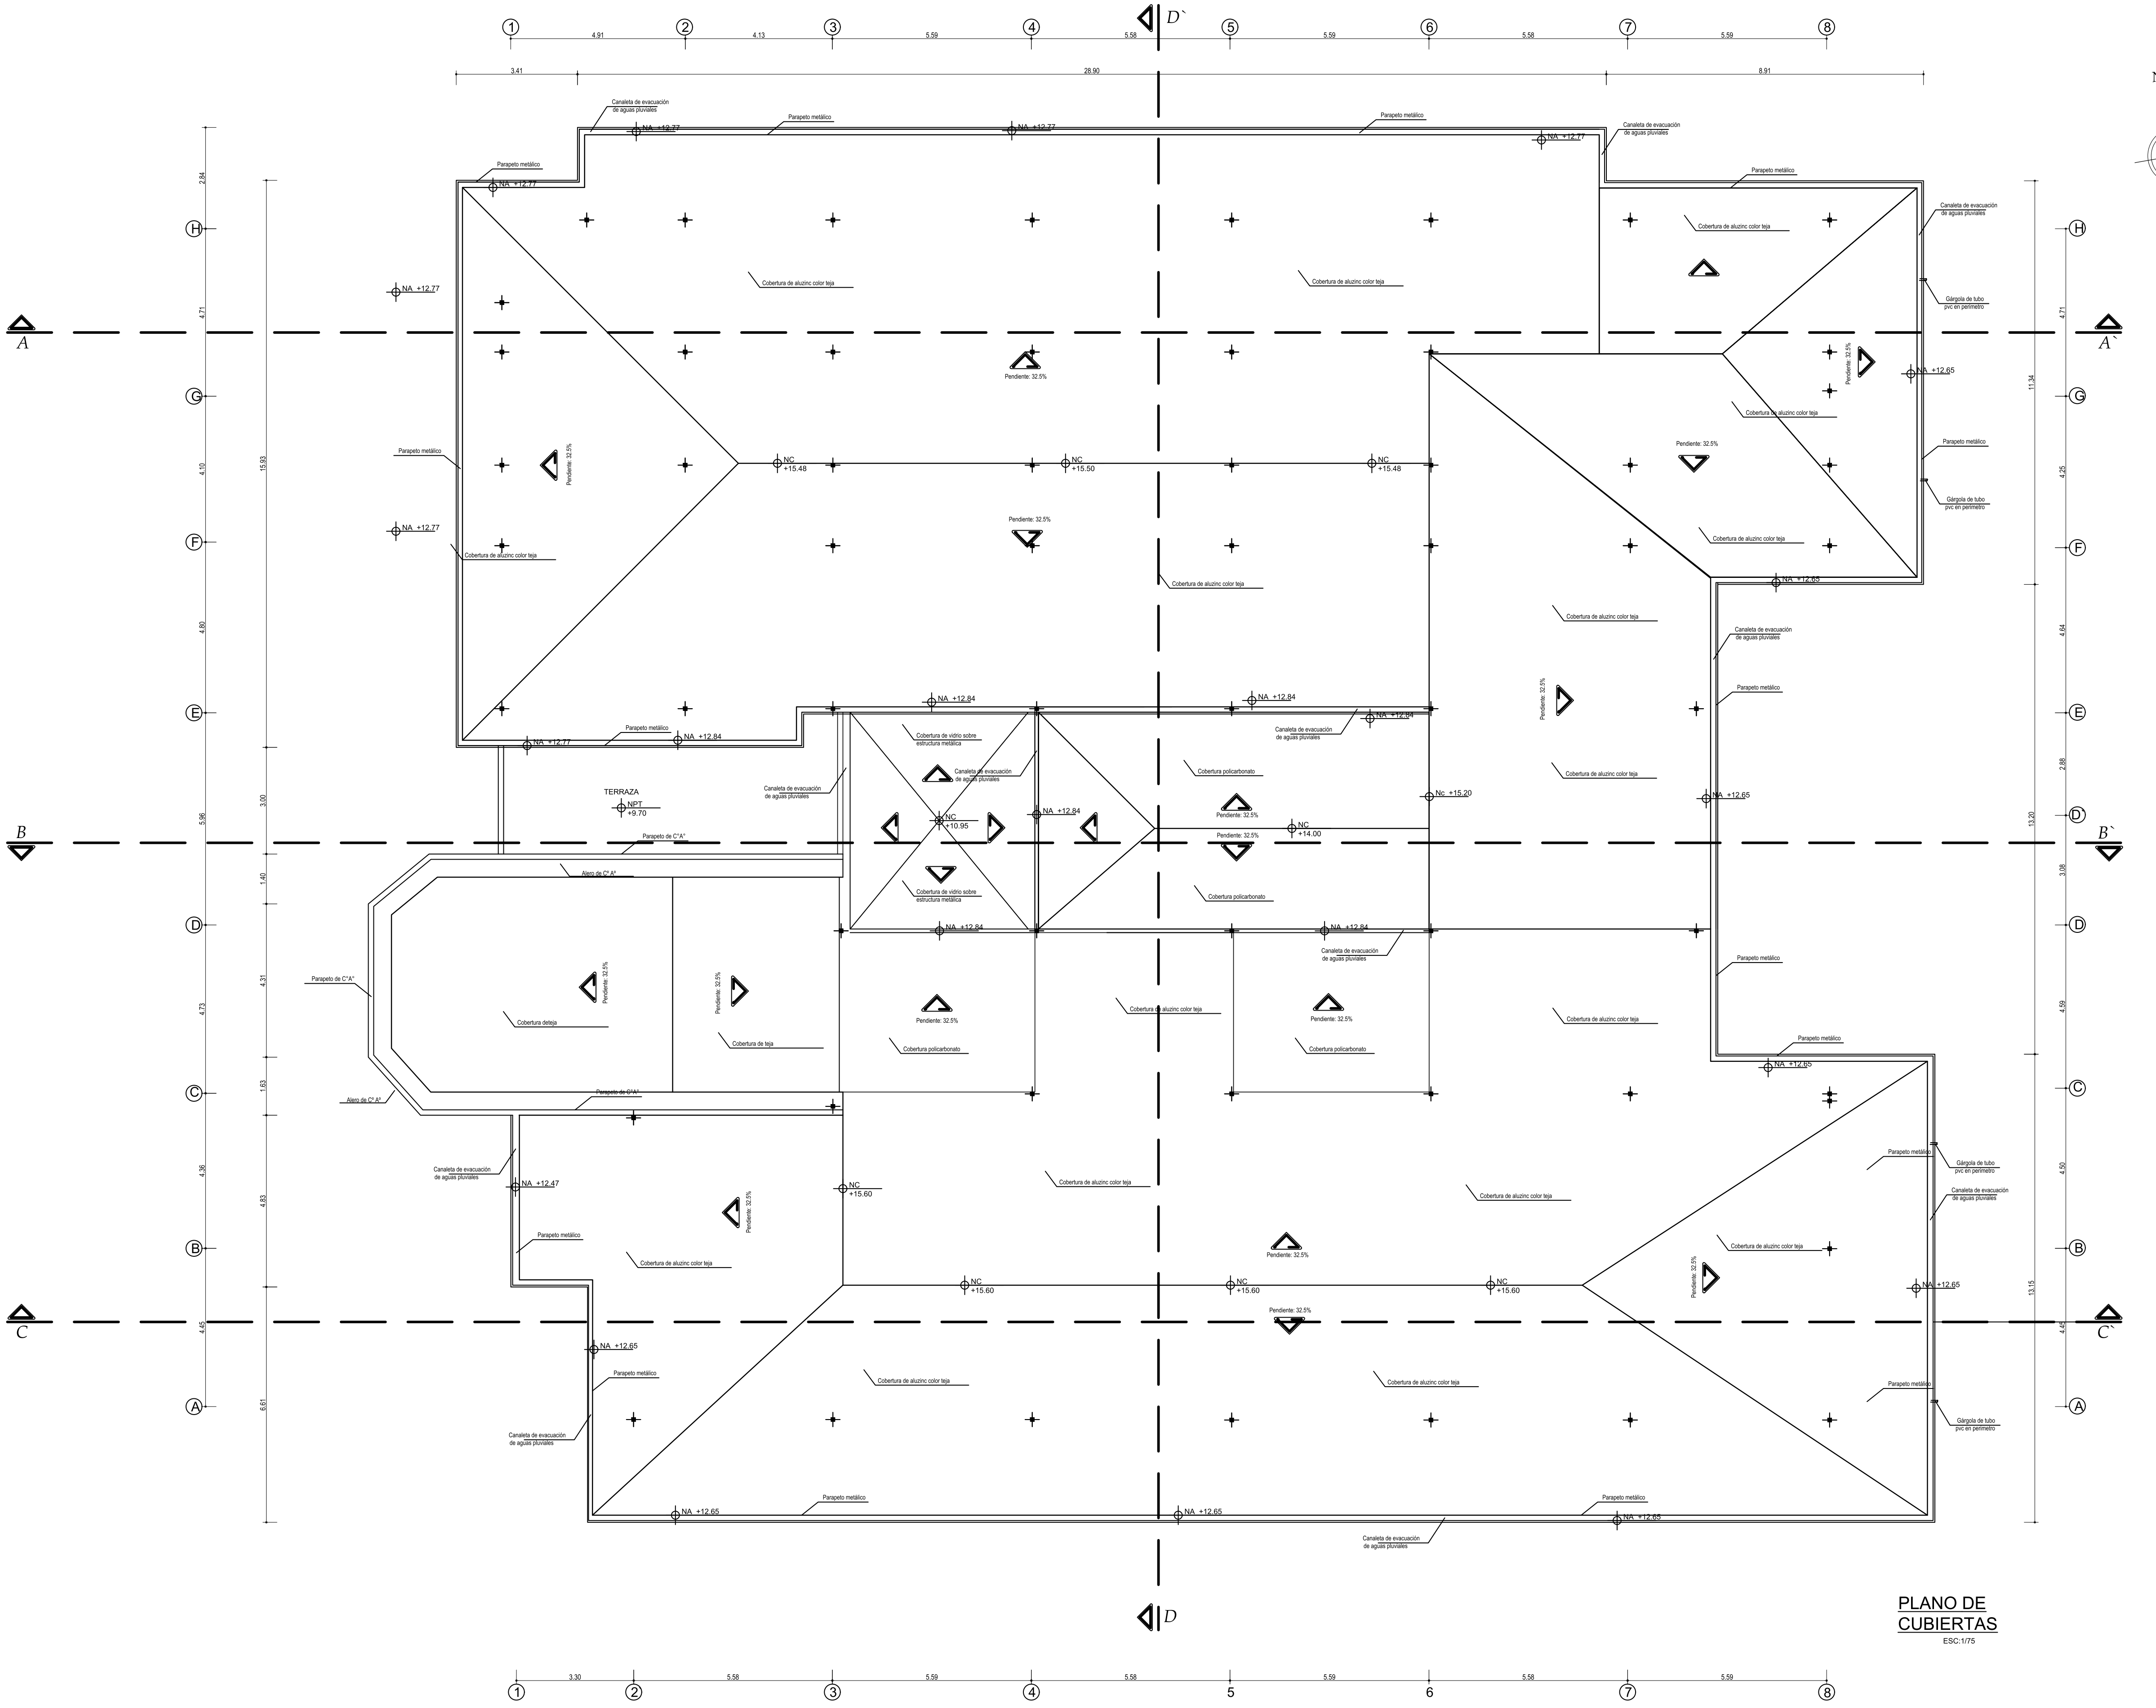

PLANO DE CUBIERTAS

ESC:1/75

GREMSA
CONSULTORIA - OBRAS
INVERSIONES

LEVANTAMIENTO TOPOGRÁFICO INTEGRAL DEL ESTADO ACTUAL A DETALLE DE LA INFRAESTRUCTURA INTERIOR Y EXTERIOR DE LA CIUDAD UNIVERSITARIA DE PERAYOC-UNSAAC

PABELLON:
09. INFORMATICA Y SISTEMAS

PLANO:
PLANO DE CUBIERTAS

JEFE DE PROYECTO:
Arqto° JORGE SALCEDO QUISPE CAP 5812

EQUIPO TÉCNICO:
Arqto° AMED TEDILIO MOSCOSO TOLEDO CAP 13006
Arqta° NÉLIDA COANQUI SINCHI ROCA CAP 12517
Arqta° SOLANGE DIAZ CACERES CAP 12616
Arqta° VILMA CUSI DELGADO CAP 12615
Arqto° JUAN CARLOS PAUCAR VEGA CAP 11059
Bach. Arqta° JANIA CUSIQUISPE QUISPE
Bach. Arqto° DANDY BARRIENTOS RAMOS
Bach. Arqta° ADRIANA AIQUIPA ALOSILLA
Bach. Arqto° KENY CHOQUE INCACUTIPA
Asist. JHONATAN CASAVERDE CCOICCA

UBICACION:
CIUDAD UNIVERSITARIA DE PERAYOC
Distrito : CUSCO
Provincia : CUSCO
Departamento : CUSCO

ESCALA:
INDICADAS

FECHA:
Cusco, Diciembre del 2016

LAMINA:
P-09
AR - 05

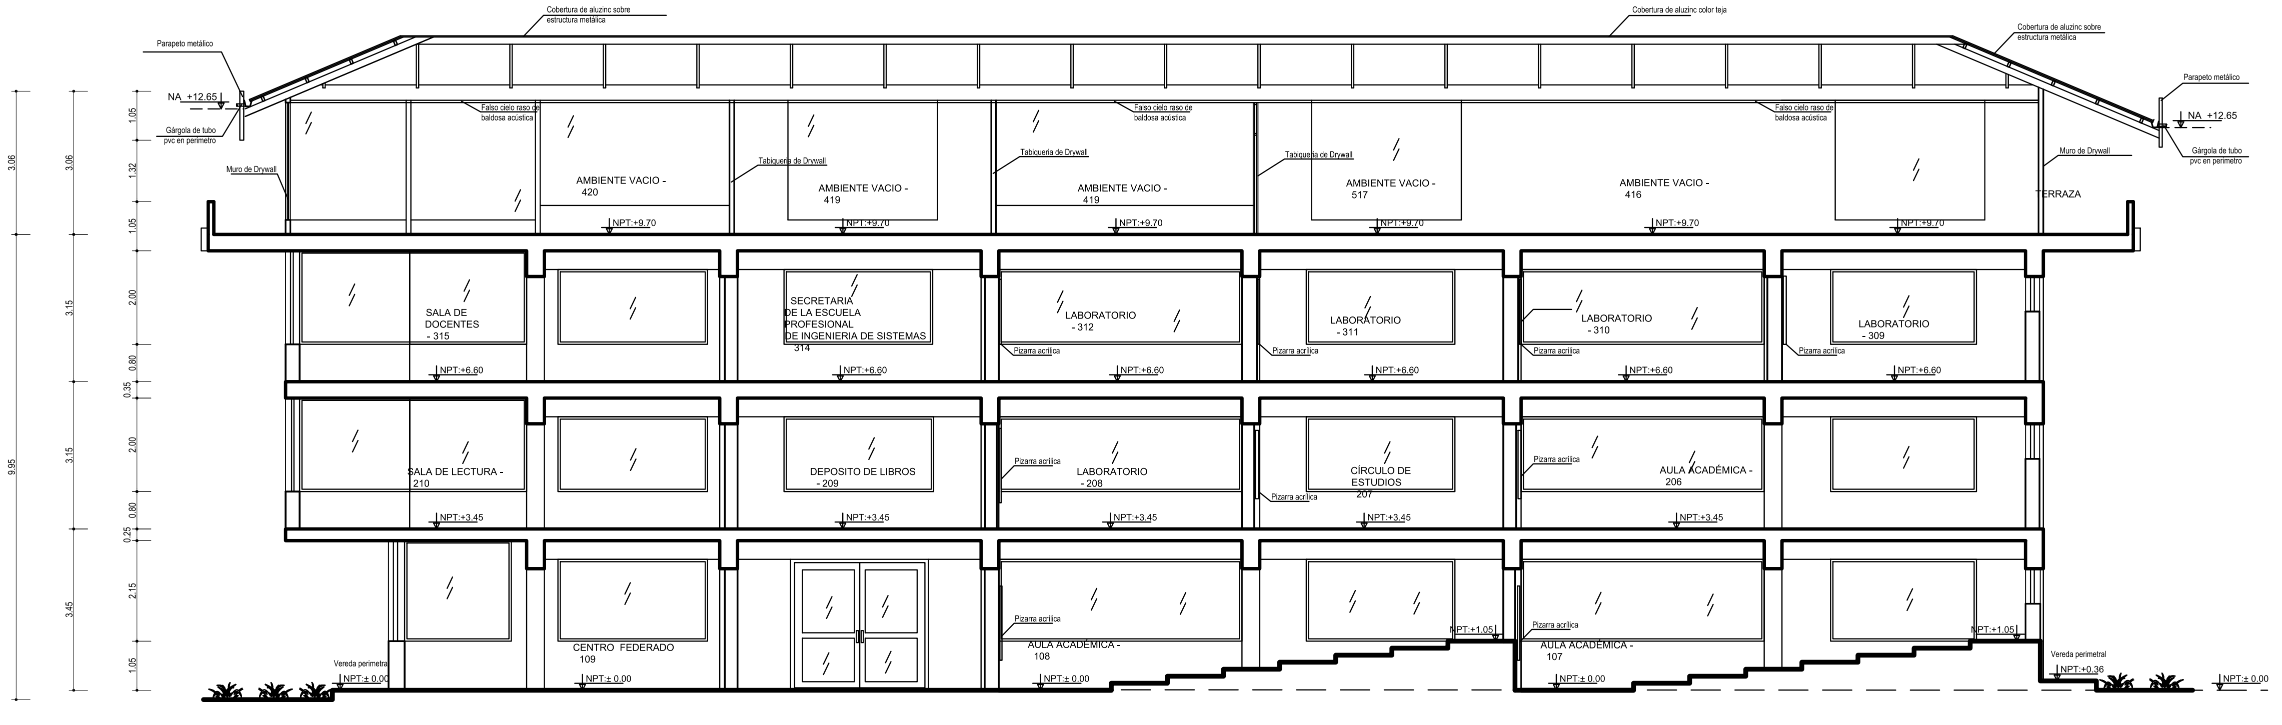

CORTE A - A´

ESC:1/75

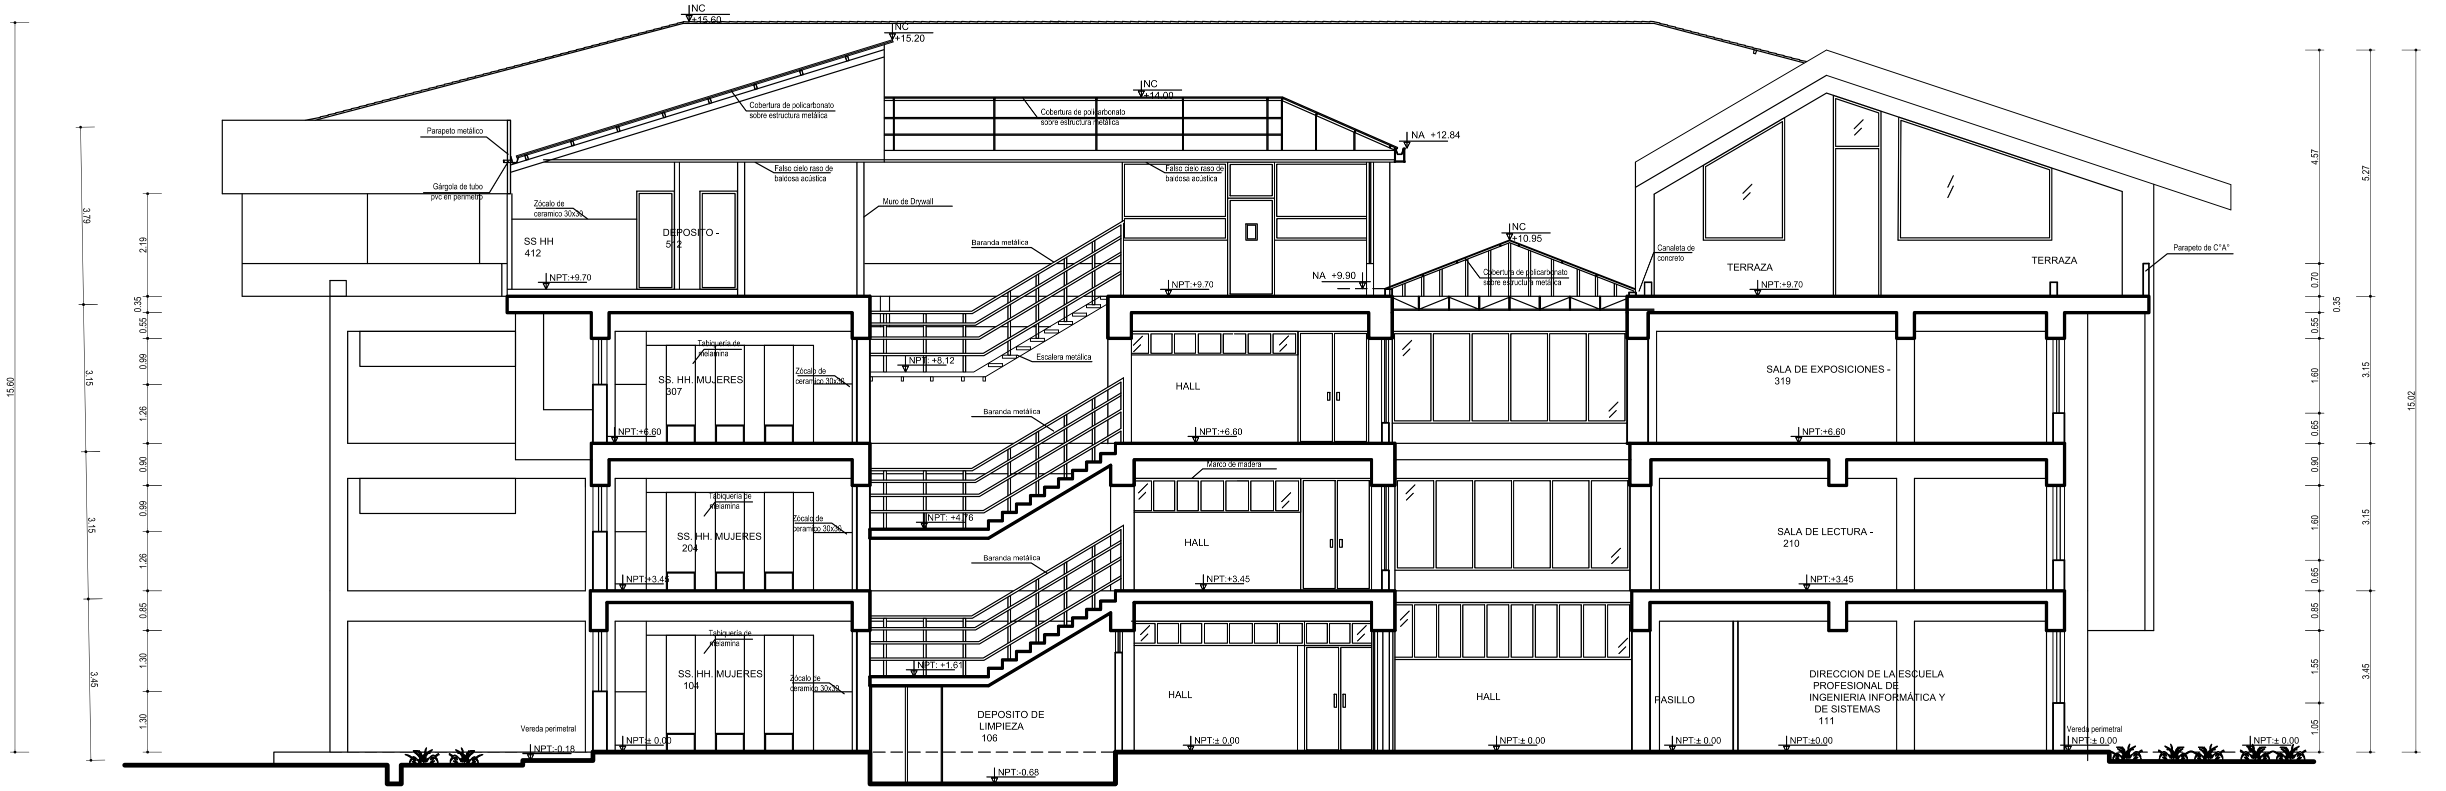

CORTE B - B´

ESC:1/75

gremsa
CONSULTORIA - OBRAS
INVERSIONES

LEVANTAMIENTO TOPOGRÁFICO INTEGRAL
DEL ESTADO ACTUAL A DETALLE DE LA
INFRAESTRUCTURA INTERIOR Y EXTERIOR
DE LA CIUDAD UNIVERSITARIA DE
PERAYOC-UNSAAC

PABELLON:
09. INFORMATICA Y SISTEMAS

PLANO:
CORTES

JEFE DE PROYECTO:
Arqto° JORGE SALCEDO QUISPE CAP 5812

EQUIPO TÉCNICO:
Arqto° AMED TEDILIO MOSCOSO TOLEDO CAP 13006
Arqta° NÉLIDA COANQUI SINCHI ROCA CAP 12517
Arqta° SOLANGE DIAZ CACERES CAP 12616
Arqta° VILMA CUSI DELGADO CAP 12615
Arqto° JUAN CARLOS PAUCAR VEGA CAP 11059
Bach. Arqta° JANIA CUSIQUISPE QUISPE
Bach. Arqto° DANDY BARRIENTOS RAMOS
Bach. Arqta° ADRIANA AIQUIPA ALOSILLA
Bach. Arqto° KENY CHOQUE INCACUTIPA
Asist. JONATAN CASAVERDE CCOICCA

UBICACION:
CIUDAD UNIVERSITARIA DE PERAYOC
Distrito : CUSCO
Provincia : CUSCO
Departamento : CUSCO

ESCALA:
INDICADAS

FECHA:
Cusco, Diciembre del 2016

LAMINA:
P-09
AR - 06

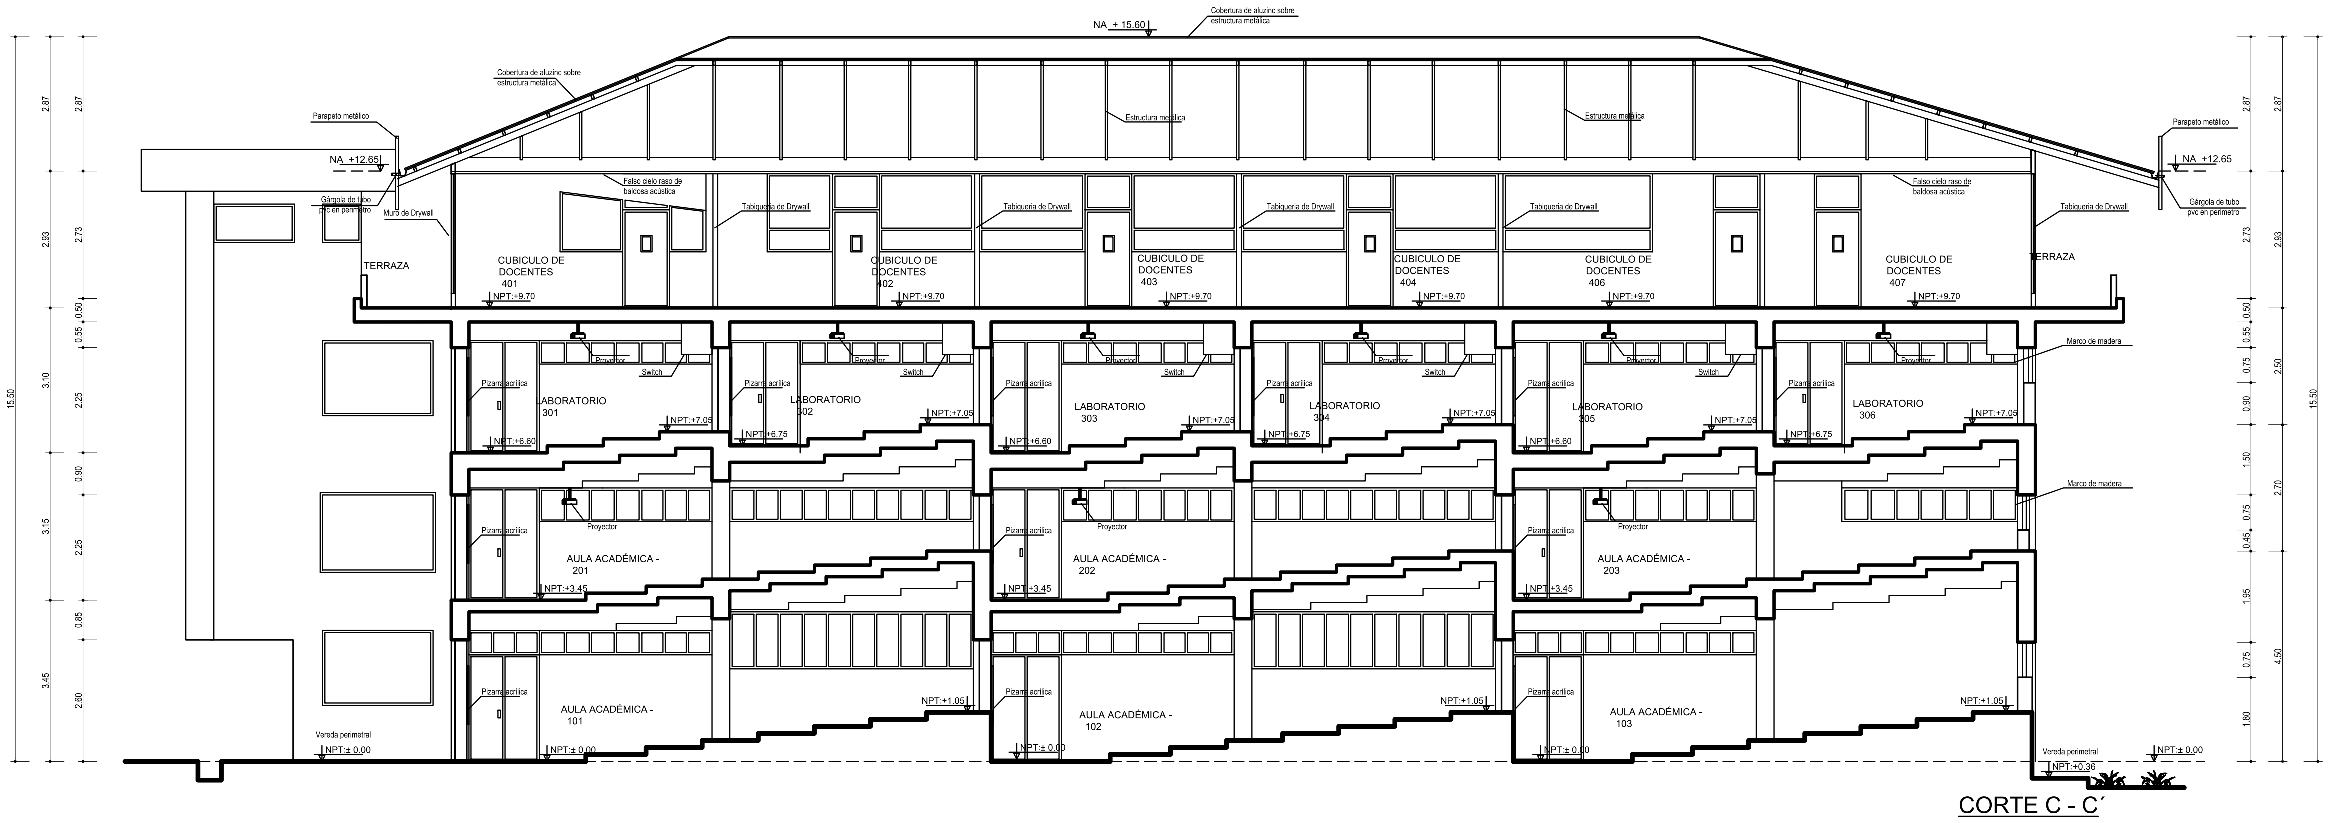

CORTE C - C´
ESC:1/75

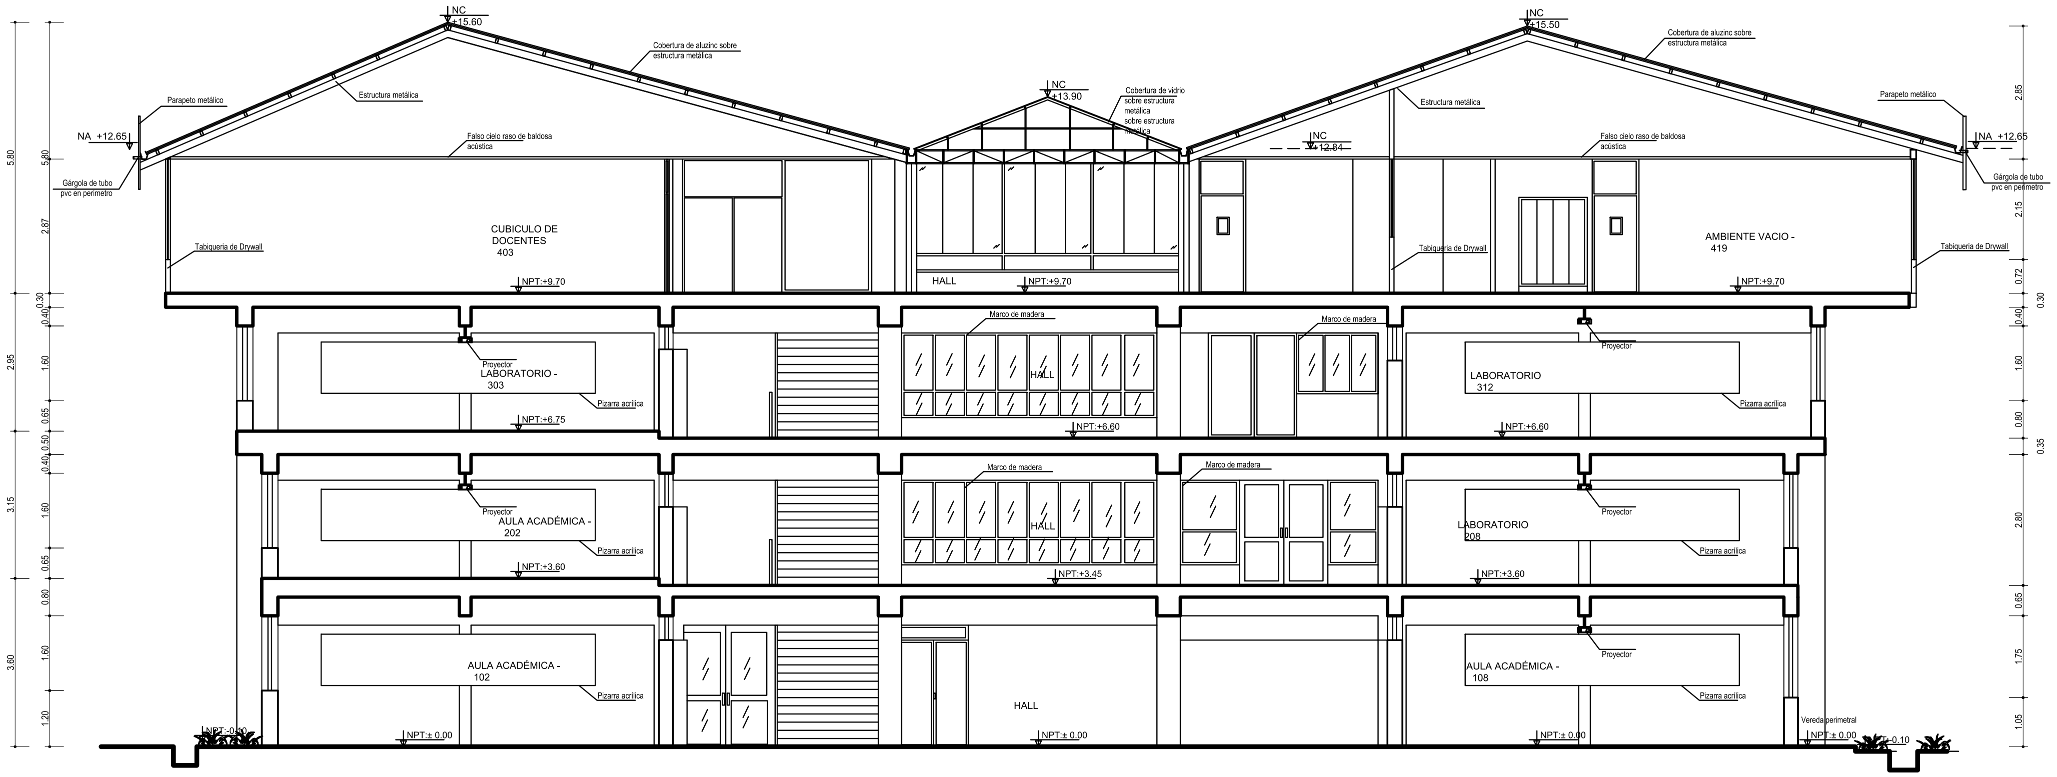

CORTE D - D´
ESC:1/75

GREMSA
CONSULTORIA - OBRAS
INVERSIONES

LEVANTAMIENTO TOPOGRÁFICO INTEGRAL
DEL ESTADO ACTUAL A DETALLE DE LA
INFRAESTRUCTURA INTERIOR Y EXTERIOR
DE LA CIUDAD UNIVERSITARIA DE
PERAYOC-UNSAAC

PABELLON:
09. INFORMATICA Y SISTEMAS

PLANO:
CORTES

JEFE DE PROYECTO:
Arqto° JORGE SALCEDO QUISPE CAP 5812

EQUIPO TÉCNICO:
Arqto° AMED TEDILIO MOSCOSO TOLEDO CAP 13006
Arqta° NÉLIDA COANQUI SINCHI ROCA CAP 12517
Arqta° SOLANGE DIAZ CACERES CAP 12616
Arqta° VILMA CUSI DELGADO CAP 12615
Arqto° JUAN CARLOS PAUCAR VEGA CAP 11059
Bach. Arqta° JANIA CUSIQUISPE QUISPE
Bach. Arqto° DANDY BARRIENTOS RAMOS
Bach. Arqta° ADRIANA AIQUIPA ALOSILLA
Bach. Arqto° KENY CHOQUE INCACUTIPA
Asist. JONATAN CASAVERDE CCOICCA

UBICACION:
CIUDAD UNIVERSITARIA DE PERAYOC
Distrito : CUSCO
Provincia : CUSCO
Departamento : CUSCO

ESCALA:
INDICADAS

FECHA:
Cusco, Diciembre del 2016

LAMINA:
P-09
AR - 07

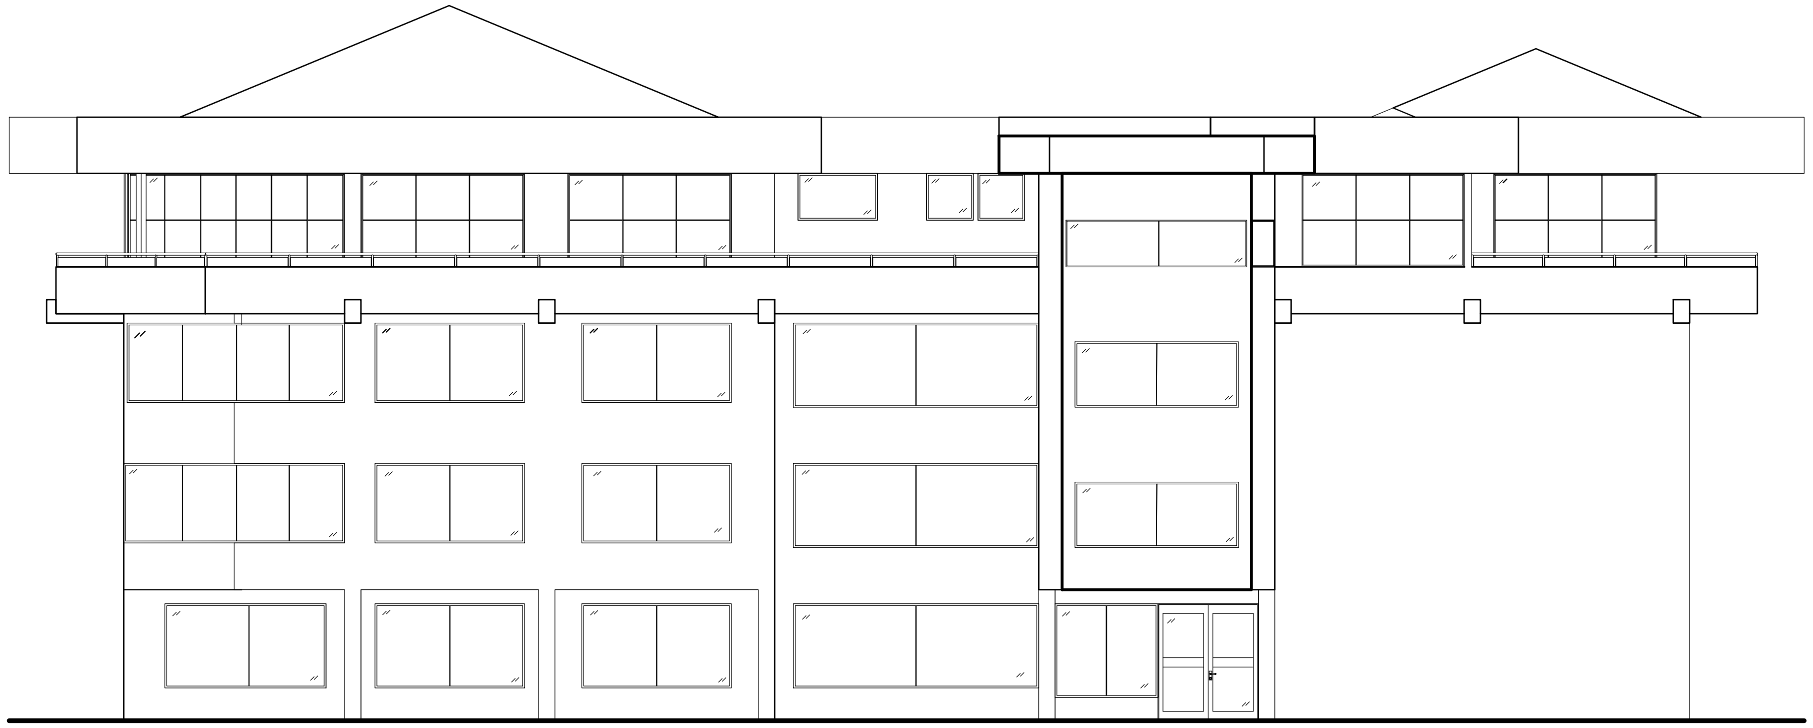

ELEVACIÓN FRONTAL
ESC:1/75

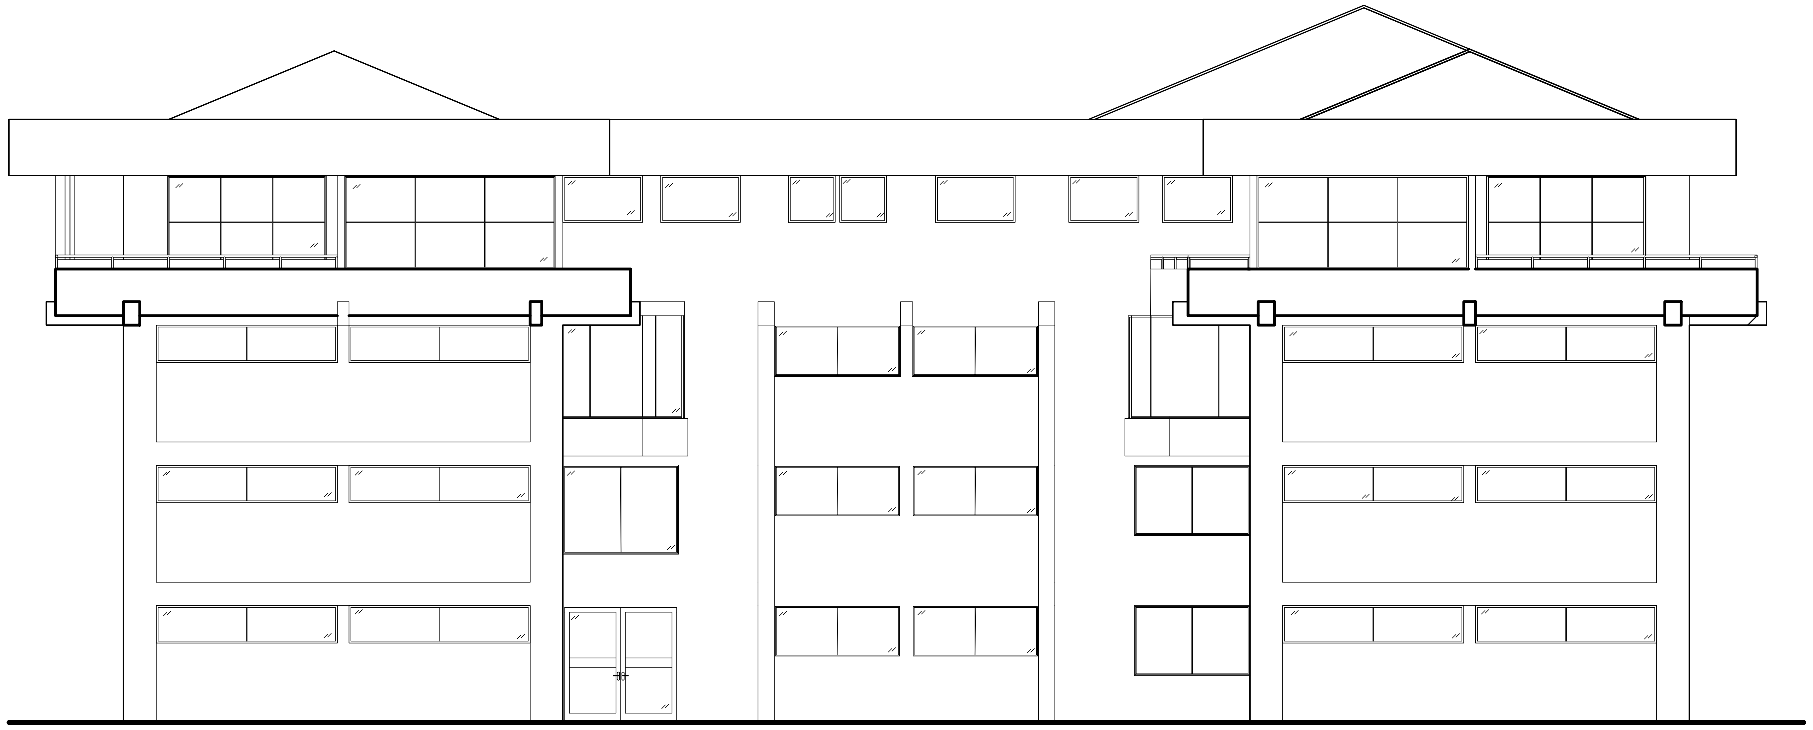

ELEVACIÓN POSTERIOR
ESC:1/75

gremsa
CONSULTORIA - OBRAS
INVERSIONES

LEVANTAMIENTO TOPOGRÁFICO INTEGRAL
DEL ESTADO ACTUAL A DETALLE DE LA
INFRAESTRUCTURA INTERIOR Y EXTERIOR
DE LA CIUDAD UNIVERSITARIA DE
PERAYOC-UNSAAC

PABELLON:
09. INFORMATICA Y SISTEMAS

PLANO:
ELEVACIONES

JEFE DE PROYECTO:
Arqto° JORGE SALCEDO QUISPE CAP 5812

EQUIPO TÉCNICO:
Arqto° AMED TEDILIO MOSCOSO TOLEDO CAP 13006
Arqta° NÉLIDA COANQUI SINCHI ROCA CAP 12517
Arqta° SOLANGE DIAZ CACERES CAP 12616
Arqta° VILMA CUSI DELGADO CAP 12615
Arqto° JUAN CARLOS PAUCAR VEGA CAP 11059
Bach. Arqta° JANIA CUSIQUISPE QUISPE
Bach. Arqto° DANDY BARRIENTOS RAMOS
Bach. Arqta° ADRIANA AIQUIPA ALOSILLA
Bach. Arqto° KENY CHOQUE INCACUTIPA
Asist. JHONATAN CASAVERDE CCOICCA

UBICACION:
CIUDAD UNIVERSITARIA DE PERAYOC
Distrito : CUSCO
Provincia : CUSCO
Departamento : CUSCO

ESCALA:
INDICADAS

FECHA:
Cusco, Diciembre del 2016

LAMINA:
P-09
AR - 08

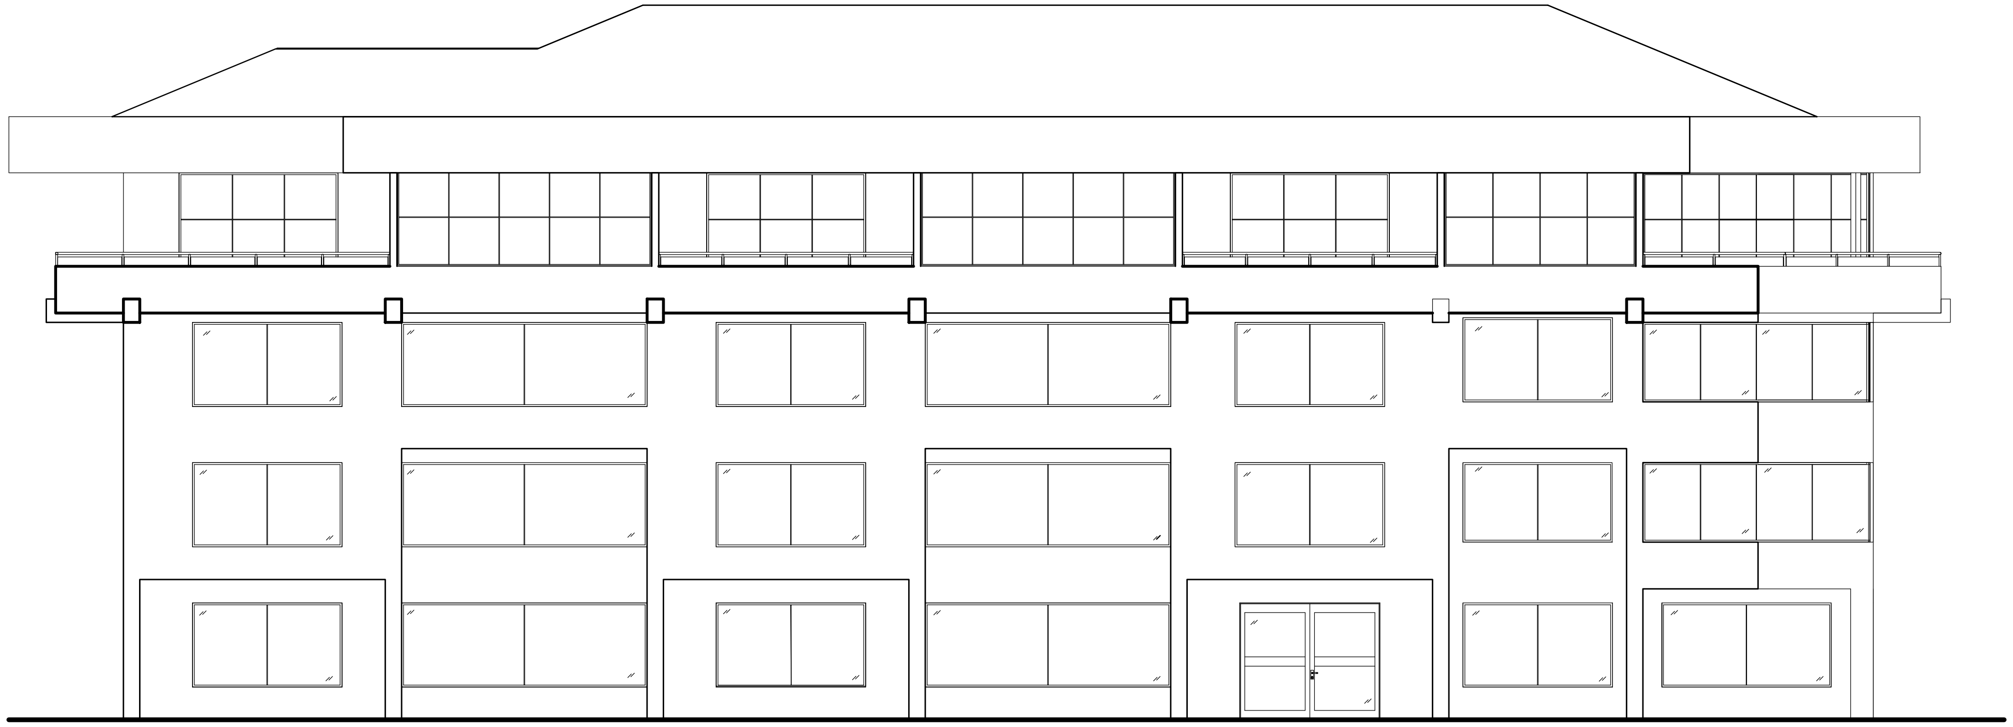

ELEVACIÓN LATERAL IZQUIERDA

ESC:1/75

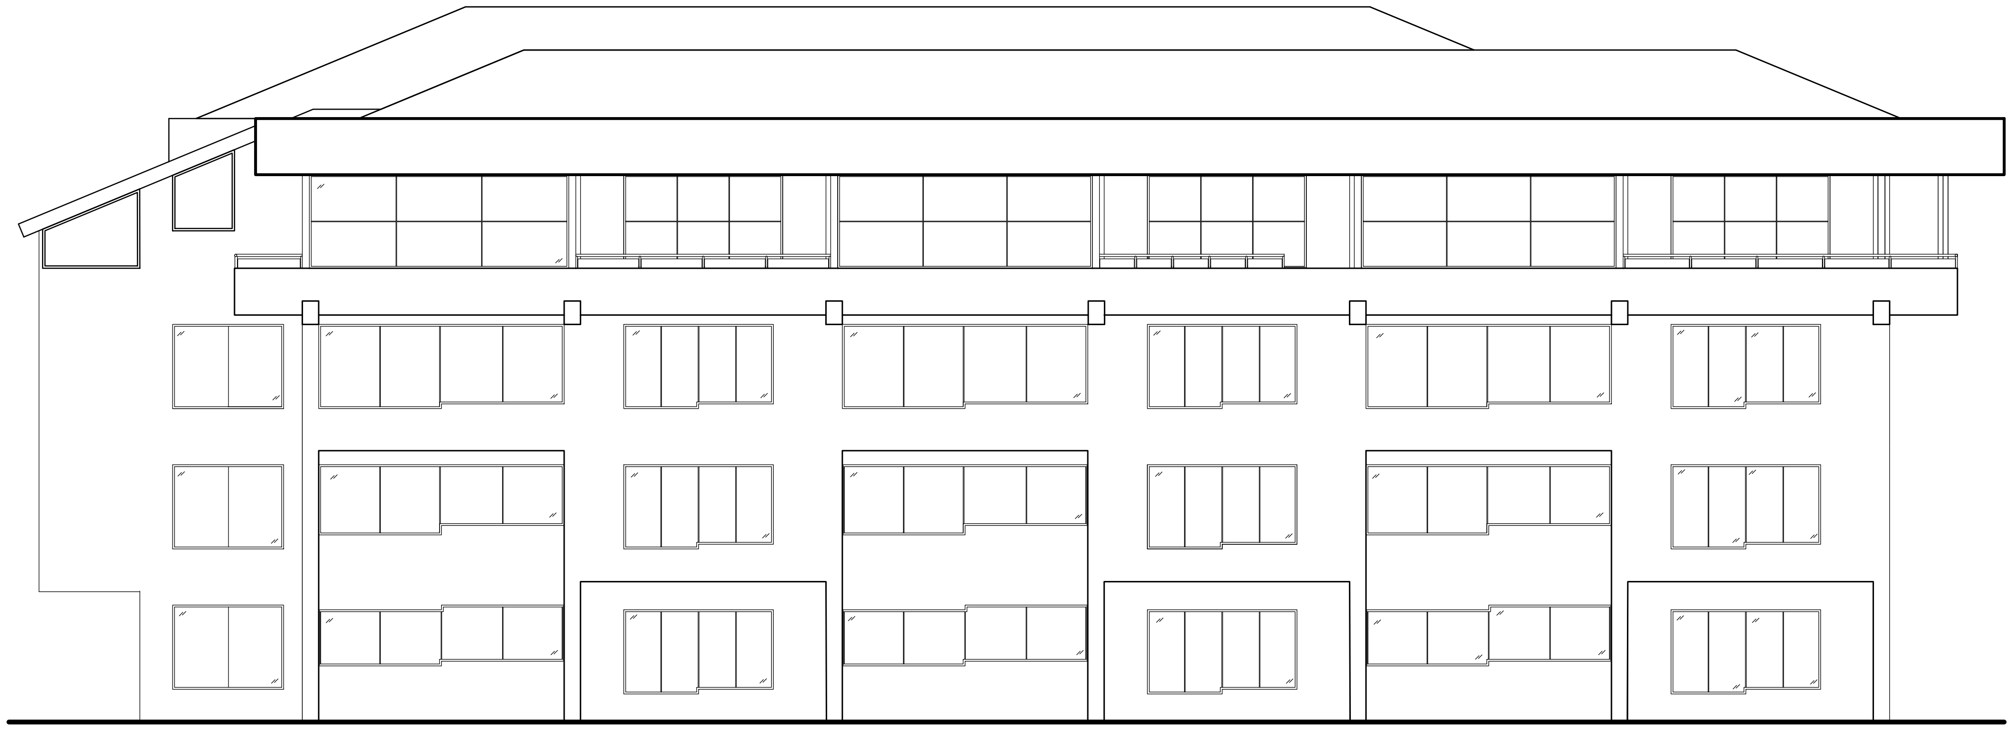

ELEVACIÓN LATERAL DERECHA

ESC:1/75

gremsa
CONSULTORIA - OBRAS
INVERSIONES

LEVANTAMIENTO TOPOGRÁFICO INTEGRAL
DEL ESTADO ACTUAL A DETALLE DE LA
INFRAESTRUCTURA INTERIOR Y EXTERIOR
DE LA CIUDAD UNIVERSITARIA DE
PERAYOC-UNSAAC

PABELLON:
09. INFORMATICA Y SISTEMAS

PLANO:
ELEVACIONES

JEFE DE PROYECTO:
Arqto° JORGE SALCEDO QUISPE CAP 5812

EQUIPO TÉCNICO:
Arqto° AMED TEDILIO MOSCOSO TOLEDO CAP 13006
Arqta° NÉLIDA COANQUI SINCHI ROCA CAP 12517
Arqta° SOLANGE DIAZ CACERES CAP 12616
Arqta° VILMA CUSI DELGADO CAP 12615
Arqto° JUAN CARLOS PAUCAR VEGA CAP 11059
Bach. Arqta° JANIA CUSIQUISPE QUISPE
Bach. Arqto° DANDY BARRIENTOS RAMOS
Bach. Arqta° ADRIANA AIQUIPA ALOSILLA
Bach. Arqto° KENY CHOQUE INCACUTIPA
Asist. JHONATAN CASAVERDE CCOICCA

UBICACION:
CIUDAD UNIVERSITARIA DE PERAYOC
Distrito : CUSCO
Provincia : CUSCO
Departamento : CUSCO

ESCALA:
INDICADAS

FECHA:
Cusco, Diciembre del 2016

LAMINA:
P-09
AR - 09