Universidad Nacional de San Antonio Abad del Cusco

Facultad de Ingeniería Eléctrica, Electrónica, Informática y Mecánica

---

Escuela Profesional de Ingeniería Informática y de Sistemas

EXPEDIENTE TÉCNICO DE OBRA

Planos de estructura

Primer entregable del curso de:

Redes de computadoras I

Docente:
Rony Villafuerte Serna

Integrantes:

- José Francisco Quentasi Juachin	215948
- Luis Alejandro Ramos Aguirre	225425
- Hernan Washington Ramos Alata	221989
- Efrian Vitorino Marin	160337

12 de octubre de 2026

1. Normas y estándares aplicados

El diseño, suministro, instalación y certificación de todo el sistema de telecomunicaciones se regirá estrictamente por las normas y estándares internacionales de la industria de cableado estructurado, así como por las especificaciones técnicas detalladas en el presente expediente.

1. **Estándares de Cableado Estructurado:**
   El proyecto debe cumplir con los estándares **ANSI/TIA/EIA** aplicables para cableado de telecomunicaciones.
   El cableado estructurado será instalado y certificado según la **Categoría 6A** para el canal completo.
   Las etiquetas de cables, patch cords y paneles deben seguir el estándar **ANSI/TIA/EIA 606B**.
   El sistema de cableado debe ser diseñado bajo la premisa de los **seis componentes clave** de la infraestructura de telecomunicaciones: Instalaciones de entrada, Sala de equipos, Canalizaciones de montantes (Back-bone), Salas de telecomunicaciones, Canalizaciones horizontales y Áreas de trabajo.
2. **Estándares de Fibra Óptica:**
   Las especificaciones y parámetros de transmisión para el cableado de fibra óptica están basados en las normas **TIA-568 y TIA-569**.
   Se recomienda el uso de fibra óptica multimodo de **50 µm** para cableado vertical debido a su eficiencia en distancias largas.
3. **Normas de Calidad y Unidades:**
   En todos los documentos del presente suministro se utilizará el **Sistema Métrico Internacional de Medidas**.
   Los materiales utilizados en la instalación, incluidos los equipos, deben ser **nuevos, de la mejor calidad** dentro de su clase y libres de defectos.
   El equipo en general debe funcionar sin vibraciones indebidas y con el mínimo ruido permitido por las normas.
   El revestimiento de los cables (UTP, Patch Cord y Line Cord) debe ser **LSZH (Low Smoke Zero Halogen)**.
4. **Certificación y Pruebas:**
   Se someterá a los materiales y equipos a todas las **pruebas, controles, inspecciones o verificaciones** prescritas para comprobar su cumplimiento.
   La certificación del cableado estructurado se realizará **in situ por un Certificador independiente**.
   Se utilizarán **probadores de campo calibrados** para la certificación de puntos de red y se deberá generar el reporte con los parámetros técnicos.

A-0

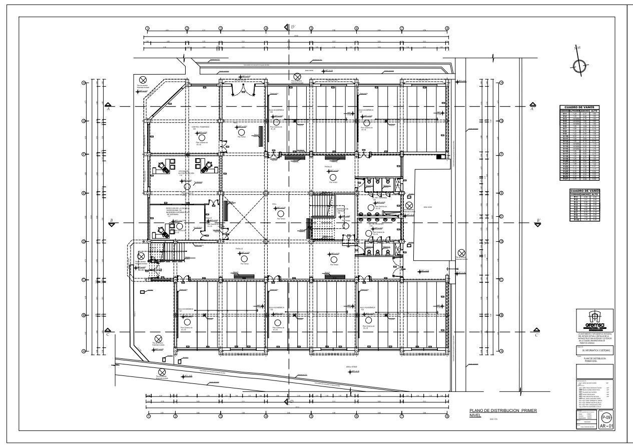

A-0

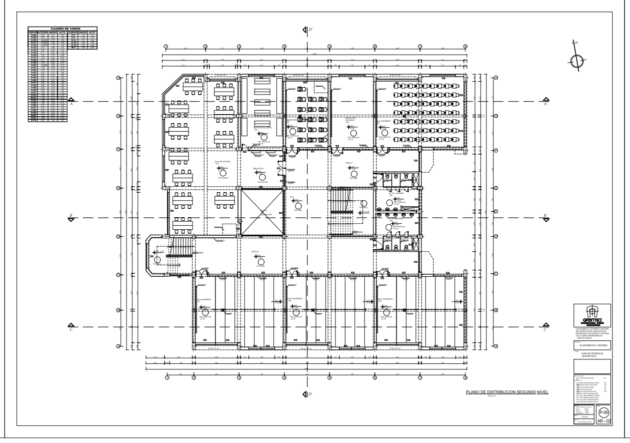

A-0

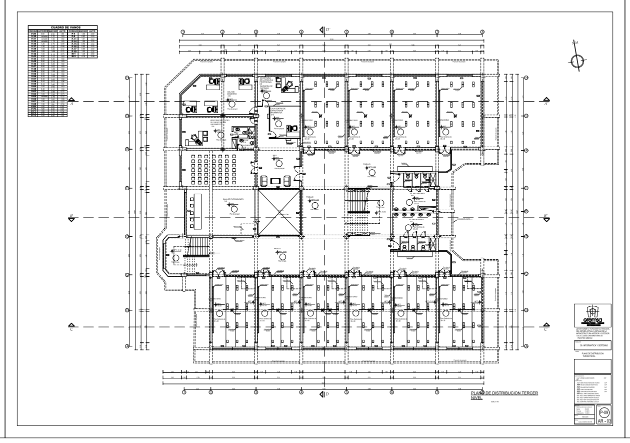

A-0

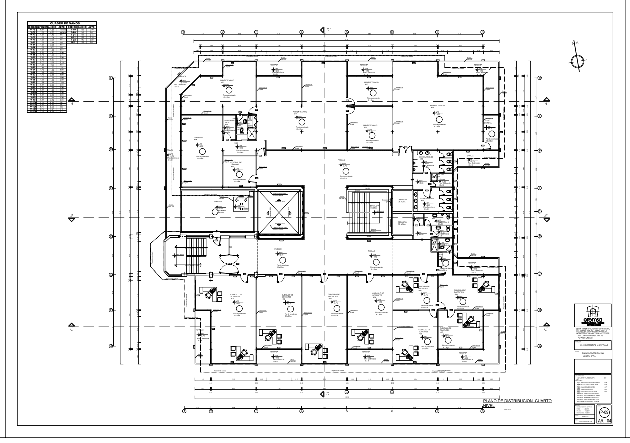

A-0

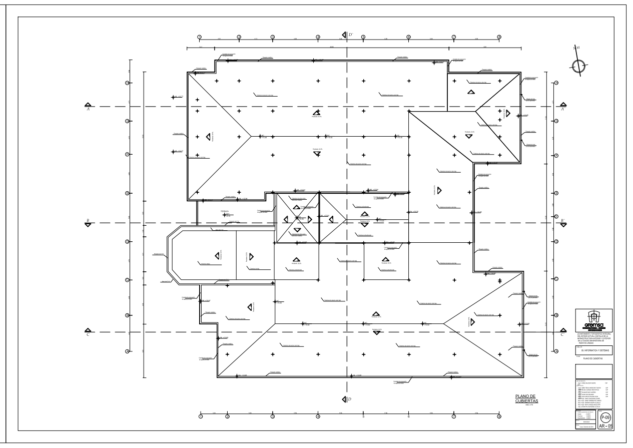

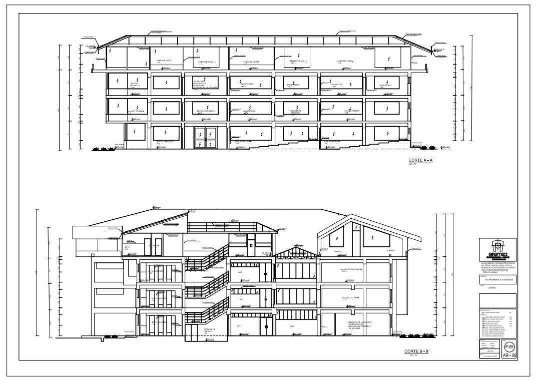

A-1

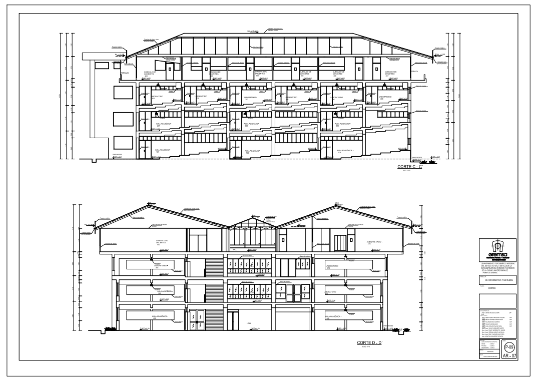

A-1

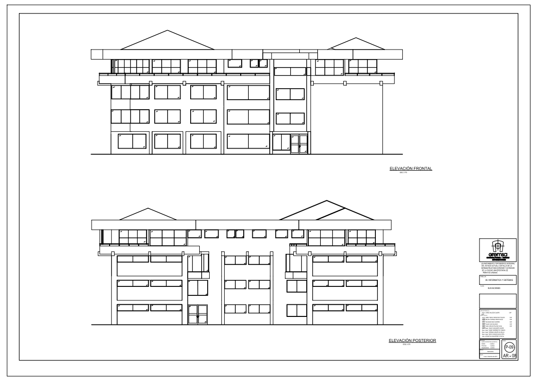

A-1

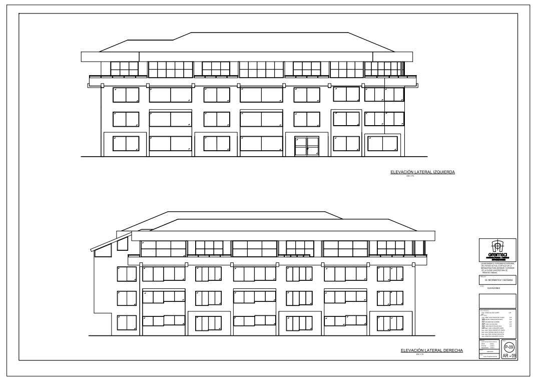

A-1

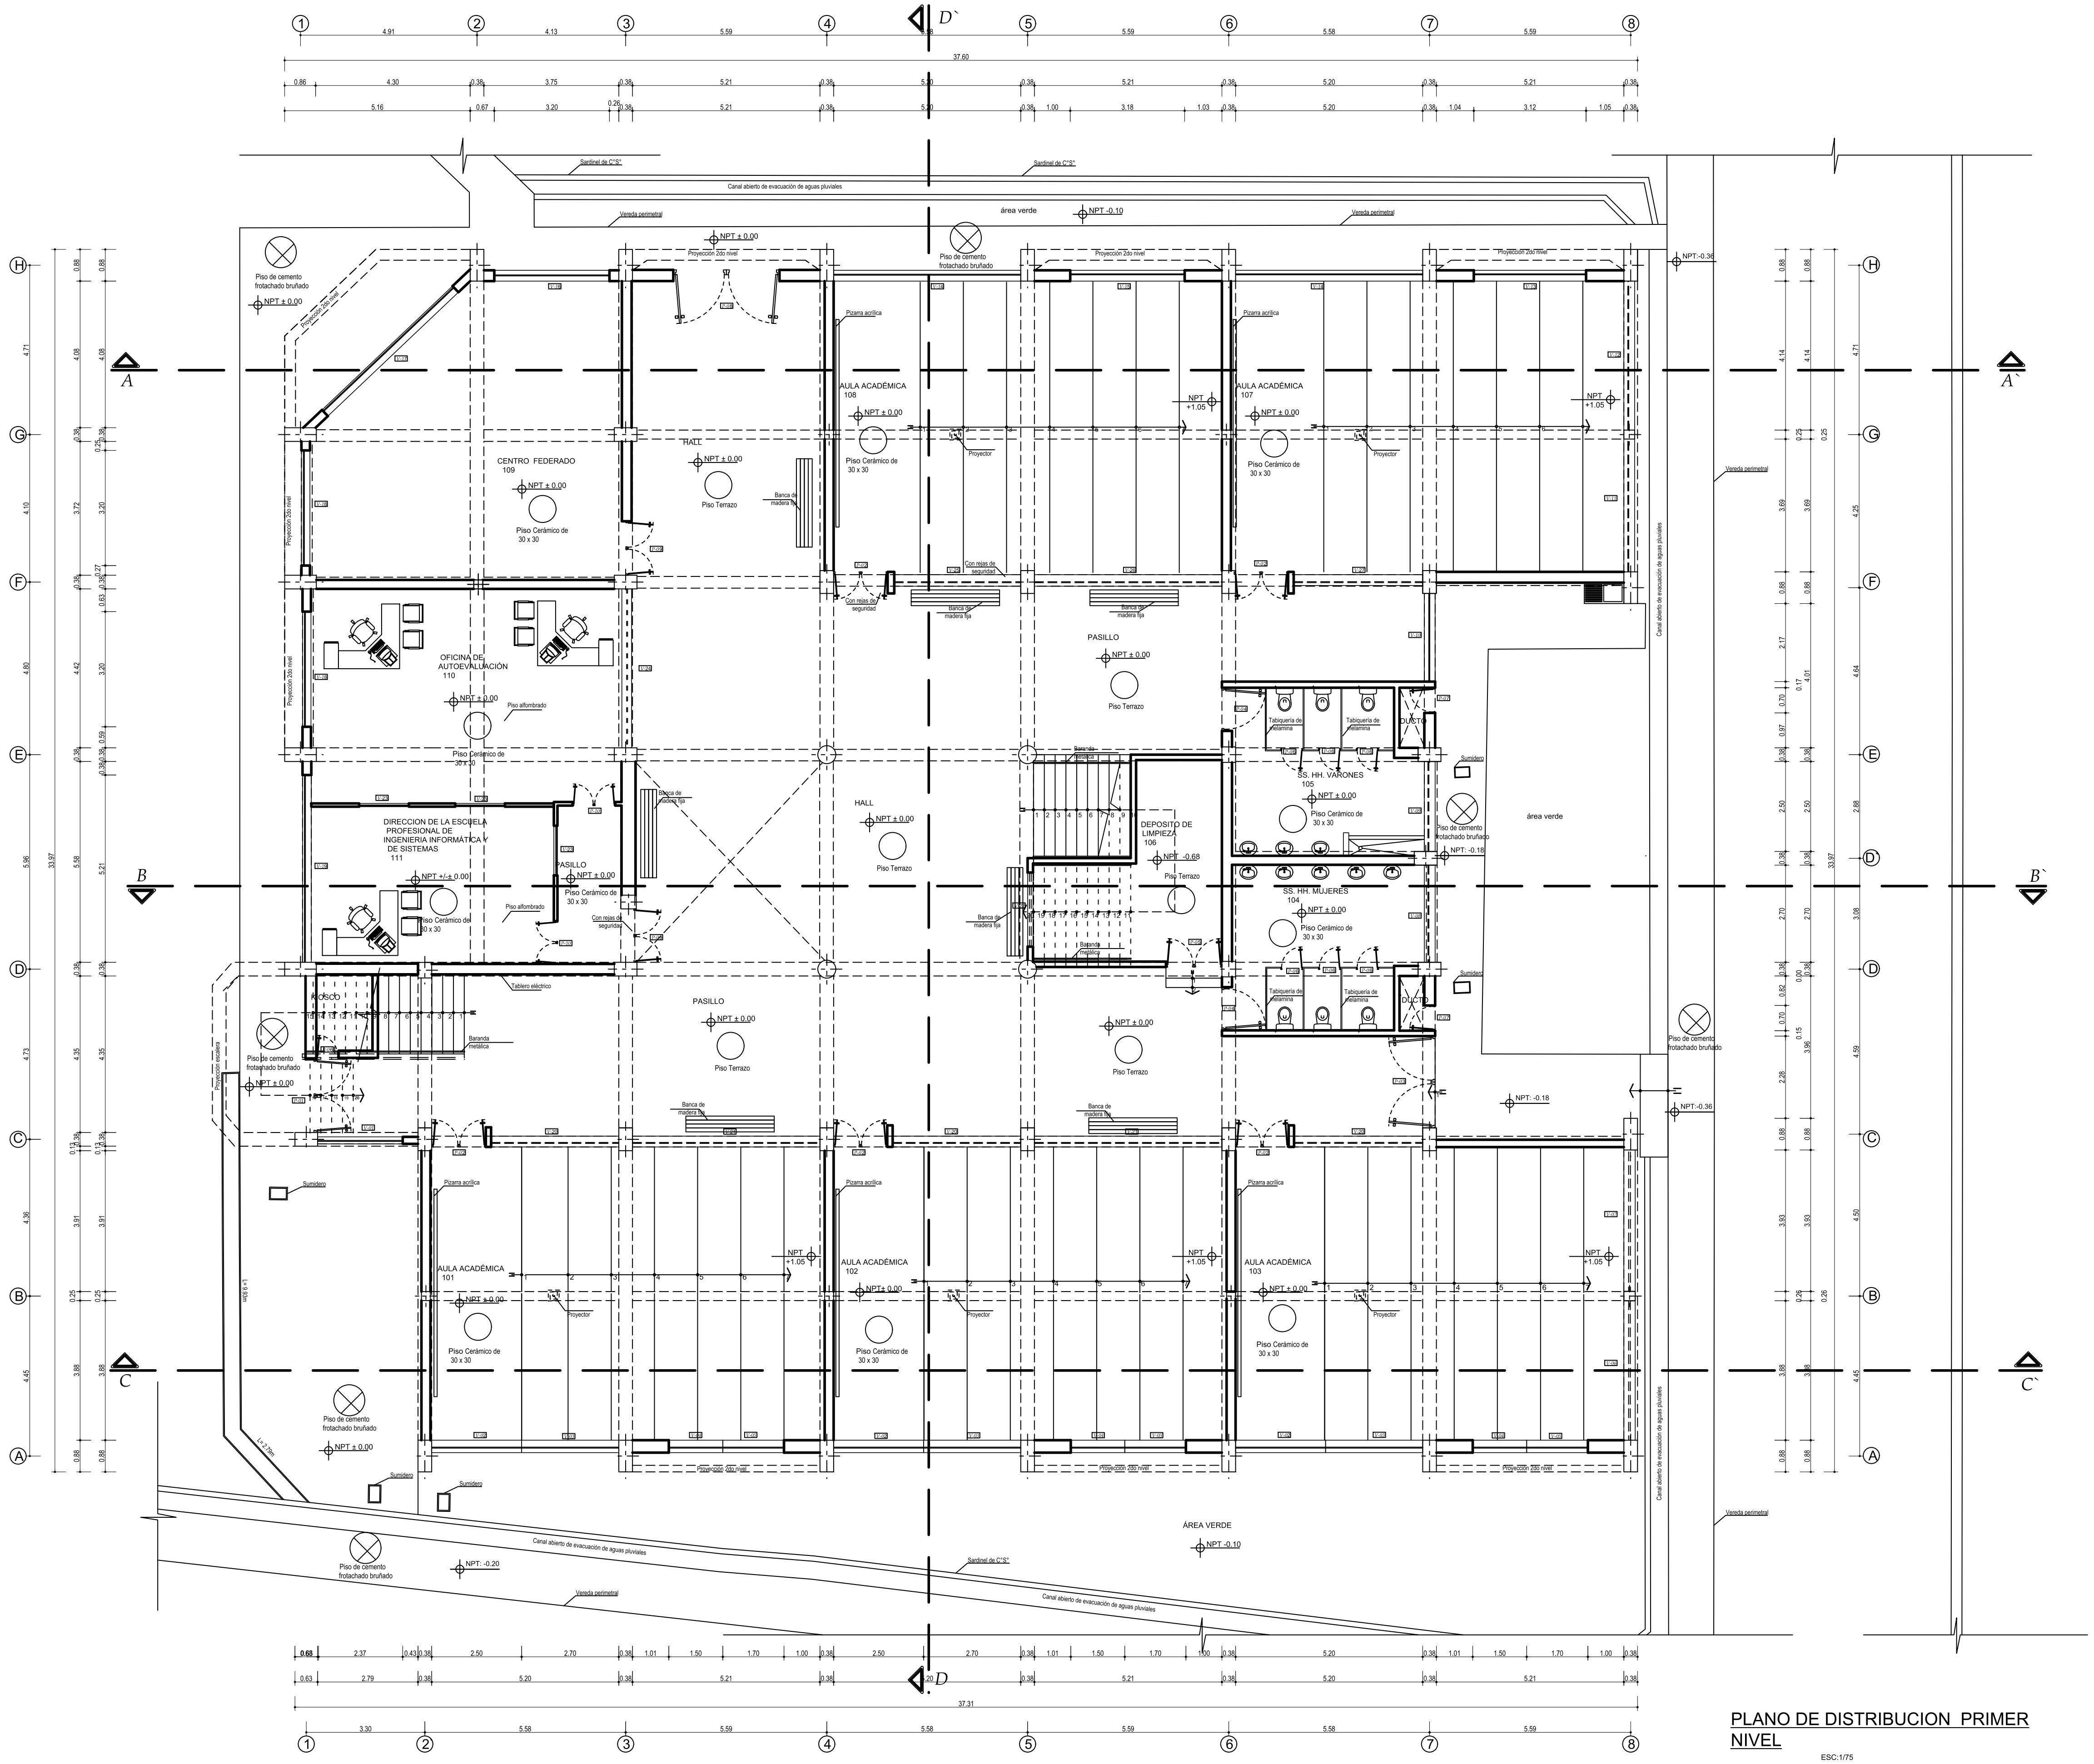
AULA ACADÉMICA 108
AULA ACADÉMICA 107
CENTRO FEDERADO 109
HALL
OFICINA DE AUTOEVALUACIÓN 110
DIRECCION DE LA ESCUELA PROFESIONAL DE INGENIERIA INFORMATICA Y DE SISTEMAS 111
PASILLO
HALL
DEPOSITO DE LIMPIEZA 106
SS. HH. VARONES 105
SS. HH. MUJERES 104
KIOSCO
AULA ACADÉMICA 101
AULA ACADÉMICA 102
AULA ACADÉMICA 103
área verde
ÁREA VERDE
Piso de cemento frotachado bruñado
Piso Cerámico de 30 x 30
Piso Terrazo
Piso alfombrado
NPT ± 0.00
NPT -0.10
NPT -0.36
NPT -0.18
NPT -0.20
NPT +1.05
Canal abierto de evacuación de aguas pluviales
Sardinel de C°S°
Vereda perimetral
Proyección 2do nivel
Pizarra acrílica
Proyector
Banca de madera fija
Sumidero
Tablero eléctrico
Baranda metálica
37.60
37.31
A
A`
B
B`
C
C`
D
D`

PLANO DE DISTRIBUCION PRIMER NIVEL

ESC:1/75

CUADRO DE VANOS			
CODIGO	**ALFEIZER**	**ANCHO**	**ALTO**
V-1	1.20	2.37	1.60
V-2	1.20	2.50	1.60
V-3	variable	2.70	1.60
V-4	variable	1.50	1.60
V-5	variable	1.70	1.60
V-6	1.80	3.88	0.75
V-7	1.80	3.93	0.75
V-8	1.30	2.70	1.30
V-9	1.22	2.50	1.38
V-10	0.90	2.17	1.70
V-11	1.80	3.69	0.75
V-12	1.85	4.14	0.75
V-13	variable	3.12	1.75
V-14	variable	5.20	1.75
V-15	variable	3.18	1.75
V-16	1.05	3.20	1.75
V-17	1.05	5.00	2.15
V-18	1.05	3.20	1.55
V-19	1.05	5.21	1.55
V-20	2.28	3.55	0.52
V-21	1.98	5.21	1.22
V-22	2.13	2.06	0.47
V-23	1.10	1.38	1.17
V-24	2.28	4.42	0.52
V-25	2.28	3.52	0.52
V-26	2.28	5.21	0.52
V-27	2.28	3.59	0.52

CUADRO DE VANOS		
CODIGO	**ANCHO**	**ALTO**
P-1	2.08	2.60
P-2	1.51	2.80
P-3	2.55	2.60
P-4	1.00	2.80
P-5	1.55	2.10
P-6	0.62	2.50
P-7	0.70	1.75
P-8	2.95	2.80
P-9	1.50	2.60
P-10	1.19	3.20

gremsa
CONSULTORIA - OBRAS
INVERSIONES

LEVANTAMIENTO TOPOGRÁFICO INTEGRAL
DEL ESTADO ACTUAL A DETALLE DE LA
INFRAESTRUCTURA INTERIOR Y EXTERIOR
DE LA CIUDAD UNIVERSITARIA DE
PERAYOC-UNSAAC

PABELLON:
09. INFORMATICA Y SISTEMAS

PLANO:
PLANO DE DISTRIBUCION
PRIMER NIVEL

JEFE DE PROYECTO:
Arqto° JORGE SALCEDO QUISPE CAP 5812
EQUIPO TÉCNICO:
Arqto° AMED TEDILIO MOSCOSO TOLEDO CAP 13006
Arqta° NÉLIDA COANQUI SINCHI ROCA CAP 12517
Arqta° SOLANGE DIAZ CACERES CAP 12616
Arqta° VILMA CUSI DELGADO CAP 12615
Arqto° JUAN CARLOS PAUCAR VEGA CAP 11059
Bach. Arqta° JANIA CUSIQUISPE QUISPE
Bach. Arqto° DANDY BARRIENTOS RAMOS
Bach. Arqta° ADRIANA AIQUIPA ALOSILLA
Bach. Arqto° KENY CHOQUE INCACUTIPA
Asist. JHONATAN CASAVERDE CCOICCA

UBICACION:
CIUDAD UNIVERSITARIA DE PERAYOC
Distrito : CUSCO
Provincia : CUSCO
Departamento : CUSCO

ESCALA:
INDICADAS

FECHA:
Cusco, Diciembre del 2016

LAMINA:
P-09
AR - 01

CUADRO DE VANOS

CODIGO	ALFEIZER	ANCHO	ALTO
V-28	0.40	2.37	1.60
V-29	0.80	2.50	1.60
V-30	variable	2.70	1.60
V-31	variable	1.50	1.60
V-32	variable	1.70	1.60
V-33	0.45	3.88	0.75
V-34	0.45	3.93	0.75
V-35	0.71	2.55	1.54
V-36	1.26	2.70	0.99
V-37	1.26	2.50	0.99
V-38	0.71	2.45	1.54
V-39	1.68	3.50	0.72
V-40	variable	3.50	0.75
V-41	1.85	3.69	0.75
V-42	1.50	4.14	0.75
V-43	0.80	3.12	1.60
V-44	0.80	5.20	1.60
V-45	0.80	3.18	1.60
V-46	0.80	3.20	1.60
V-47	0.80	2.62	1.60
V-48	0.80	3.50	1.60
V-49	0.80	2.55	1.60
V-50	0.65	5.24	1.60
V-51	1.00	3.00	1.18
V-52	1.68	3.55	0.72
V-53	1.68	5.21	0.72
V-54	1.68	3.60	0.72
V-55	1.68	3.58	0.72
V-56	0.45	0.30	1.80
V-57	0.45	0.45	1.80
V-58	0.44	5.03	1.96
V-59	0.44	5.46	1.81
V-60	1.00	0.60	1.40
V-61	1.68	3.71	0.72
V-74	0.44	1.30	1.81

CODIGO	ANCHO	ALTO
P-4	1.00	2.80
P-6	0.62	2.50
P-11	1.51	2.40
P-12	1.89	2.25
P-13	0.82	2.80
M-1	1.49	2.60

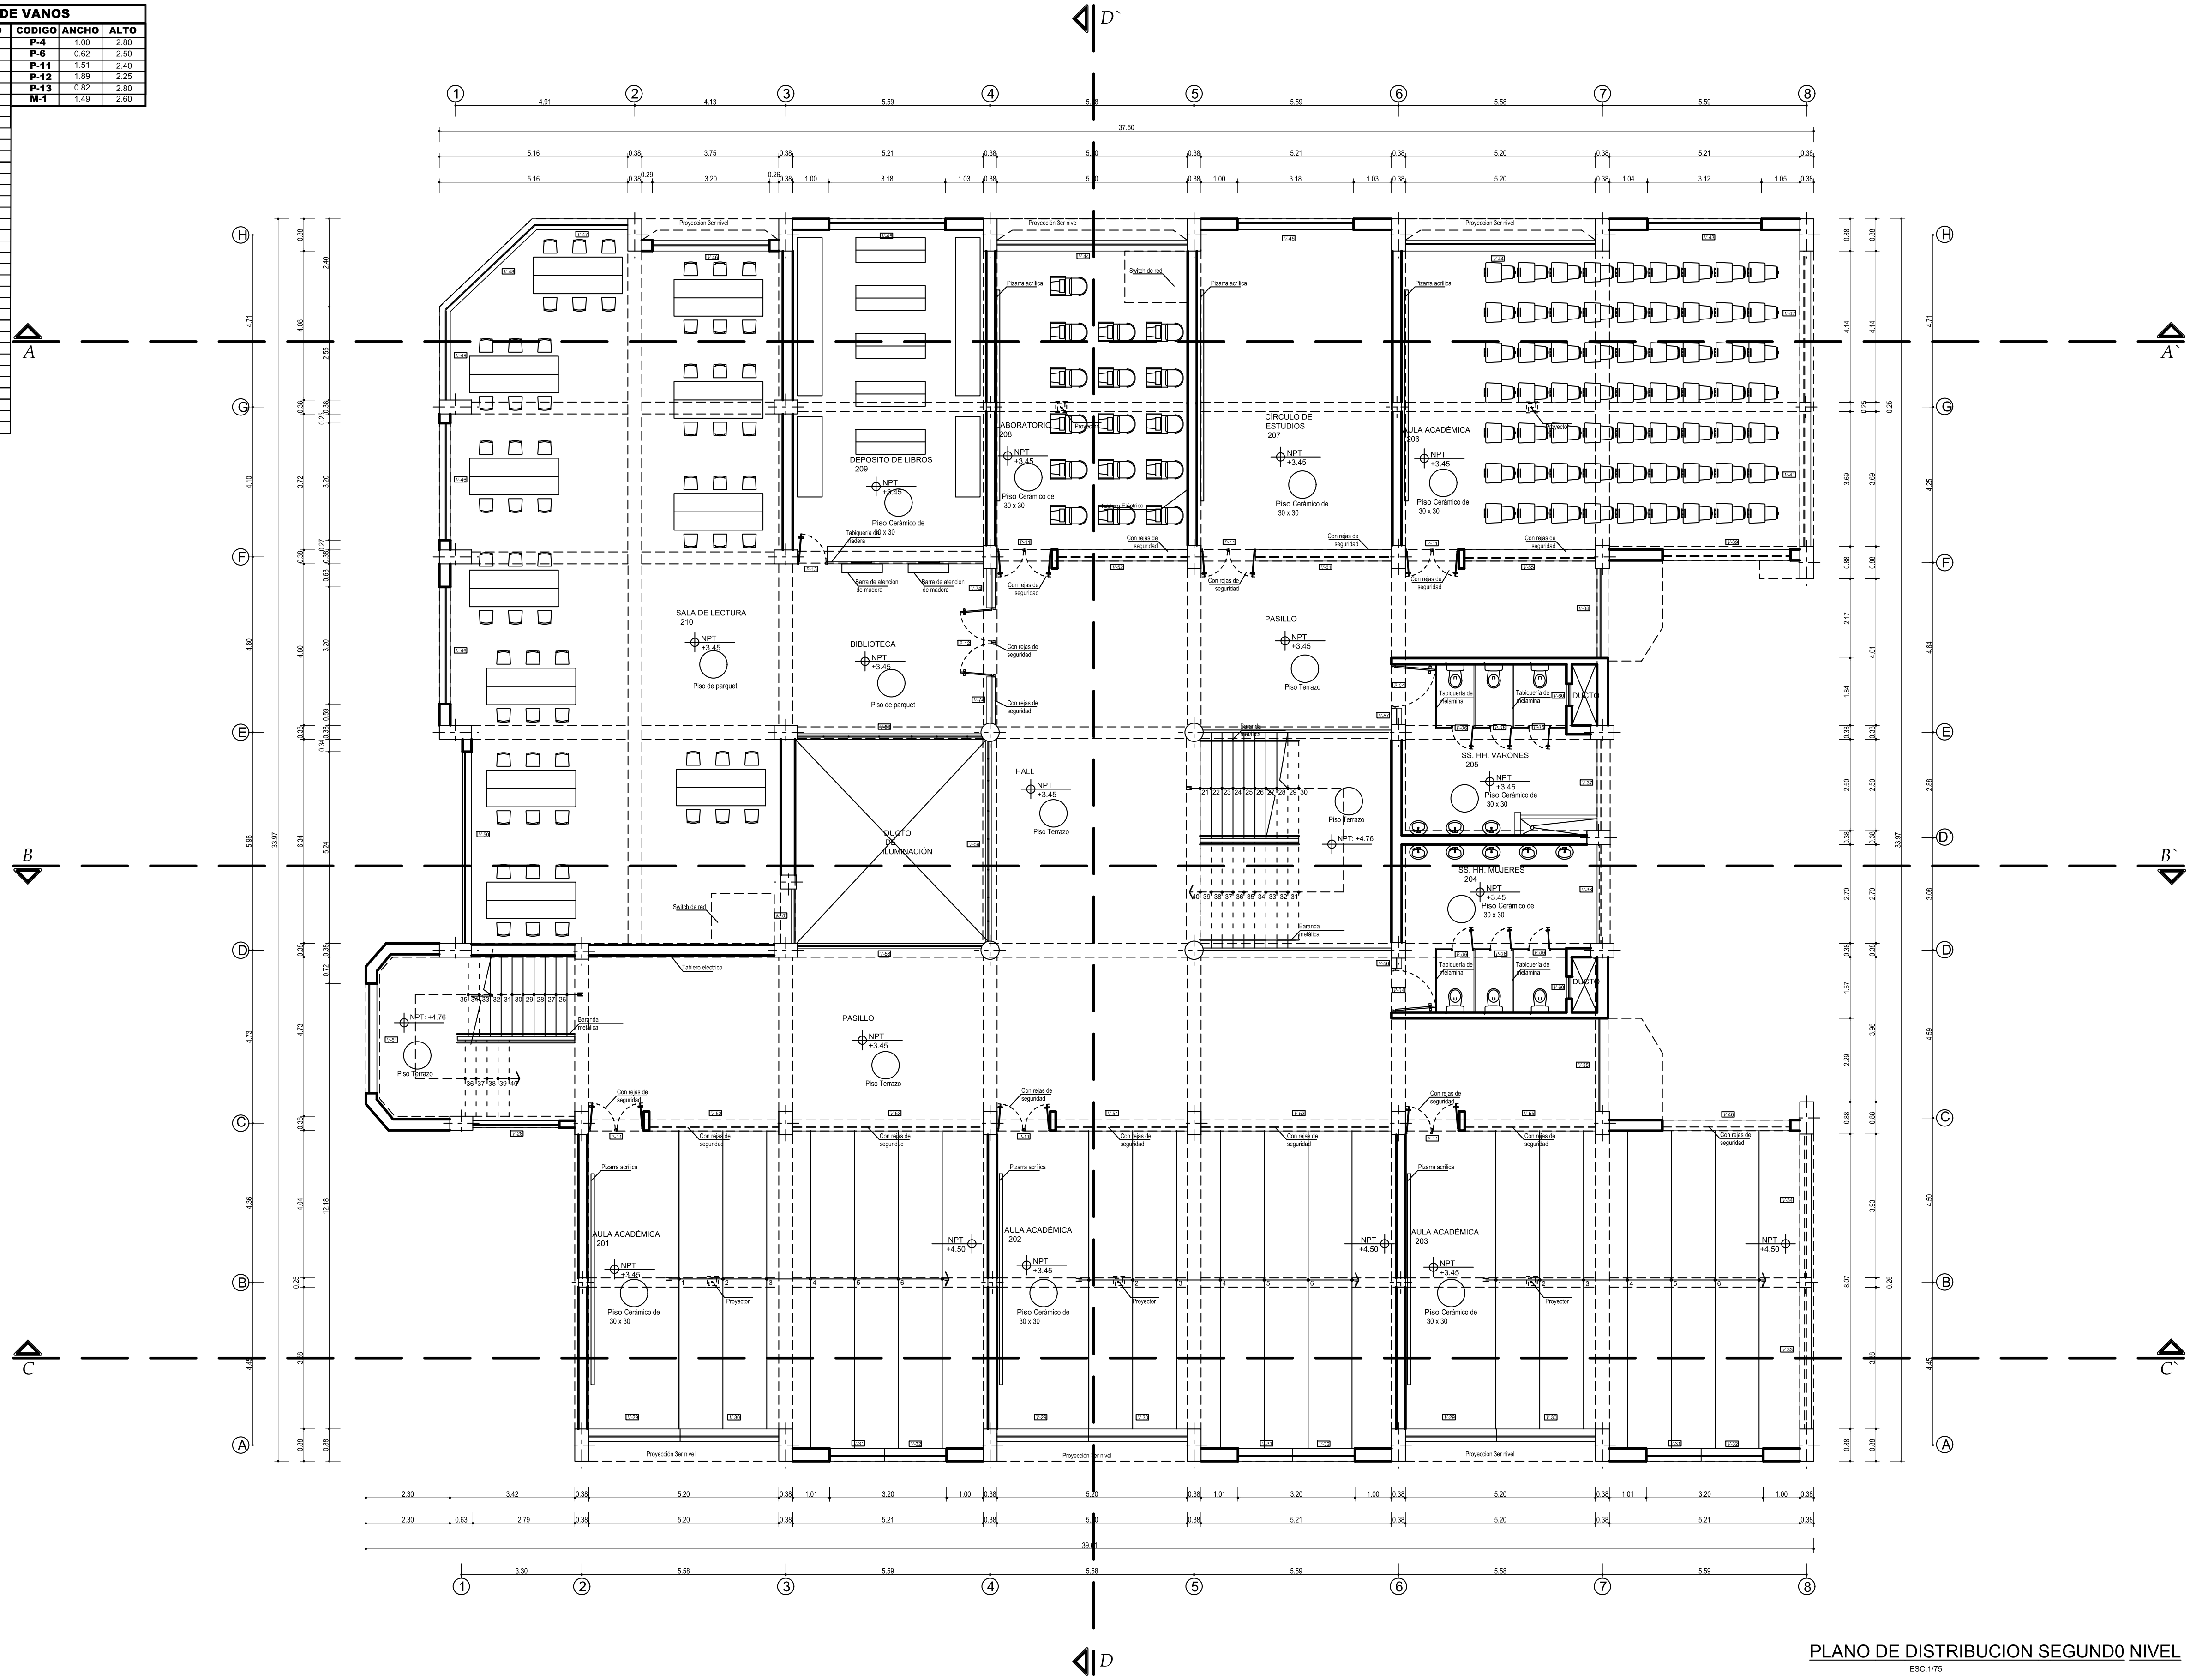

D`
D
A
A`
B
B`
C
C`
1
2
3
4
5
6
7
8
H
G
F
E
D
C
B
A
37.60
39.61
Proyección 3er nivel
DEPOSITO DE LIBROS
209
LABORATORIO
208
CIRCULO DE ESTUDIOS
207
AULA ACADÉMICA
206
SALA DE LECTURA
210
BIBLIOTECA
PASILLO
HALL
DUCTO DE ILUMINACIÓN
SS. HH. VARONES
205
SS. HH. MUJERES
204
DUCTO
AULA ACADÉMICA
201
AULA ACADÉMICA
202
AULA ACADÉMICA
203
NPT
+3.45
NPT: +4.76
NPT
+4.50
Piso de parquet
Piso Cerámico de 30 x 30
Piso Terrazo
Pizarra acrílica
Switch de red
Tablero eléctrico
Con rejas de seguridad
Barra de atencion de madera
Tabiquería de madera
Tabiquería de melamina
Baranda metálica
Proyector

PLANO DE DISTRIBUCION SEGUND0 NIVEL

ESC:1/75

gremsa
CONSULTORIA - OBRAS
INVERSIONES

LEVANTAMIENTO TOPOGRÁFICO INTEGRAL DEL ESTADO ACTUAL A DETALLE DE LA INFRAESTRUCTURA INTERIOR Y EXTERIOR DE LA CIUDAD UNIVERSITARIA DE PERAYOC-UNSAAC

PABELLON:
09. INFORMATICA Y SISTEMAS

PLANO:
PLANO DE DISTRIBUCION
SEGUNDO NIVEL

JEFE DE PROYECTO:
Arqto° JORGE SALCEDO QUISPE CAP 5812

EQUIPO TÉCNICO:
Arqto° AMED TEDILIO MOSCOSO TOLEDO CAP 13006
Arqta° NÉLIDA COANQUI SINCHI ROCA CAP 12517
Arqta° SOLANGE DIAZ CACERES CAP 12616
Arqta° VILMA CUSI DELGADO CAP 12615
Arqto° JUAN CARLOS PAUCAR VEGA CAP 11059
Bach. Arqta° JANIA CUSIQUISPE QUISPE
Bach. Arqto° DANDY BARRIENTOS RAMOS
Bach. Arqta° ADRIANA AIQUIPA ALOSILLA
Bach. Arqto° KENY CHOQUE INCACUTIPA
Asist. JHONATAN CASAVERDE CCOICCA

UBICACION:
CIUDAD UNIVERSITARIA DE PERAYOC
Distrito : CUSCO
Provincia : CUSCO
Departamento : CUSCO

ESCALA:
INDICADAS

FECHA:
Cusco, Diciembre del 2016

LAMINA:
P-09
AR - 02

CUADRO DE VANOS						
CODIGO	**ALFEIZER**	**ANCHO**	**ALTO**	**CODIGO**	**ANCHO**	**ALTO**
V-29	0.80	2.50	1.60	**P-4**	1.00	2.80
V-30	variable	2.70	1.60	**P-6**	0.62	2.50
V-31	variable	1.50	1.60	**P-11**	1.51	2.40
V-32	variable	1.70	1.60	**P-14**	1.89	2.25
V-36	1.26	2.70	0.99	**P-15**	0.90	2.80
V-37	1.26	2.50	0.99	**P-16**	0.95	2.25
V-39	1.68	3.50	0.72	**P-17**	0.80	2.80
V-41	1.85	3.69	0.75	**P-18**	1.50	2.25
V-42	1.50	4.14	0.75	**M-1**	1.49	2.60
V-43	0.80	3.12	1.60	**M-3**	4.16	2.08
V-44	0.80	5.20	1.60			
V-45	0.80	3.18	1.60			
V-46	0.80	3.20	1.60			
V-47	0.80	2.62	1.60			
V-48	0.80	3.50	1.60			
V-49	0.80	2.55	1.60			
V-50	0.80	5.24	1.60			
V-56	0.45	0.30	1.80			
V-57	0.45	0.45	1.80			
V-58	0.44	5.03	1.96			
V-59	0.44	5.46	1.81			
V-60	1.00	0.60	1.40			
V-62	0.40	2.37	1.60			
V-63	1.05	3.88	0.75			
V-64	1.05	3.93	0.75			
V-65	variable	3.48	0.75			
V-66	1.00	3.00	1.86			
V-67	1.90	3.55	0.50			
V-68	1.90	359	0.50			
V-69	1.90	3.60	0.50			
V-70	1.90	3.58	0.50			
V-71	1.66	3.70	0.74			
V-72	0.95	1.75	1.30			
V-73	1.00	0.80	1.30			

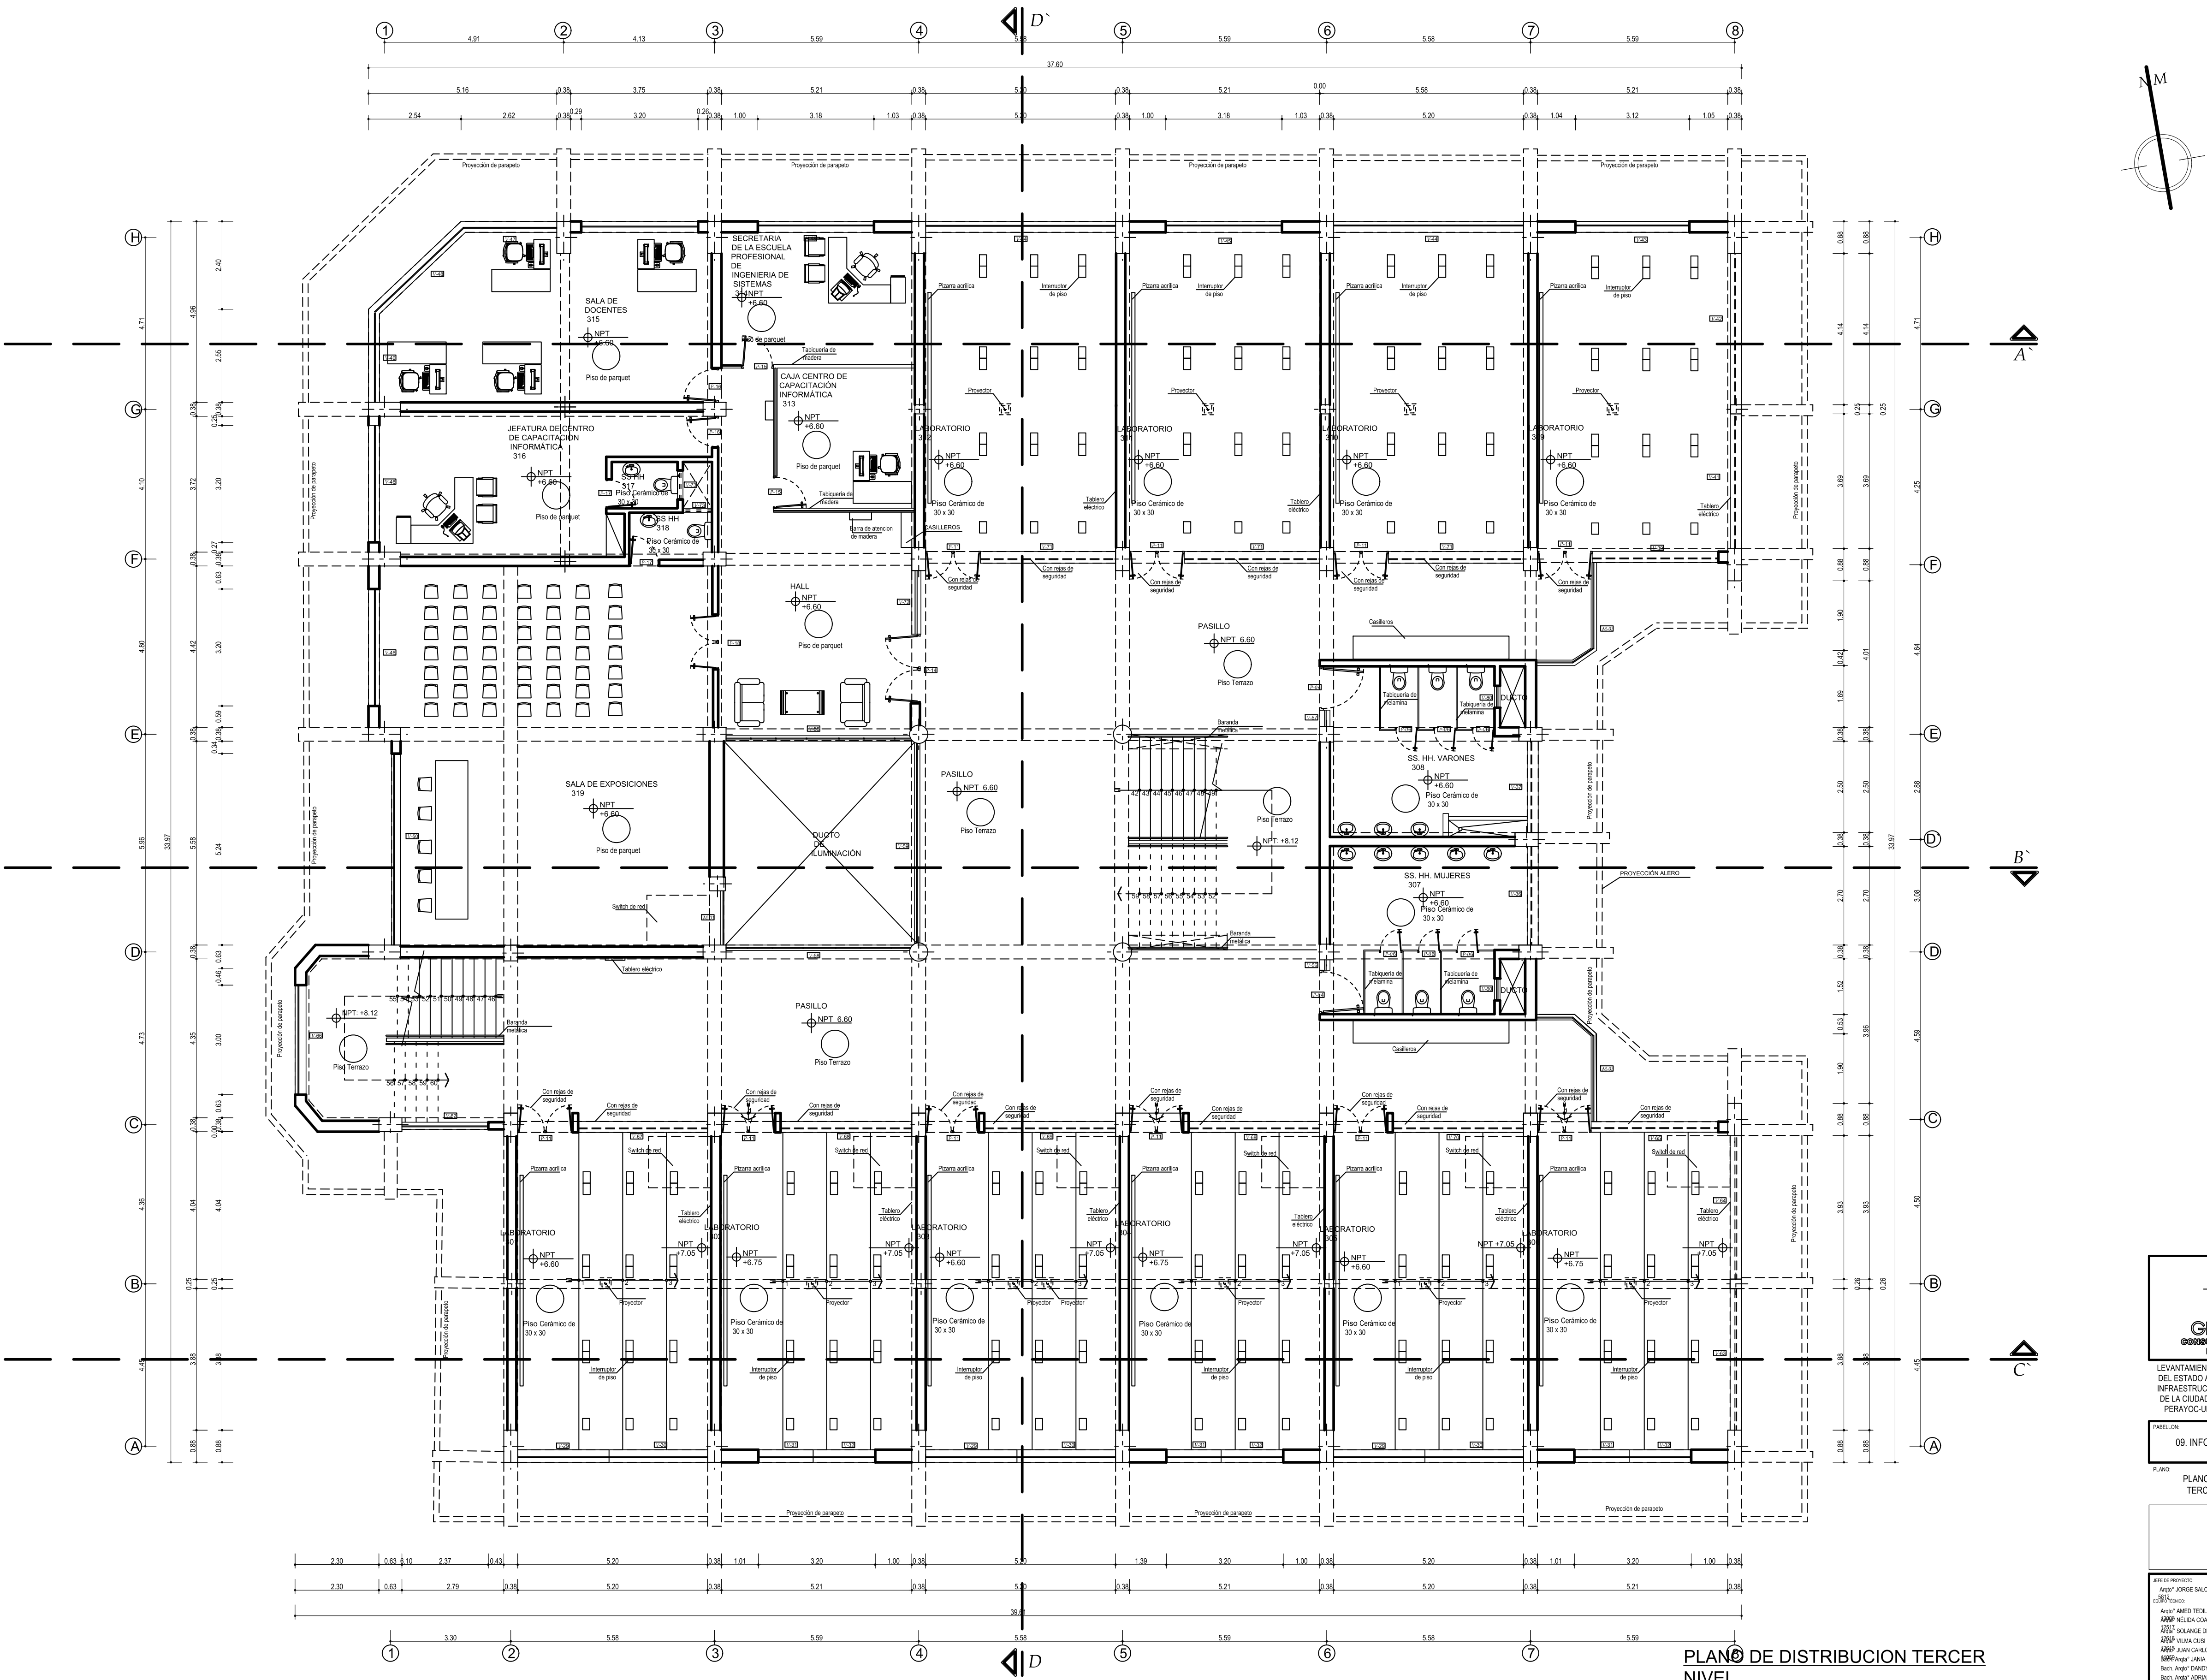
A
A`
B
B`
C
C`
D`
D
1
2
3
4
5
6
7
8
H
G
F
E
D
C
B
A
37.60
39.60
NM
SECRETARIA DE LA ESCUELA PROFESIONAL DE INGENIERIA DE SISTEMAS
SALA DE DOCENTES 315
NPT +6.60
Piso de parquet
CAJA CENTRO DE CAPACITACIÓN INFORMÁTICA 313
JEFATURA DE CENTRO DE CAPACITACIÓN INFORMÁTICA 316
SS HH 317
SS HH 318
Piso Cerámico de 30 x 30
HALL
SALA DE EXPOSICIONES 319
DUCTO DE ILUMINACIÓN
PASILLO
NPT 6.60
Piso Terrazo
LABORATORIO
Pizarra acrílica
Interruptor de piso
Proyector
Tablero eléctrico
Con rejas de seguridad
Switch de red
SS. HH. VARONES 308
SS. HH. MUJERES 307
Tabiquería de melamina
DUCTO
Casilleros
Baranda metálica
NPT +8.12
NPT +7.05
NPT +6.75
Proyección de parapeto
PROYECCIÓN ALERO

PLANO DE DISTRIBUCION TERCER NIVEL

ESC:1/75

gremsa
CONSULTORIA - OBRAS
INVERSIONES

LEVANTAMIENTO TOPOGRÁFICO INTEGRAL DEL ESTADO ACTUAL A DETALLE DE LA INFRAESTRUCTURA INTERIOR Y EXTERIOR DE LA CIUDAD UNIVERSITARIA DE PERAYOC-UNSAAC

PABELLON:
09. INFORMATICA Y SISTEMAS

PLANO:
PLANO DE DISTRIBUCION TERCER NIVEL

JEFE DE PROYECTO:
Arqto° JORGE SALCEDO QUISPE CAP 5812

EQUIPO TÉCNICO:
Arqto° AMED TEDILIO MOSCOSO TOLEDO CAP 13006
Arqta° NÉLIDA COANQUI SINCHI ROCA CAP 12517
Arqta° SOLANGE DIAZ CACERES CAP 12616
Arqta° VILMA CUSI DELGADO CAP 12615
Arqto° JUAN CARLOS PAUCAR VEGA CAP 11059
Bach. Arqta° JANIA CUSIQUISPE QUISPE
Bach. Arqto° DANDY BARRIENTOS RAMOS
Bach. Arqta° ADRIANA AIQUIPA ALOSILLA
Bach. Arqto° KENY CHOQUE INCACUTIPA
Asist. JHONATAN CASAVERDE CCOICCA

UBICACION:
CIUDAD UNIVERSITARIA DE PERAYOC
Distrito : CUSCO
Provincia : CUSCO
Departamento : CUSCO

ESCALA:
INDICADAS

FECHA:
Cusco, Diciembre del 2016

LAMINA:
P-09
AR - 03

CUADRO DE VANOS

CODIGO	ALFEIZER	ANCHO	ALTO
V-75	1.20	1.34	variable
V-76	1.20	0.78	variable
V-77	1.20	1.40	1.67
V-78	1.20	2.04	1.67
V-79	1.20	2.26	1.67
V-80	1.20	2.24	1.67
V-81	1.20	2.25	1.67
V-82	1.20	3.30	1.67
V-83	1.20	1.20	1.67
V-84	0.31	2.40	2.56
V-85	0.72	4.25	2.15
V-86	0.31	3.20	2.56
V-87	0.72	5.50	2.15
V-88	0.72	3.62	2.15
V-89	1.20	3.20	1.67
V-90	1.95	1.60	0.92
V-91	1.72	1.62	1.00
V-92	1.69	0.77	0.90
V-93	1.70	0.77	1.99
V-94	1.72	1.62	1.00
V-95	1.69	1.62	0.89
V-96	1.69	1.63	0.89
V-97	0.31	2.66	2.56
V-98	0.31	3.33	2.56
V-99	0.31	1.29	2.56
V-100	0.31	1.99	2.56
V-101	0.31	2.16	2.56
V-102	0.31	3.19	2.56
V-103	0.31	2.74	2.56
V-104	1.20	4.33	1.67
V-105	1.20	5.80	1.67
V-106	1.75	5.50	1.67
V-107	0.70	5.67	2.17
V-108	0.70	6.14	2.17

CODIGO	ANCHO	ALTO
P-19	1.00	2.80
P-20	2.40	2.87
P-21	1.00	2.15
P-22	1.00	2.10
P-23	1.62	2.80
M-2	2.02	2.87

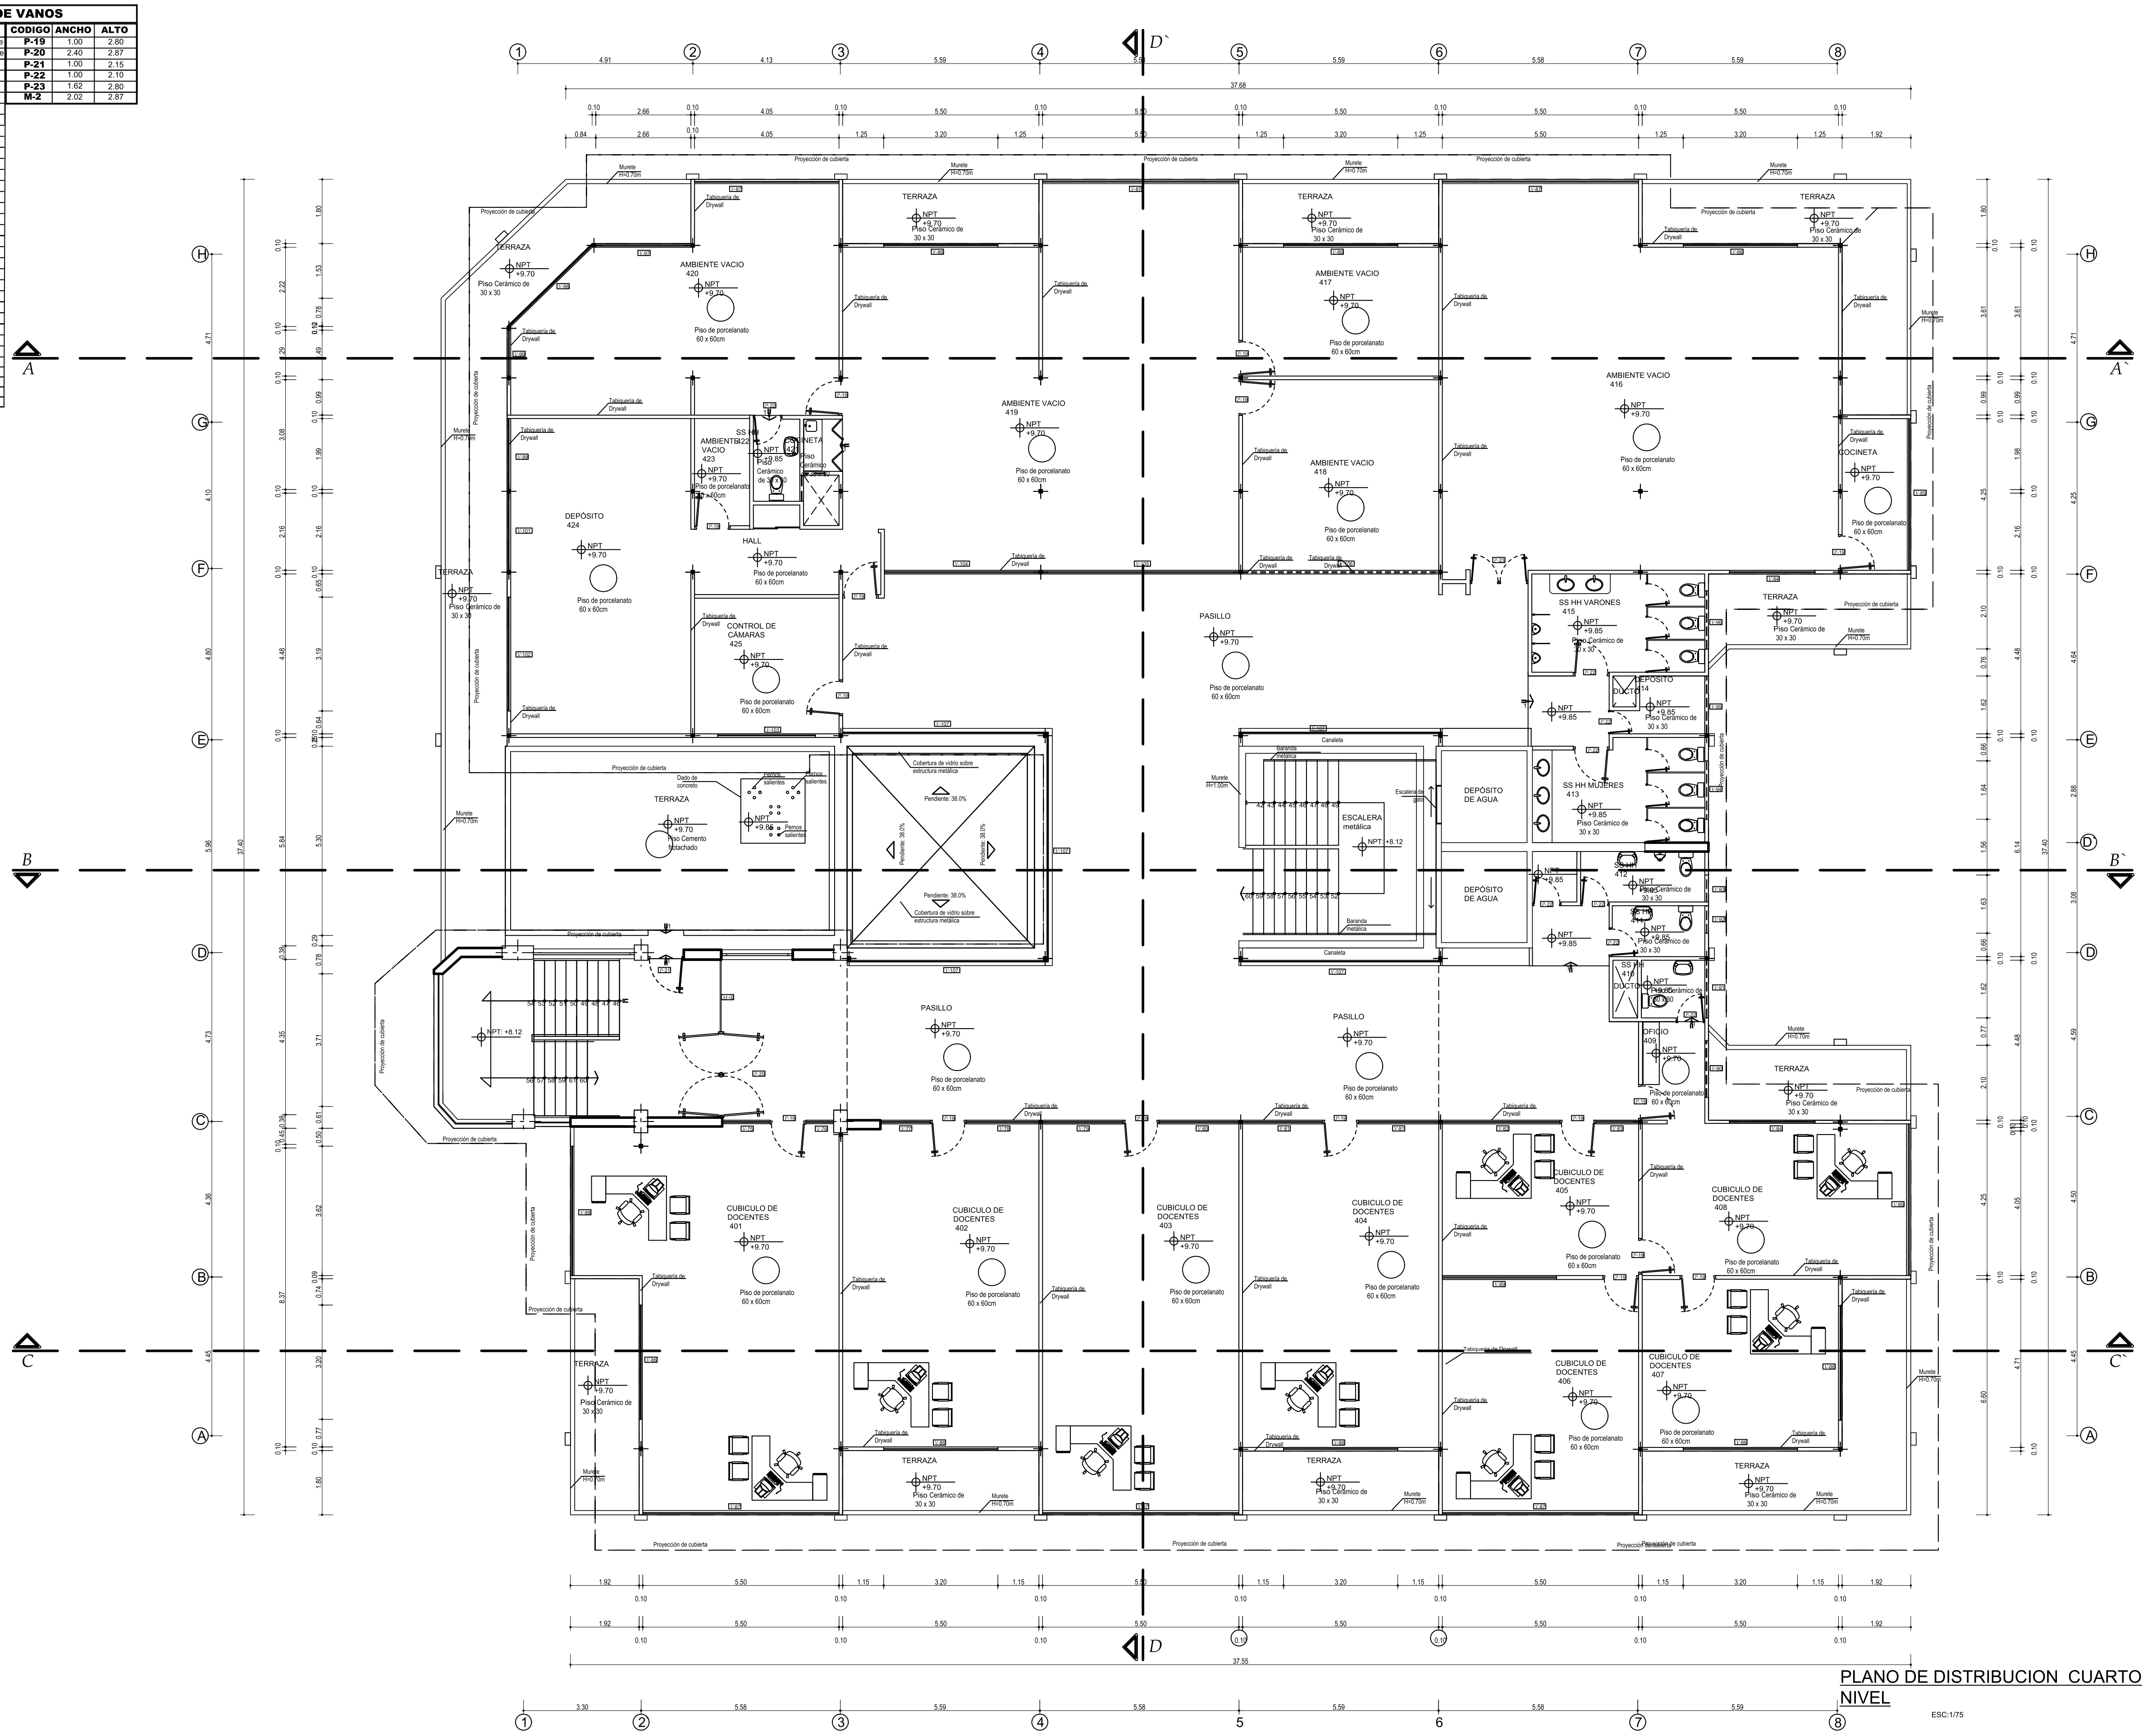

D`
D
A
A`
B
B`
C
C`
TERRAZA
AMBIENTE VACIO 420
AMBIENTE VACIO 419
AMBIENTE VACIO 417
AMBIENTE VACIO 418
AMBIENTE VACIO 416
AMBIENTE VACIO 423
SS HH 422
COCINETA
DEPÓSITO 424
HALL
CONTROL DE CÁMARAS 425
PASILLO
SS HH VARONES 415
DEPÓSITO 414
SS HH MUJERES 413
DEPÓSITO DE AGUA
ESCALERA metálica
OFICIO 409
CUBICULO DE DOCENTES 401
CUBICULO DE DOCENTES 402
CUBICULO DE DOCENTES 403
CUBICULO DE DOCENTES 404
CUBICULO DE DOCENTES 405
CUBICULO DE DOCENTES 406
CUBICULO DE DOCENTES 407
CUBICULO DE DOCENTES 408
NPT +9.70
NPT +9.85
NPT +8.12
Piso de porcelanato 60 x 60cm
Piso Cerámico de 30 x 30
Piso Cemento frotachado
Tabiquería de Drywall
Proyección de cubierta
Murete H=0.70m
Cobertura de vidrio sobre estructura metálica
Pendiente 38.0%
Canaleta
Baranda metálica
37.68
37.55
37.40

PLANO DE DISTRIBUCION CUARTO NIVEL

ESC:1/75

gremsa
CONSULTORIA - OBRAS
INVERSIONES

LEVANTAMIENTO TOPOGRÁFICO INTEGRAL DEL ESTADO ACTUAL A DETALLE DE LA INFRAESTRUCTURA INTERIOR Y EXTERIOR DE LA CIUDAD UNIVERSITARIA DE PERAYOC-UNSAAC

PABELLON:
09. INFORMATICA Y SISTEMAS

PLANO:
PLANO DE DISTRIBUCION
CUARTO NIVEL

JEFE DE PROYECTO:
Arqto° JORGE SALCEDO QUISPE CAP 5812

EQUIPO TÉCNICO:
Arqto° AMED TEDILIO MOSCOSO TOLEDO CAP 13006
Arqta° NÉLIDA COANQUI SINCHI ROCA CAP 12517
Arqta° SOLANGE DIAZ CACERES CAP 12616
Arqta° VILMA CUSI DELGADO CAP 12615
Arqto° JUAN CARLOS PAUCAR VEGA CAP 11059
Bach. Arqta° JANIA CUSIQUISPE QUISPE
Bach. Arqto° DANDY BARRIENTOS RAMOS
Bach. Arqta° ADRIANA AIQUIPA ALOSILLA
Bach. Arqto° KENY CHOQUE INCACUTIPA
Asist. JHONATAN CASAVERDE CCOICCA

UBICACION:
CIUDAD UNIVERSITARIA DE PERAYOC
Distrito : CUSCO
Provincia : CUSCO
Departamento : CUSCO

ESCALA:
INDICADAS

FECHA:
Cusco, Diciembre del 2016

LAMINA:
P-09
AR - 04

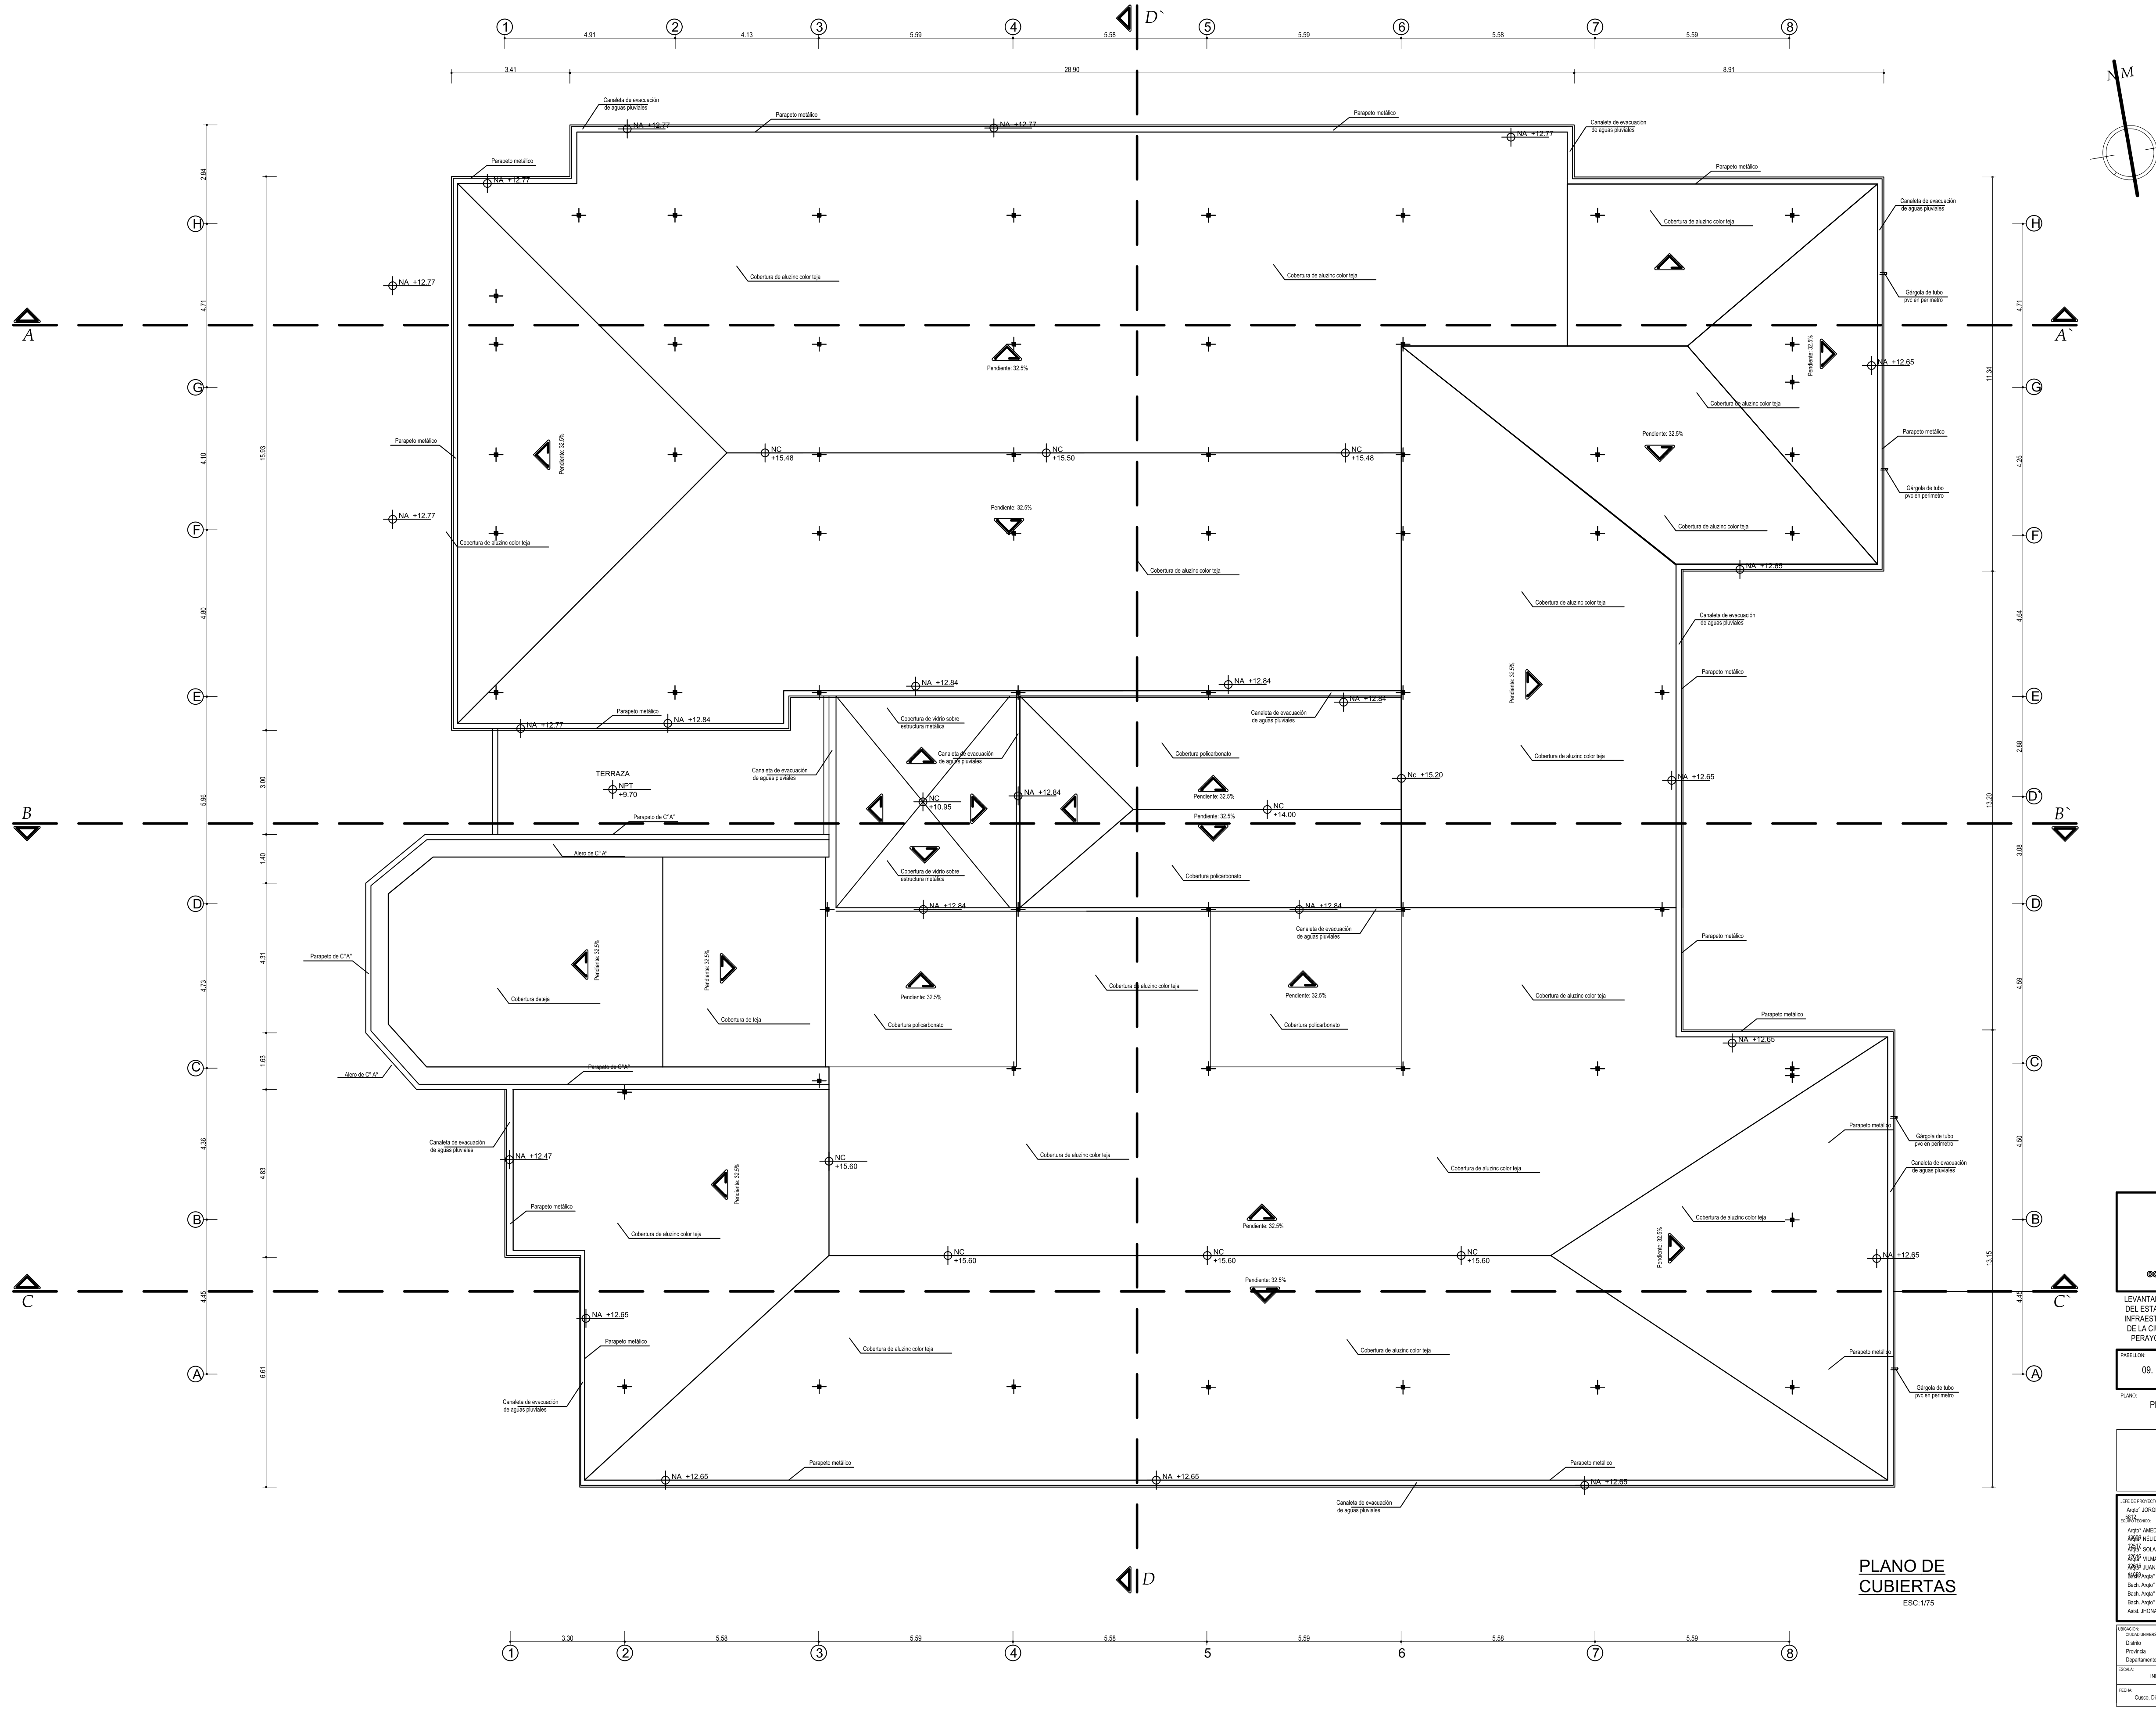

D`
D
A
A`
B
B`
C
C`
1
2
3
4
5
6
7
8
H
G
F
E
D
C
B
A
N M
4.91
4.13
5.59
5.58
5.59
5.58
5.59
3.41
28.90
8.91
3.30
5.58
5.59
5.58
5.59
5.58
5.59
2.84
4.71
4.10
4.80
5.96
4.73
4.36
4.45
15.93
3.00
1.40
4.31
1.63
4.83
6.61
11.34
4.25
4.64
2.68
3.06
4.59
4.50
4.45
13.20
13.15
Canaleta de evacuación de aguas pluviales
Parapeto metálico
Cobertura de aluzinc color teja
Pendiente: 32.5%
Gárgola de tubo pvc en perimetro
NA +12.77
NA +12.84
NA +12.65
NA +12.47
NC +15.48
NC +15.50
NC +15.60
NC +10.95
NC +14.00
Nc +15.20
TERRAZA
NPT +9.70
Parapeto de C°A°
Alero de C° A°
Cobertura deteja
Cobertura de teja
Cobertura de vidrio sobre estructura metálica
Cobertura policarbonato

PLANO DE CUBIERTAS

ESC:1/75

gremsa
CONSULTORIA - OBRAS
INVERSIONES

LEVANTAMIENTO TOPOGRÁFICO INTEGRAL DEL ESTADO ACTUAL A DETALLE DE LA INFRAESTRUCTURA INTERIOR Y EXTERIOR DE LA CIUDAD UNIVERSITARIA DE PERAYOC-UNSAAC

PABELLON:
09. INFORMATICA Y SISTEMAS

PLANO:
PLANO DE CUBIERTAS

JEFE DE PROYECTO:
Arqto° JORGE SALCEDO QUISPE CAP 5812
EQUIPO TÉCNICO:
Arqto° AMED TEDILIO MOSCOSO TOLEDO CAP 13006
Arqta° NÉLIDA COANQUI SINCHI ROCA CAP 12517
Arqta° SOLANGE DIAZ CACERES CAP 12616
Arqta° VILMA CUSI DELGADO CAP 12615
Arqto° JUAN CARLOS PAUCAR VEGA CAP 11059
Bach. Arqta° JANIA CUSIQUISPE QUISPE
Bach. Arqto° DANDY BARRIENTOS RAMOS
Bach. Arqta° ADRIANA AIQUIPA ALOSILLA
Bach. Arqto° KENY CHOQUE INCACUTIPA
Asist. JHONATAN CASAVERDE CCOICCA

UBICACION:
CIUDAD UNIVERSITARIA DE PERAYOC
Distrito : CUSCO
Provincia : CUSCO
Departamento : CUSCO

ESCALA:
INDICADAS

FECHA:
Cusco, Diciembre del 2016

LAMINA:
P-09
AR - 05

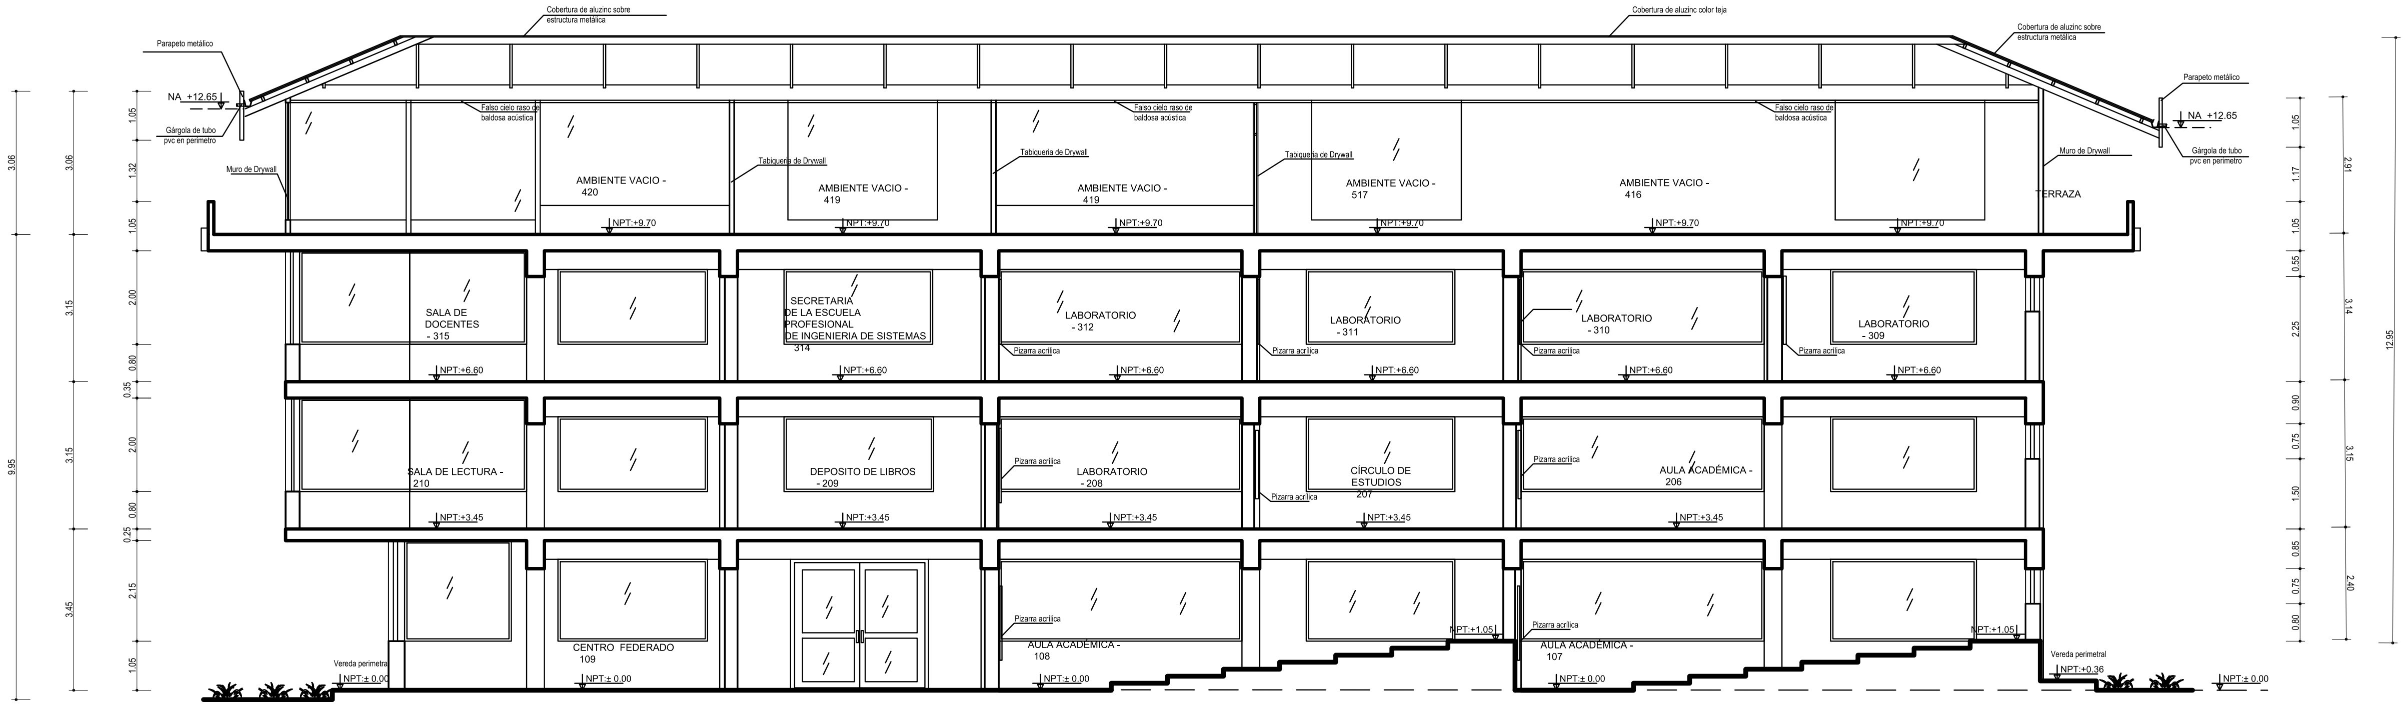
Cobertura de aluzinc sobre estructura metálica
Cobertura de aluzinc color teja
Parapeto metálico
NA. +12.65
Gárgola de tubo pvc en perímetro
Falso cielo raso de baldosa acústica
Tabiquería de Drywall
Muro de Drywall
AMBIENTE VACIO - 420
AMBIENTE VACIO - 419
AMBIENTE VACIO - 419
AMBIENTE VACIO - 517
AMBIENTE VACIO - 416
TERRAZA
NPT:+9.70
SALA DE DOCENTES - 315
SECRETARIA DE LA ESCUELA PROFESIONAL DE INGENIERIA DE SISTEMAS 314
LABORATORIO - 312
LABORATORIO - 311
LABORATORIO - 310
LABORATORIO - 309
Pizarra acrílica
NPT:+6.60
SALA DE LECTURA - 210
DEPOSITO DE LIBROS - 209
LABORATORIO - 208
CÍRCULO DE ESTUDIOS 207
AULA ACADÉMICA - 206
NPT:+3.45
CENTRO FEDERADO 109
AULA ACADÉMICA - 108
AULA ACADÉMICA - 107
NPT:+1.05
Vereda perimetral
NPT:± 0.00
NPT:+0.36
12.95
9.95

CORTE A - A´

ESC:1/75

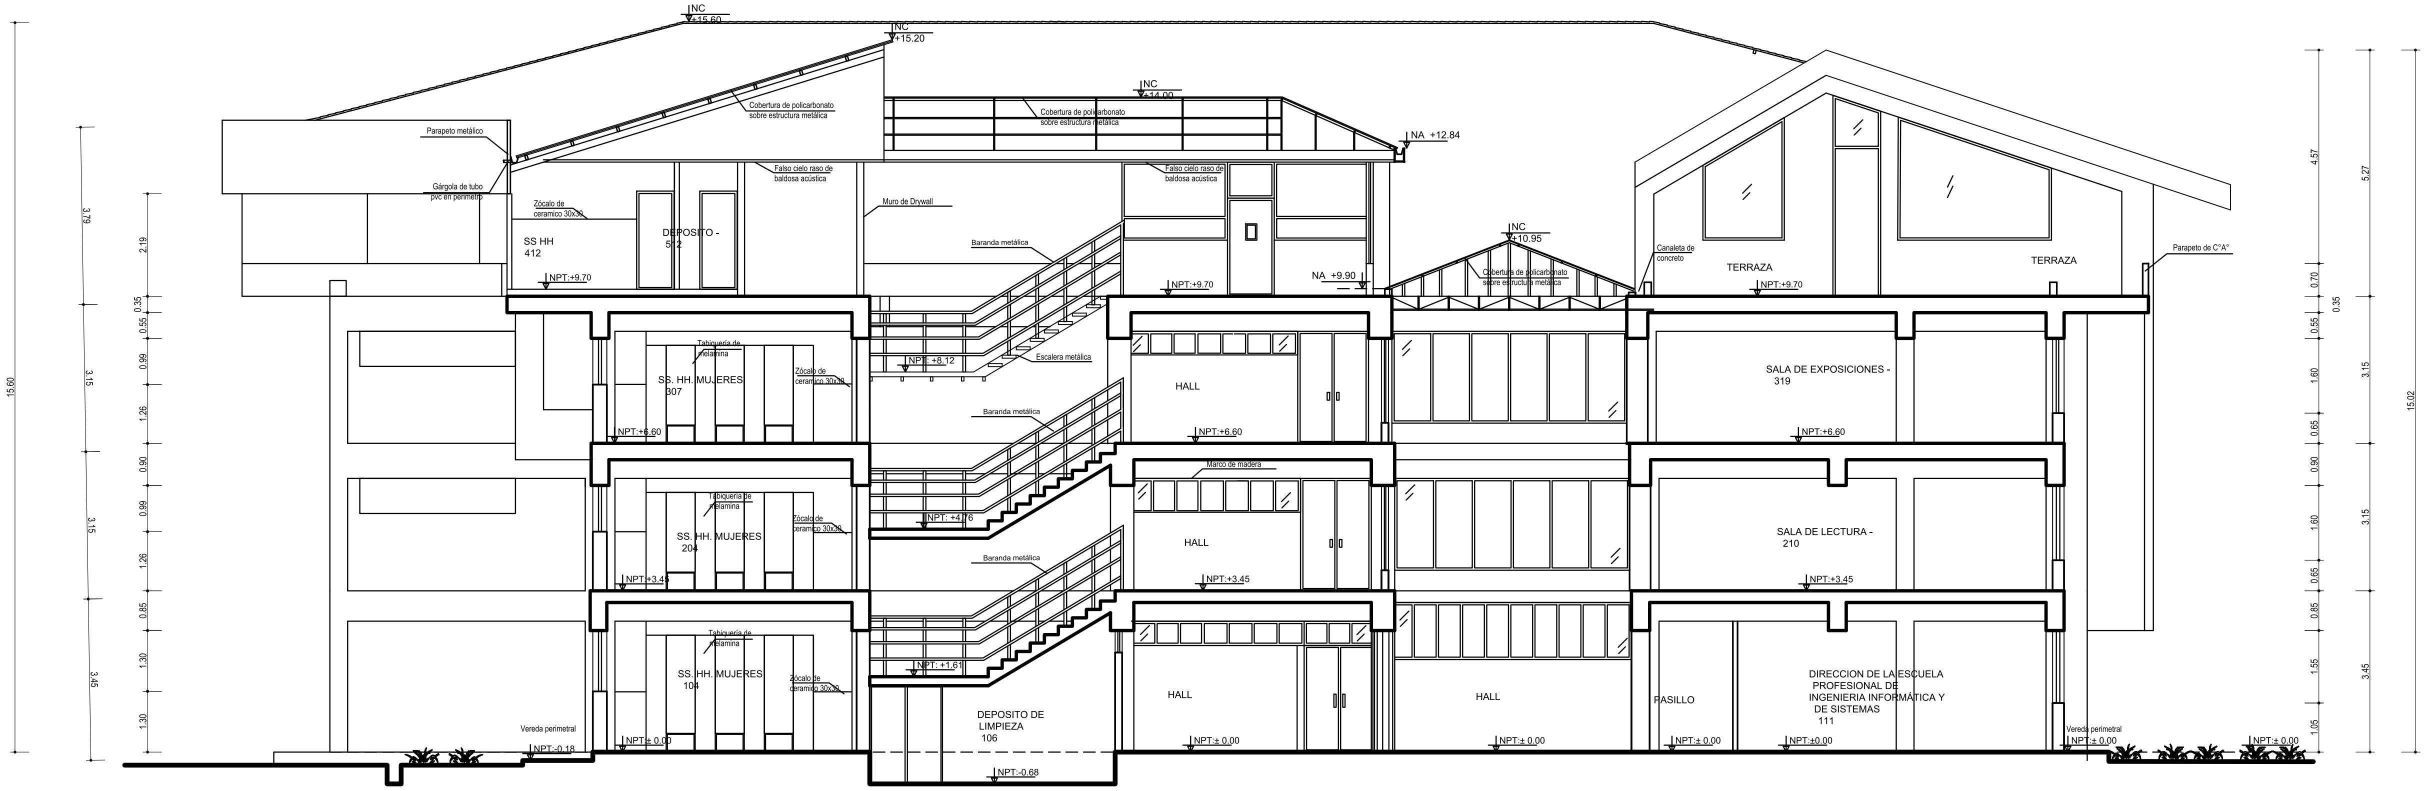
NC +15.60
NC +15.20
NC +14.00
NA +12.84
NC +10.95
NA +9.90
Cobertura de policarbonato sobre estructura metálica
Parapeto metálico
Gárgola de tubo pvc en perímetro
Falso cielo raso de baldosa acústica
Muro de Drywall
Zócalo de cerámico 30x30
SS HH 412
DEPOSITO - 512
Baranda metálica
Escalera metálica
Canaleta de concreto
Parapeto de C°A°
TERRAZA
TERRAZA
NPT:+9.70
SS. HH. MUJERES 307
NPT:+8.12
HALL
SALA DE EXPOSICIONES - 319
NPT:+6.60
Tabiquería de melamina
Marco de madera
SS. HH. MUJERES 204
NPT:+4.78
HALL
SALA DE LECTURA - 210
NPT:+3.45
SS. HH. MUJERES 104
NPT: +1.61
DEPOSITO DE LIMPIEZA 106
HALL
HALL
PASILLO
DIRECCION DE LA ESCUELA PROFESIONAL DE INGENIERIA INFORMATICA Y DE SISTEMAS 111
Vereda perimetral
NPT:-0.18
NPT:± 0.00
NPT:-0.68
15.60
15.02

CORTE B - B´

ESC:1/75

GREMSA
CONSULTORIA - OBRAS
INVERSIONES

LEVANTAMIENTO TOPOGRÁFICO INTEGRAL
DEL ESTADO ACTUAL A DETALLE DE LA
INFRAESTRUCTURA INTERIOR Y EXTERIOR
DE LA CIUDAD UNIVERSITARIA DE
PERAYOC-UNSAAC

PABELLON:
09. INFORMATICA Y SISTEMAS

PLANO:
CORTES

JEFE DE PROYECTO:
Arqto° JORGE SALCEDO QUISPE CAP 5812

EQUIPO TÉCNICO:
Arqto° AMED TEDILIO MOSCOSO TOLEDO CAP 13006
Arqta° NÉLIDA COANQUI SINCHI ROCA CAP 12517
Arqta° SOLANGE DIAZ CACERES CAP 12616
Arqta° VILMA CUSI DELGADO CAP 12615
Arqto° JUAN CARLOS PAUCAR VEGA CAP 11059
Bach. Arqta° JANIA CUSIQUISPE QUISPE
Bach. Arqto° DANDY BARRIENTOS RAMOS
Bach. Arqta° ADRIANA AIQUIPA ALOSILLA
Bach. Arqto° KENY CHOQUE INCACUTIPA
Asist. JONATAN CASAVERDE CCOICCA

UBICACION:
CIUDAD UNIVERSITARIA DE PERAYOC
Distrito : CUSCO
Provincia : CUSCO
Departamento : CUSCO

ESCALA:
INDICADAS

FECHA:
Cusco, Diciembre del 2016

LAMINA:
P-09
AR - 06

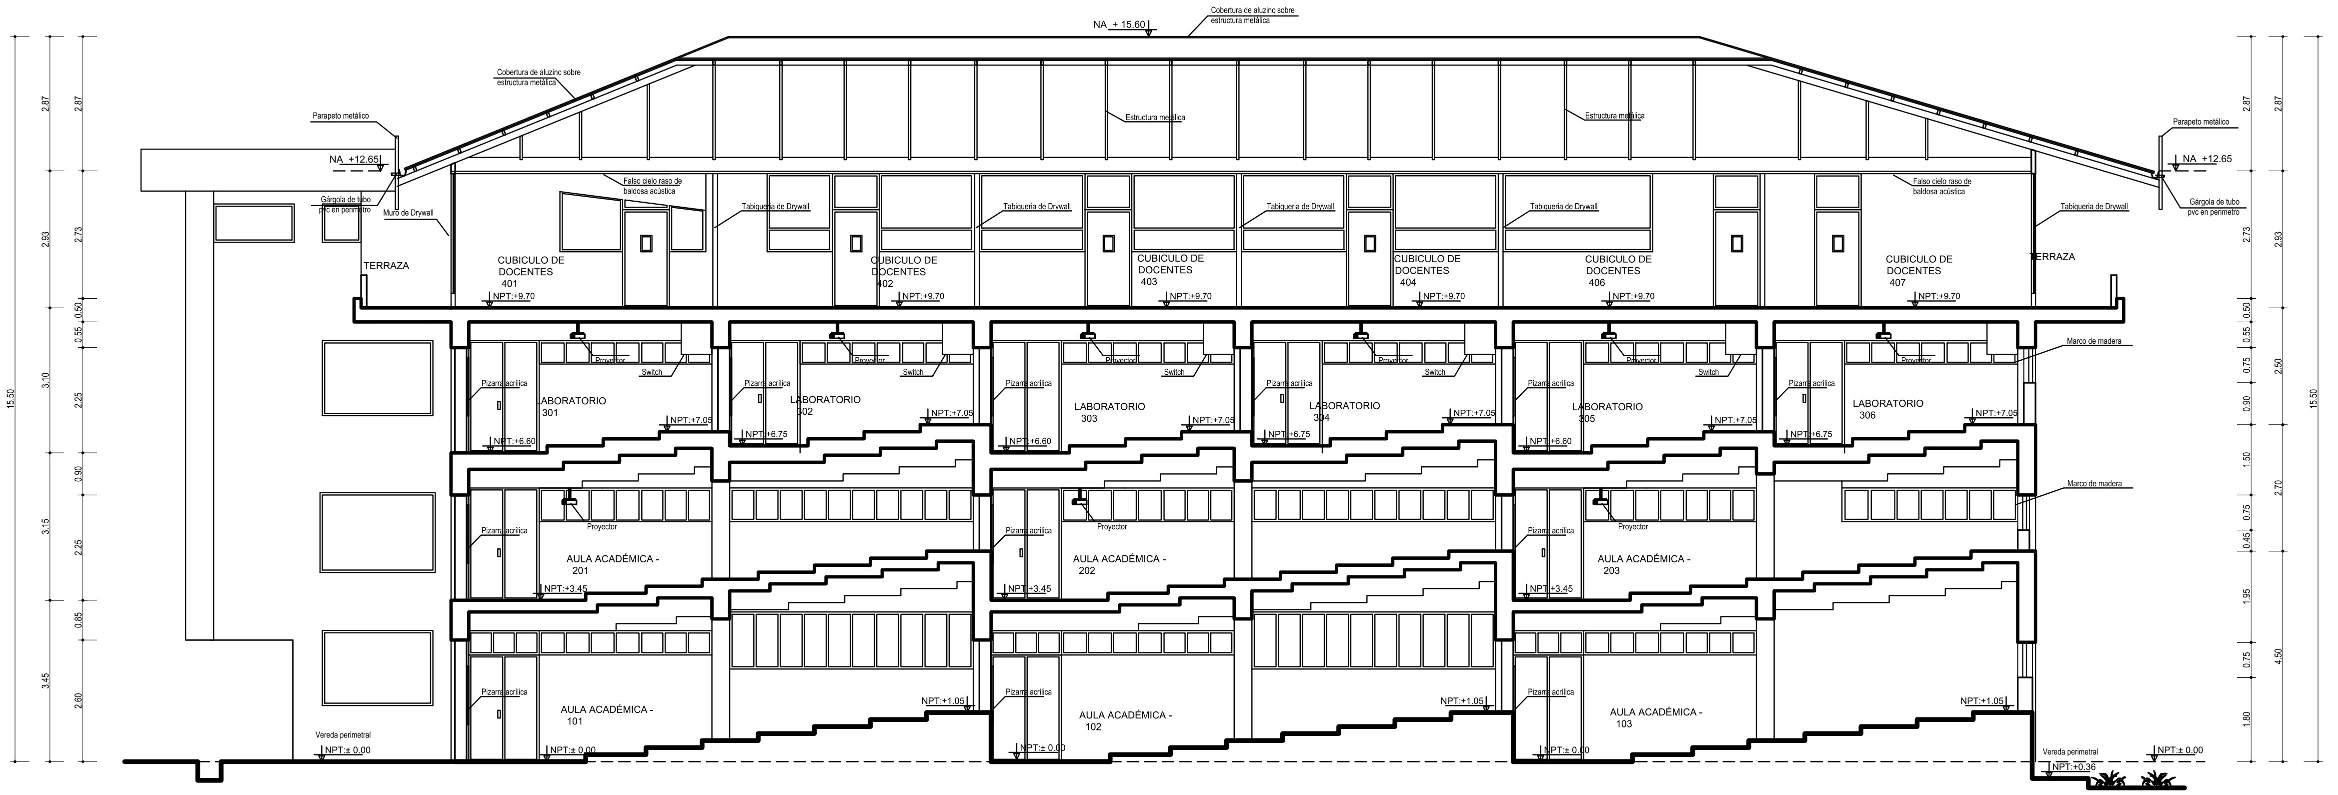
NA + 15.60
Cobertura de aluzinc sobre estructura metálica
Parapeto metálico
NA +12.65
Gárgola de tubo pvc en perimetro
Muro de Drywall
Falso cielo raso de baldosa acústica
Tabiquería de Drywall
Estructura metálica
TERRAZA
CUBICULO DE DOCENTES 401
CUBICULO DE DOCENTES 402
CUBICULO DE DOCENTES 403
CUBICULO DE DOCENTES 404
CUBICULO DE DOCENTES 406
CUBICULO DE DOCENTES 407
NPT:+9.70
Proyector
Switch
Pizarra acrílica
Marco de madera
LABORATORIO 301
LABORATORIO 302
LABORATORIO 303
LABORATORIO 304
LABORATORIO 305
LABORATORIO 306
NPT:+7.05
NPT:+6.60
NPT:+6.75
AULA ACADÉMICA - 201
AULA ACADÉMICA - 202
AULA ACADÉMICA - 203
NPT:+3.45
AULA ACADÉMICA - 101
AULA ACADÉMICA - 102
AULA ACADÉMICA - 103
NPT:+1.05
NPT:± 0.00
Vereda perimetral
NPT:+0.36
15.50
2.87
2.93
2.73
3.10
3.15
3.45
0.50
0.55
2.25
0.90
0.85
2.60
2.50
0.75
1.50
2.70
0.45
1.95
4.50
1.80

CORTE C - C´

ESC:1/75

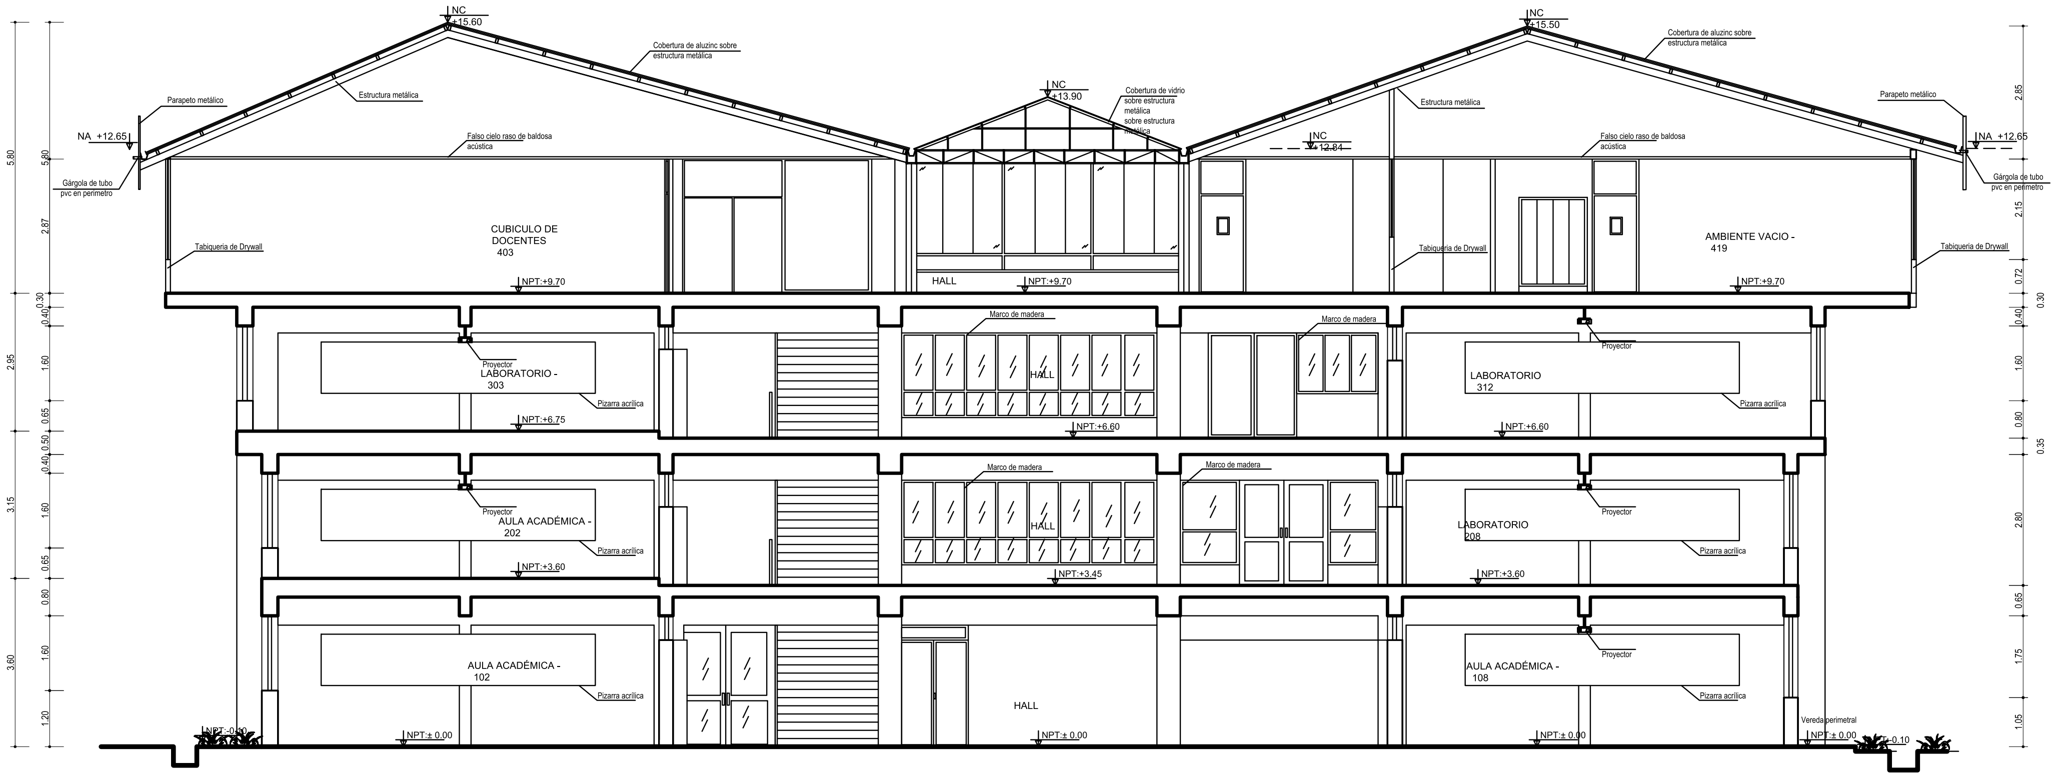
NC +15.60
NC +15.50
NC +13.90
NC +12.84
NA +12.65
Cobertura de aluzinc sobre estructura metálica
Cobertura de vidrio sobre estructura metálica sobre estructura metálica
Parapeto metálico
Estructura metálica
Falso cielo raso de baldosa acústica
Gárgola de tubo pvc en perimetro
Tabiquería de Drywall
CUBICULO DE DOCENTES 403
HALL
AMBIENTE VACIO - 419
NPT:+9.70
Marco de madera
Proyector
Pizarra acrílica
LABORATORIO - 303
LABORATORIO 312
NPT:+6.75
NPT:+6.60
AULA ACADÉMICA - 202
LABORATORIO 208
NPT:+3.60
NPT:+3.45
AULA ACADÉMICA - 102
AULA ACADÉMICA - 108
NPT:± 0.00
NPT:-0.10
Vereda perimetral
5.80
2.87
2.95
3.15
3.60
0.30
0.40
1.60
0.65
0.50
0.80
1.20
2.85
2.15
0.72
0.35
2.80
1.75
1.05

CORTE D - D´

ESC:1/75

gremsa
CONSULTORIA - OBRAS
INVERSIONES

LEVANTAMIENTO TOPOGRÁFICO INTEGRAL
DEL ESTADO ACTUAL A DETALLE DE LA
INFRAESTRUCTURA INTERIOR Y EXTERIOR
DE LA CIUDAD UNIVERSITARIA DE
PERAYOC-UNSAAC

PABELLON:
09. INFORMATICA Y SISTEMAS

PLANO:
CORTES

JEFE DE PROYECTO:
Arqto° JORGE SALCEDO QUISPE CAP 5812
EQUIPO TÉCNICO:
Arqto° AMED TEDILIO MOSCOSO TOLEDO CAP 13006
Arqta° NÉLIDA COANQUI SINCHI ROCA CAP 12517
Arqta° SOLANGE DIAZ CACERES CAP 12616
Arqta° VILMA CUSI DELGADO CAP 12615
Arqto° JUAN CARLOS PAUCAR VEGA CAP 11059
Bach. Arqta° JANIA CUSIQUISPE QUISPE
Bach. Arqto° DANDY BARRIENTOS RAMOS
Bach. Arqta° ADRIANA AIQUIPA ALOSILLA
Bach. Arqto° KENY CHOQUE INCACUTIPA
Asist. JONATAN CASAVERDE CCOICCA

UBICACION:
CIUDAD UNIVERSITARIA DE PERAYOC
Distrito : CUSCO
Provincia : CUSCO
Departamento : CUSCO

ESCALA:
INDICADAS

FECHA:
Cusco, Diciembre del 2016

LAMINA:
P-09
AR - 07

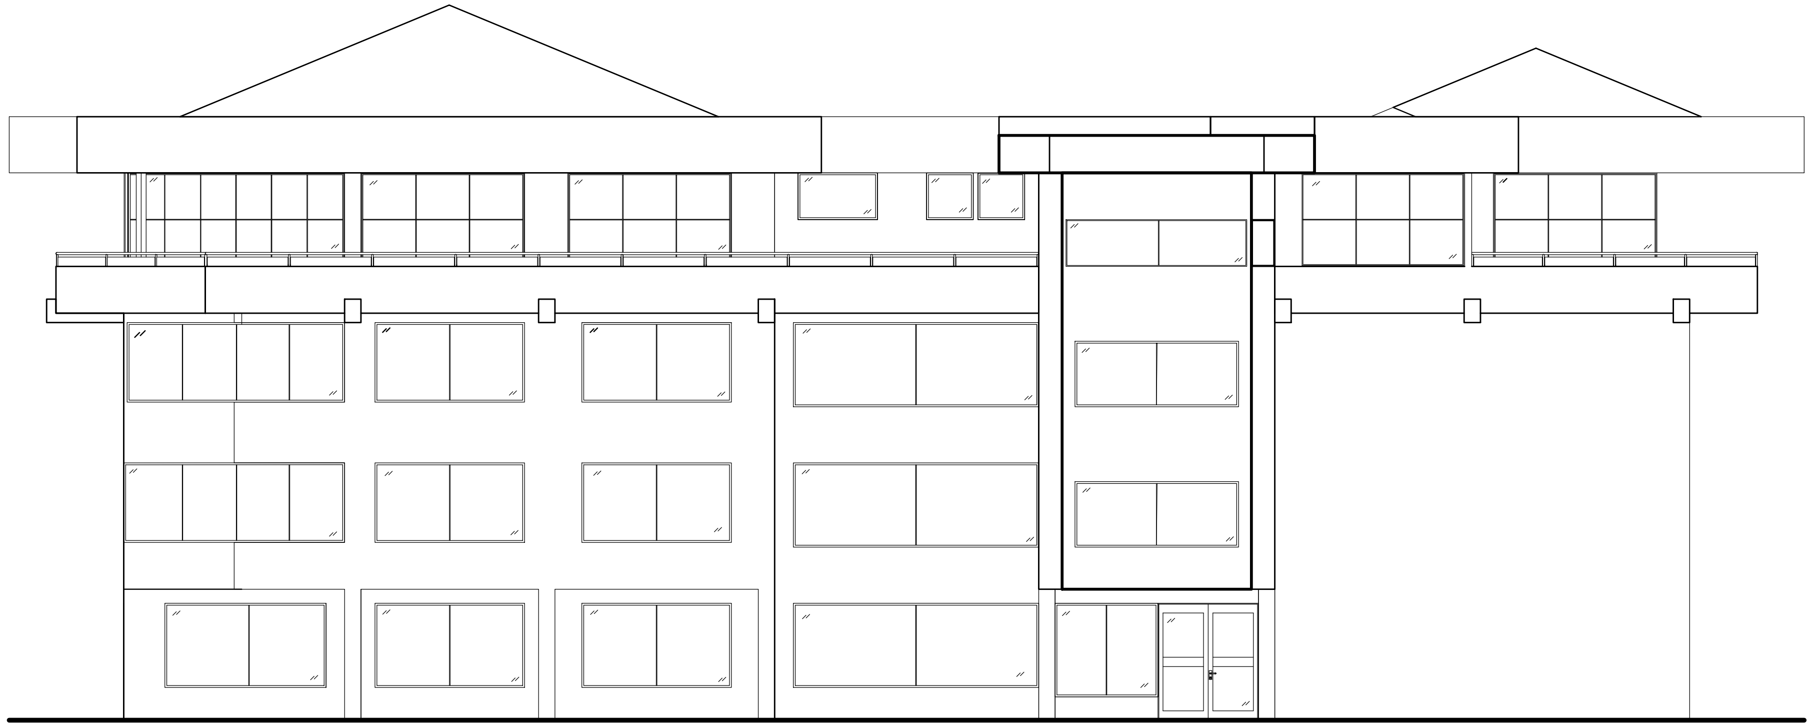

ELEVACIÓN FRONTAL
ESC:1/75

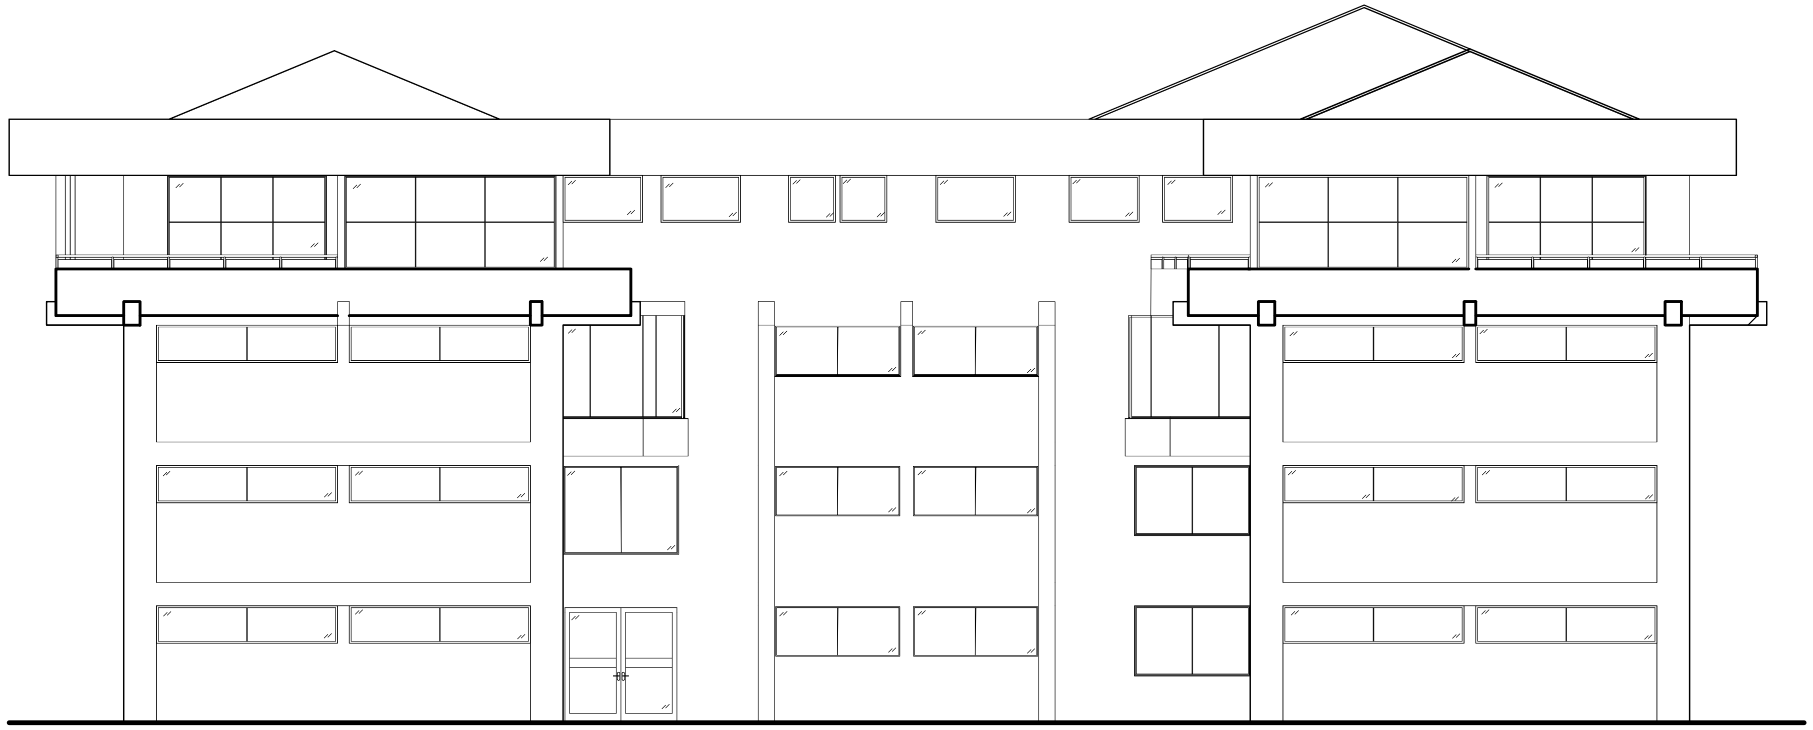

ELEVACIÓN POSTERIOR
ESC:1/75

gremsa
CONSULTORIA - OBRAS
INVERSIONES

LEVANTAMIENTO TOPOGRÁFICO INTEGRAL
DEL ESTADO ACTUAL A DETALLE DE LA
INFRAESTRUCTURA INTERIOR Y EXTERIOR
DE LA CIUDAD UNIVERSITARIA DE
PERAYOC-UNSAAC

PABELLON:
09. INFORMATICA Y SISTEMAS

PLANO:
ELEVACIONES

JEFE DE PROYECTO:
Arqto° JORGE SALCEDO QUISPE CAP 5812

EQUIPO TÉCNICO:
Arqto° AMED TEDILIO MOSCOSO TOLEDO CAP 13006
Arqta° NÉLIDA COANQUI SINCHI ROCA CAP 12517
Arqta° SOLANGE DIAZ CACERES CAP 12616
Arqta° VILMA CUSI DELGADO CAP 12615
Arqto° JUAN CARLOS PAUCAR VEGA CAP 11059
Bach. Arqta° JANIA CUSIQUISPE QUISPE
Bach. Arqto° DANDY BARRIENTOS RAMOS
Bach. Arqta° ADRIANA AIQUIPA ALOSILLA
Bach. Arqto° KENY CHOQUE INCACUTIPA
Asist. JHONATAN CASAVERDE CCOICCA

UBICACION:
CIUDAD UNIVERSITARIA DE PERAYOC
Distrito : CUSCO
Provincia : CUSCO
Departamento : CUSCO

ESCALA:
INDICADAS

FECHA:
Cusco, Diciembre del 2016

LAMINA:
P-09
AR - 08

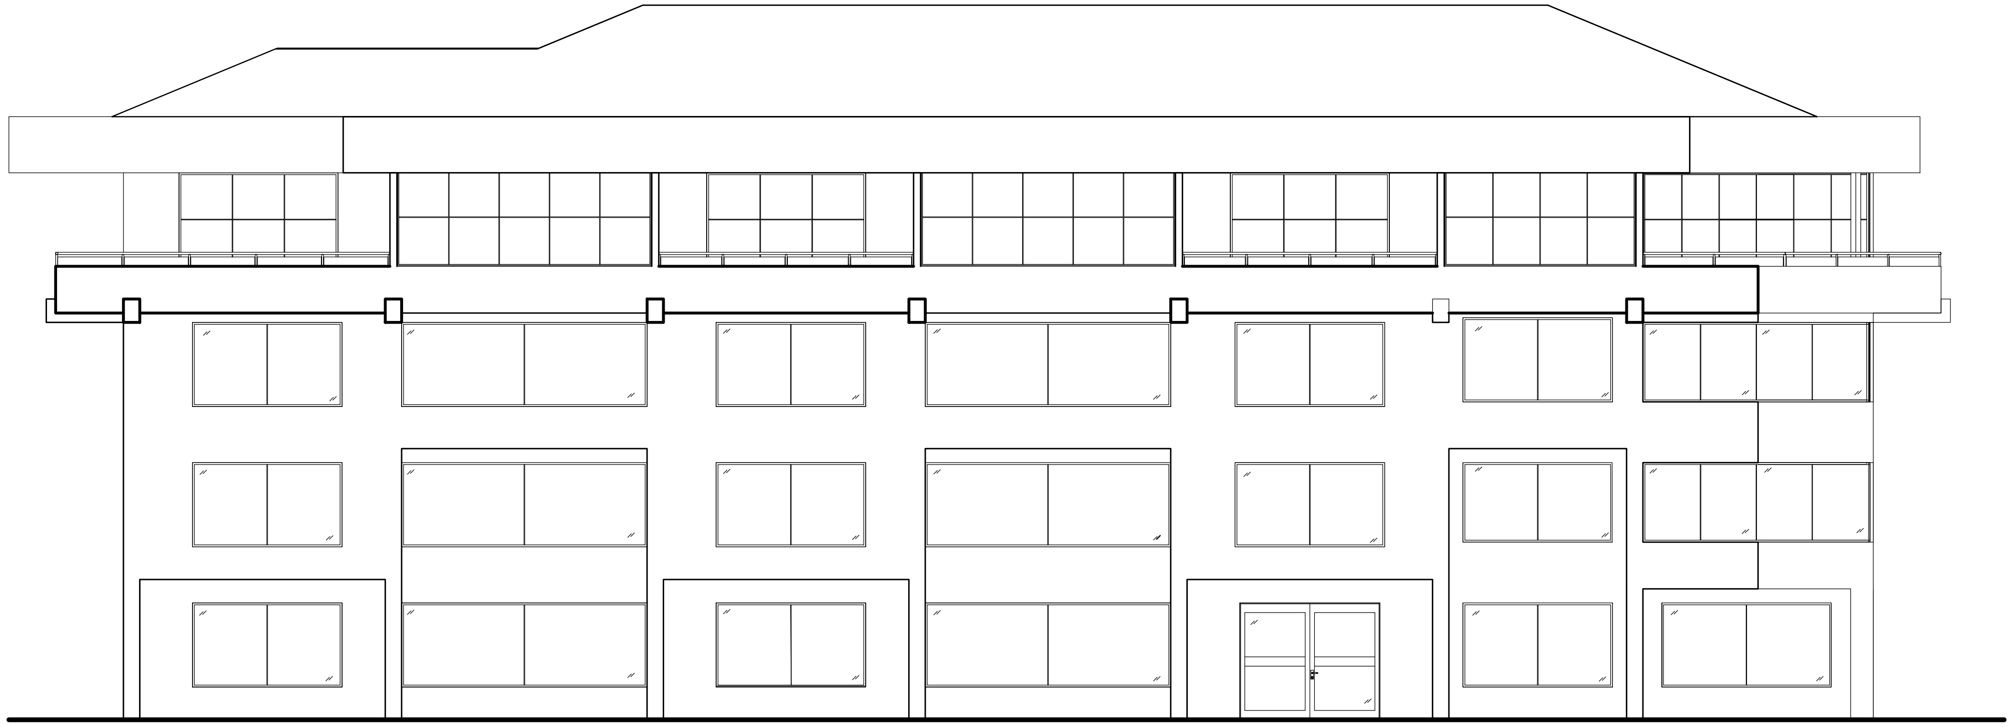

ELEVACIÓN LATERAL IZQUIERDA

ESC:1/75

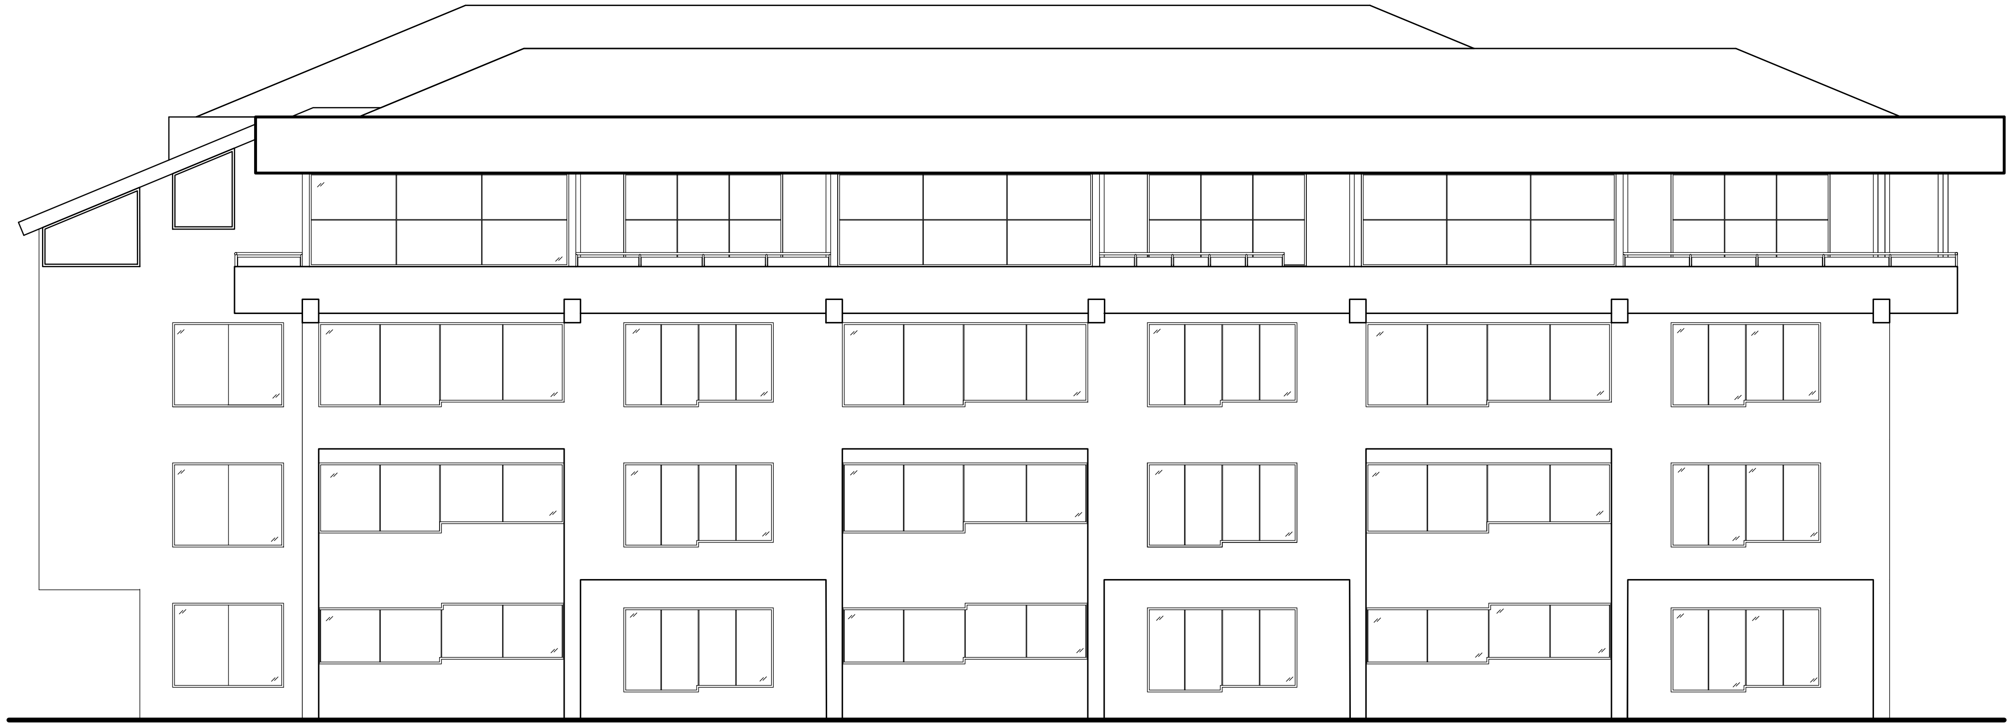

ELEVACIÓN LATERAL DERECHA

ESC:1/75

CONSULTORIA - OBRAS
INVERSIONES

LEVANTAMIENTO TOPOGRÁFICO INTEGRAL
DEL ESTADO ACTUAL A DETALLE DE LA
INFRAESTRUCTURA INTERIOR Y EXTERIOR
DE LA CIUDAD UNIVERSITARIA DE
PERAYOC-UNSAAC

PABELLON:
09. INFORMATICA Y SISTEMAS

PLANO:
ELEVACIONES

JEFE DE PROYECTO:
Arqto° JORGE SALCEDO QUISPE CAP 5812

EQUIPO TÉCNICO:
Arqto° AMED TEDILIO MOSCOSO TOLEDO CAP 13006
Arqta° NÉLIDA COANQUI SINCHI ROCA CAP 12517
Arqta° SOLANGE DIAZ CACERES CAP 12616
Arqta° VILMA CUSI DELGADO CAP 12615
Arqto° JUAN CARLOS PAUCAR VEGA CAP 11059
Bach. Arqta° JANIA CUSIQUISPE QUISPE
Bach. Arqto° DANDY BARRIENTOS RAMOS
Bach. Arqta° ADRIANA AIQUIPA ALOSILLA
Bach. Arqto° KENY CHOQUE INCACUTIPA
Asist. JHONATAN CASAVERDE CCOICCA

UBICACION:
CIUDAD UNIVERSITARIA DE PERAYOC
Distrito : CUSCO
Provincia : CUSCO
Departamento : CUSCO

ESCALA:
INDICADAS

FECHA:
Cusco, Diciembre del 2016

LAMINA:
P-09
AR - 09